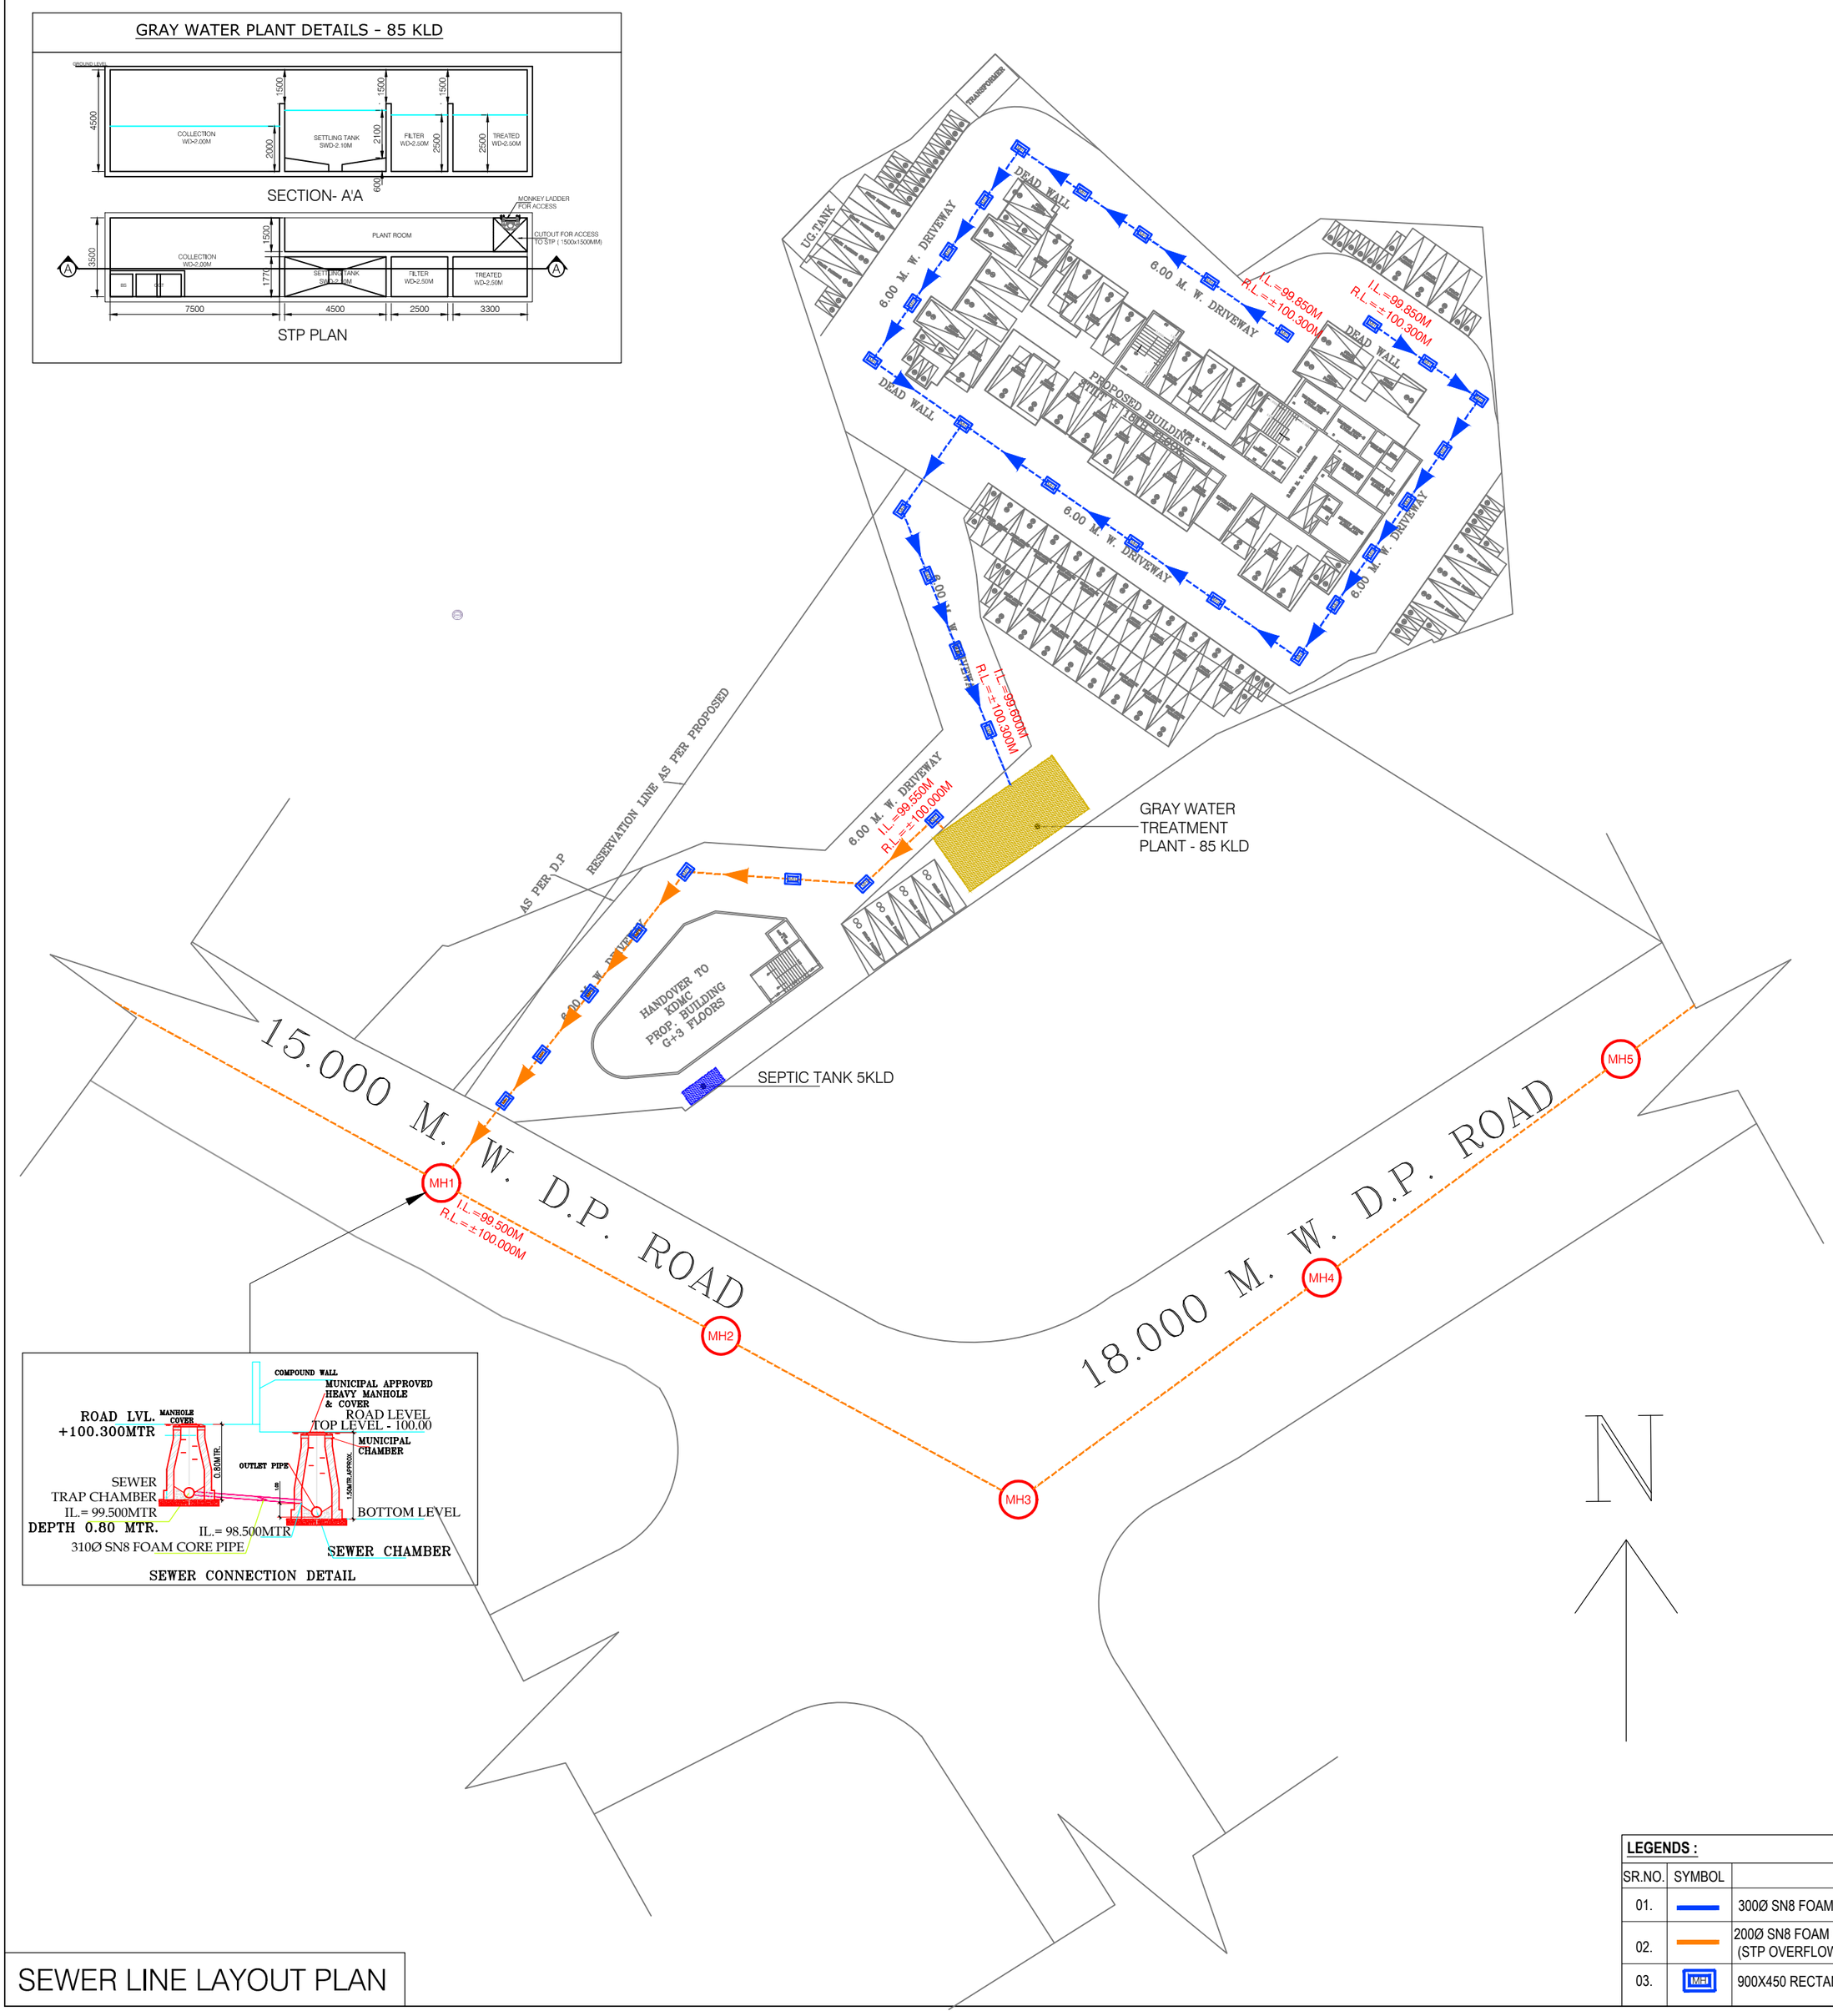

ELCON ENGINEERS DOMBIVLI

Digitally signed by SUBODH GOTHOSKAR
DN: c=IN, o=PERSONAL, title=2743, pseudonym=a6b2cf06642f4e609443a721bd66f67f, 2.5.4.20=183ac62810c4ef7a873fc39d4297045bd3a4e2852f3a34bf1bd70cb479d7ad8a, postalCode=421301, st=Maharashtra, serialNumber=ef390763b4f8c69191fe25800f5aca39ca0755c25ec0b0546949141687dd8988, cn=SUBODH GOTHOSKAR
Date: 2026.03.04 12:54:32 +05'30'

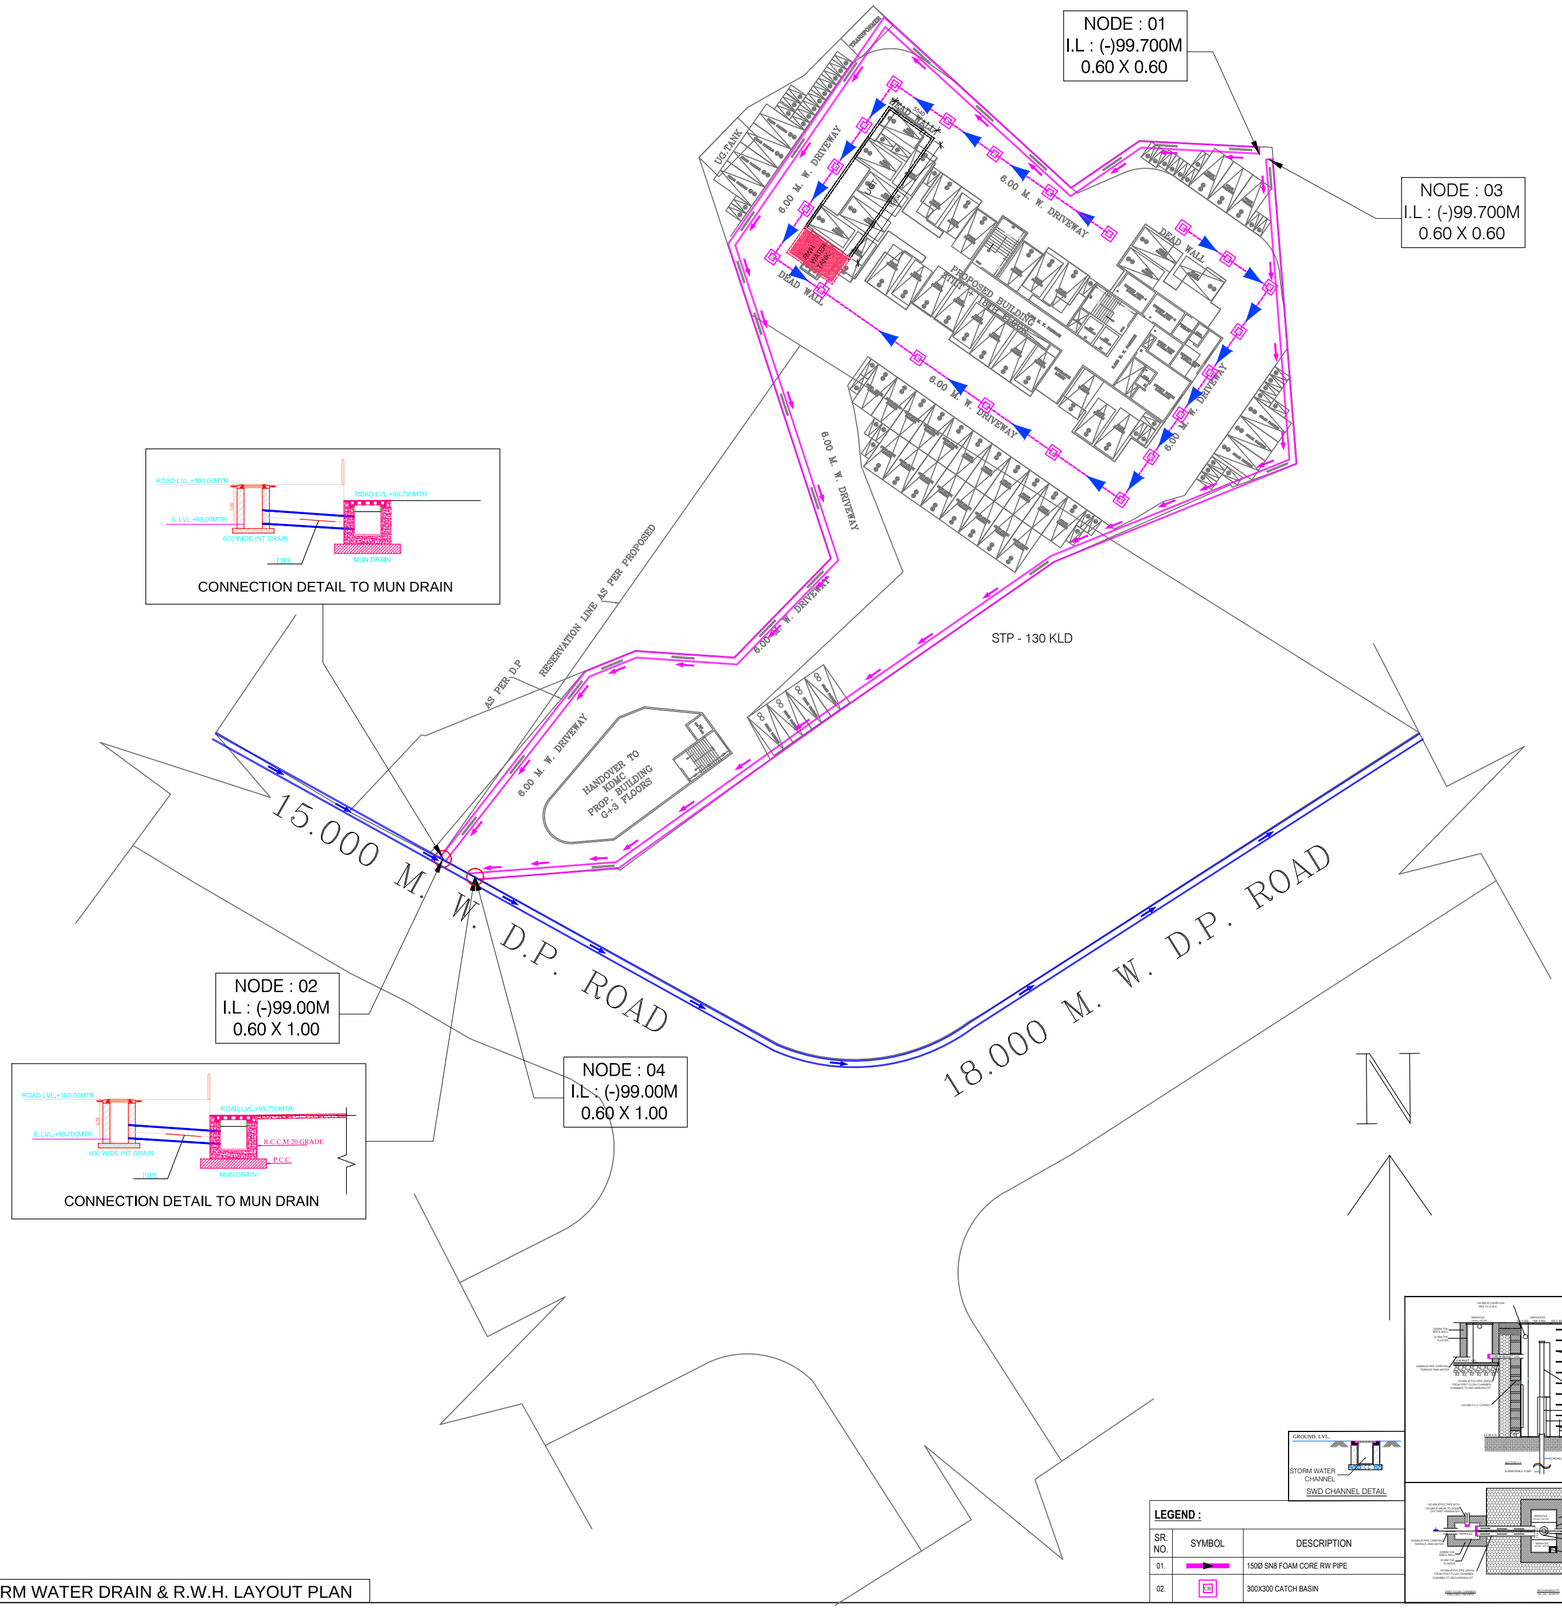

STORM WATER DRAIN & R.W.H. LAYOUT PLAN

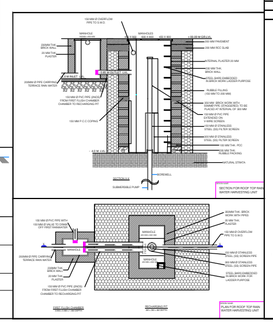

SWD CHANNEL DETAIL

LEGEND :

SR. NO.	SYMBOL	DESCRIPTION
01.		150Ø SN8 FOAM CORE RW PIPE
02.		300X300 CATCH BASIN

TECHNICAL SPECIFICATIONS

DIA IN INCH	MOC	SLOT SIZE IN MM	TOTAL LENGTH OF SCREEN SINGLE PIECE	TOTAL LENGTH OF SCREEN WITH END CONNECTION
6"	SS 304	00.50	1.0 MT.	1.9 MT.
12"	SS 304	00.75	1.0 MT.	1.8 MT.

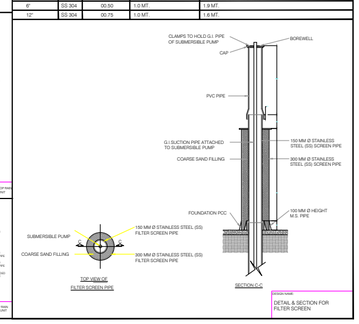

ELCON ENGINEERS DOMBIVLI

Digitally signed by SUBODH GOTHOSKAR
DN: c=IN, o=PERSONAL, title=2743, pseudonym=a6b2cf06642f4e609443a721bd6e8b7f, 2.5.4.20=183ac62810c4ef7a8735c39d42970545bf5a9e2852f3d34bf1bd7b0c647bd7ad8a, postalCode=421301, st=Maharashtra, serialNumber=ef39b7b3b4f8c691919b25800f5ac639ca075c25ec0b054649491416d7dd8988, cn=SUBODH GOTHOSKAR
Date: 2026.02.26 18:36:31 +05'30'