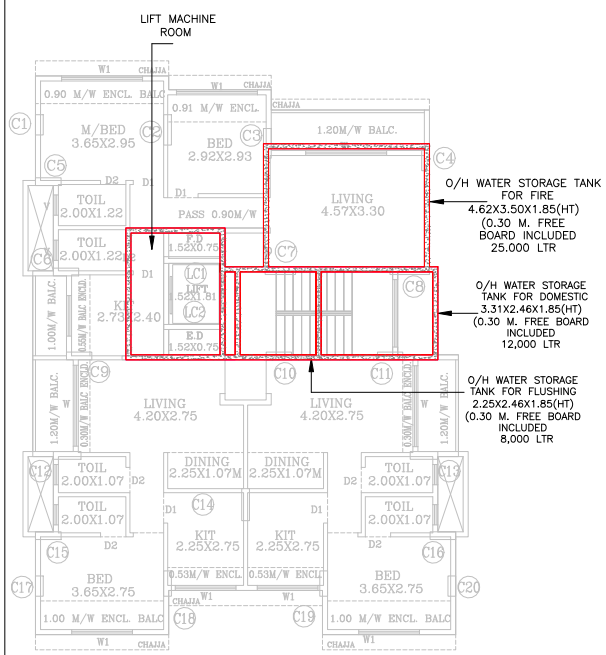

TYPICAL FLOOR PLAN
1ST TO 7TH FLOOR
SCALE 1:100

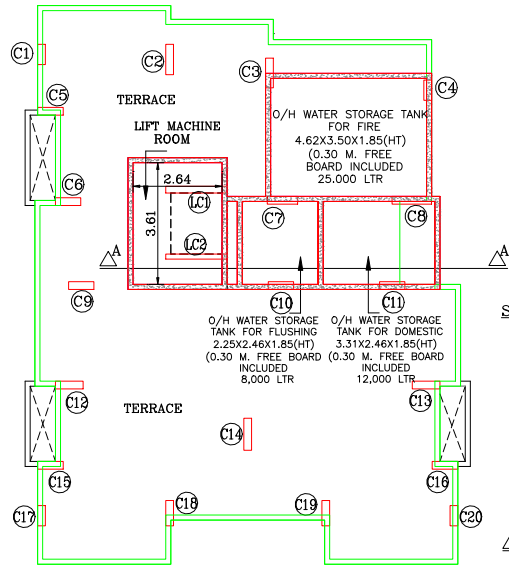

TERRACE FLOOR PLAN

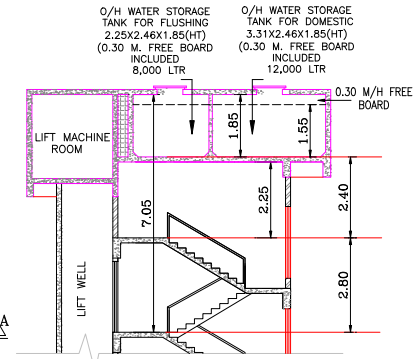

SECTION OF O/H TANK & LIFT MACHINE ROOM
SECTION A–A

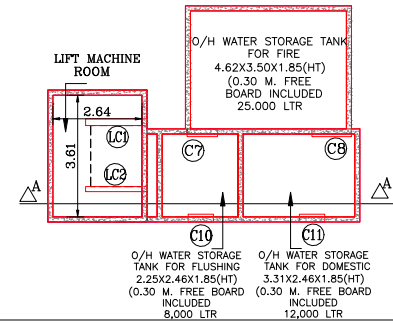

STAMPS OF APPROVAL OF PLANS:

SHEET NO.:– 01

Signature
(Name of Architect/ Licensed Engineer/ Supervisor.)

DESCRIPTION OF PROPOSAL AND PROPERTY

PROPOSED RESIDENTIAL BUILDING ON PLOT BEARING S.NO– 111 H.NO– 16 E PLOT NO 23 A. AT TRIMURTY CO–OP HSG SOCIETY LTD, VILLAGE CHOLE, DOMBIVLI (WEST), TALUKA KALYAN.

For,

Mr:–SHASHIKANT YASHWANT JADHAV & OTHERS (OWNER)

Mr. PAWAN POTDAR (P.A.HOLDER)

Mr. SURAJ GOSWAMI (P.A.HOLDER)

Mr. PUNIT INGLE (P.A.HOLDER)

M/S AVIGHNA GROUP.

DRG. SH. NO.	SCALE	DESIGN BY	DRAWN BY	CHECKED BY
01	AS STATED	---		

SIGNATURE OF ARCHITECT	NAME AND ADDRES OF ARCHITECT
	RACHANA SHILP C.A. NO. 198 4 /0 8 6 2 3 R.C. MODAK Sreeji Arcade, First Floor, Above H.D.F.C.Bank, Phadke Cross Road, Dombivli (E)