SAIRAJ PETROLIUM

BUILDING	FLOORS	FSI AREA						BALCONY	TERRACE	LIFT	LIFTWELL	DUCT	VENT	OTHER	TOTAL
		COMM.	RESI.	IND.	EDU.	INS.	MEZZ.	PROP.					SHAFT	DEDUCTION	FSI AREA
SAIRAJ PETROLIUM	GROUND FLOOR	24.75	0.00	0.00	0.00	0.00	0.00	0.00	0.00	0.00	0.00	0.00	0.00	0.00	24.76
SAIRAJ PETROLIUM	1ST FLOOR	24.75	0.00	0.00	0.00	0.00	0.00	0.00	0.00	0.00	0.00	0.00	0.00	0.00	24.76
SAIRAJ PETROLIUM	TOTAL	49.50	0.00	0.00	0.00	0.00	0.00	0.00	0.00	0.00	0.00	0.00	0.00	0.00	49.52

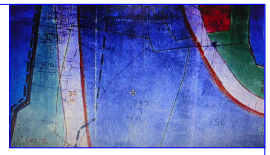

FSI DETAILS

9 Index	Basic FSI (on serial no 1)	Premium FSI (on serial no 1)	TDR (on serial no 1)	Incentive FSI for green building If Applicable (on basic FSI)	Ancillary Area 60% of (2+3+4+5)	Ancillary Area 80% of (2+3+4+5)	Total	Inclusive Housing (20%) If Applicable	Drawing Value
9.1 Permissible Index	0.25	0.50	1.40	0.00	0.00	0.00	2.15	0.00	0.00
9.2 Existing Comsumed Index	0.00	0.00	0.00	0.00	0.00	0.00	0.00	0.00	0.00
9.3 Balance Index to be Consumed	0.25	0.50	1.40	0.00	0.00	0.00	0.00	0.00	0.00
9.4 Total Permissible PLine Area	223.00	446.00	1248.80	0.00	0.00	39.60	1957.40	0.00	0.00
9.5 Proposed P Line Area (Should not exceed 9.4)	49.52	0.00	0.00	0.00	0.00	0.00	49.52	0.00	49.52
9.6 Index Consumed	0.06	0.00	0.00	0.00	0.00	0.00	0.06	0.00	0.00

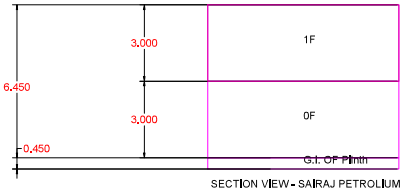

SECTION VIEW - SAIRAJ PETROLIUM

PARKING STATEMENT CAR PARKING PER UDCPR

TYPE	NO.OF OFFICE	REQUIRED CAR 100%	ADDITIONAL 5% VISITOR CARS	100% CAR REQUIRED	REQUIRED CARS 80%	PROPOSED CARS
OFFICE AREA	30.15 SQ.MT.	0.45 NO.		0.45 NO.	0.36 NO.	01 NO.
TOTAL CAR PROPOSED FOR OFFICE					0.36 NO.	01 NOS.

PARKING STATEMENT SCOOTER PARKING PER UDCPR

TYPE	NO.OF OFFICE	REQUIRED SCO. 100%	ADDITIONAL 5% VISITOR SCO.	100% SCO. REQUIRED	REQUIRED SCO.80%	PROPOSED SCOOTER
OFFICE AREA	30.15 SQ.MT	1.66 NO.		1.66 NO.	1.32 NO.	02 NO.
TOTAL SCOOTER PROPOSED FOR OFFICE					1.32 NO.	02 NOS.

F.S.I. & NON F.S.I. AREA CALCULATION

TOTAL SUMMARY STATEMENT

AREA	AREA IN SQ.MT.
BUILT UP AREA	49.52
CANOPY AREA	168.00
TOTAL	217.52

SITE UNDER REFERANCE

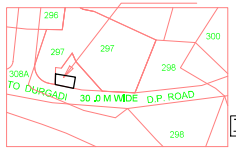

LOCATION PLAN
SCALE 1 : 5000

GROUND & 1ST FLOOR AREA CALCULATION

A = 7.50 x 4.05 = 30.38 SQ.MT.
DEDUCTIONS
1 = 5.35 x 1.05 = 5.62

TOTAL DEDUCTIONS = 5.62 SQ.MT.
GROUND FLOOR AREA = 24.76 SQ.MT.

BUILT UP AREA STATEMENT

FLOOR	IN SQ.MT.
GROUND FLOOR	24.76
FIRST FLOOR	24.76
TOTAL AREA	49.52

TOTAL HEIGHT OFFICE BLDG. 6.45 MT.

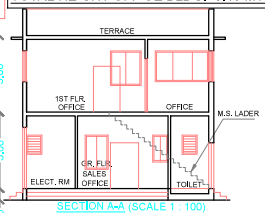

SECTION A-A (SCALE 1 : 100)

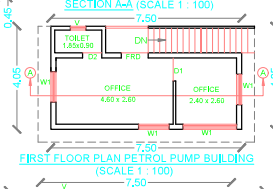

FIRST FLOOR PLAN PETROL PUMP BUILDING
(SCALE 1 : 100)

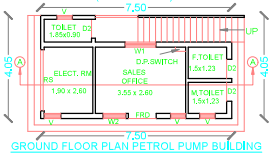

GROUND FLOOR PLAN PETROL PUMP BUILDING
(SCALE 1 : 100)

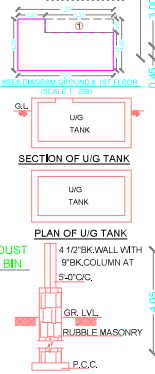

TYPICAL SECTION OF COMPOUND WALL.

STAMP OF APPROVAL OF PLAN | SHEET NO. 01/01

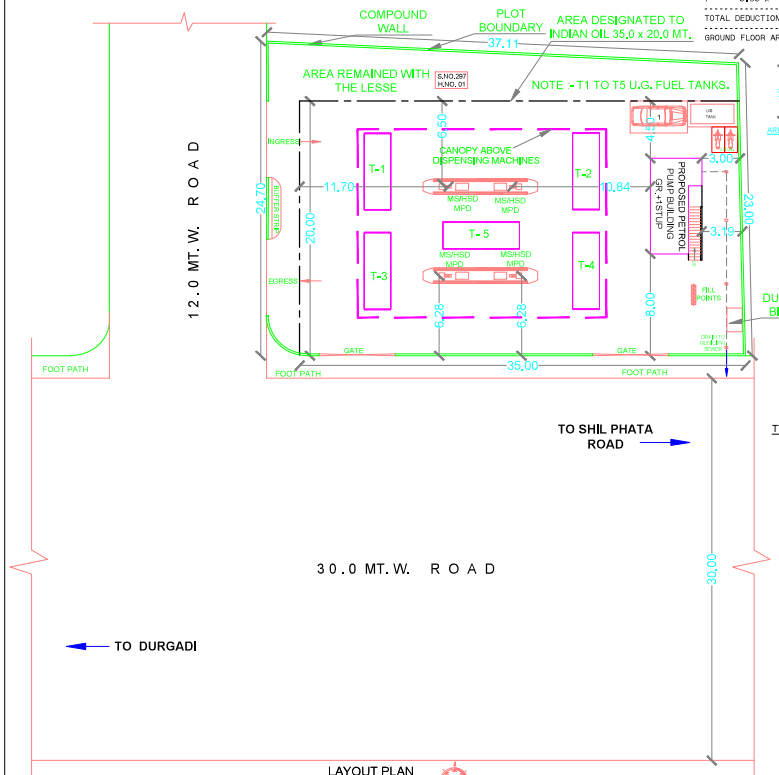

LAYOUT PLAN
(SCALE 1 : 200)

NOTES

1 PLOT SHOWN IN THICK BLACK
2 EXISTING STREET GREEN
3 PROPOSED WORK RED FILLED IN
4 DRAINAGE & SEWERAGE WORK RED DOTTED
5 ROAD AND SET BACK BURNT SIENNA
6 A.P.ARCHITECTURAL PROJECTION 0.75 MT.W.

DOOR & WINDOW SCHEDULE:

FRD	T.W. PANELLED DOOR.	1.05 X 2.10 M.
D1	T.W. FLUSH DOOR.	0.90 X 2.10 M.
D2	T.W. FLUSH DOOR.	0.75 X 1.80 M.
W1	T.W. SHUTTER GLAZED	1.50 X 1.20 M.
W2	T.W. SHUTTERED GLAZED	1.20 X 1.20 M.
V	LOUVERED WINDOW	0.60 X 0.75 M.

CERTIFICATE FOR AREA.

CERTIFICATE THAT THE PLOT UNDER REFERENCE WAS GOT SURVED BY ME ON DT 10/02/24 AND THE DIMENSIONS OF SIDES ETC. OF PLOT STATED ON PLANS ARE AS MEASURED ON SITE AND THE AREA SO WORKED 892.00 SQ.MT. AND TALLIES WITH THE AREA STATED IN DOCUMENT OF OWNERSHIP / T.P. RECORD.

SIGN. OF ARCHITECT

PROPOSED PETROL PUMP PLAN ON PLOT BEARING S.NO.297 H.NO. 01 AT VIL. - KALYAN , TAL.- KALYAN , DIST.-THANE.
FOR.
MR. KIRAN ANKUSH PATIL
MR. KIRAN ANKUSH PATIL

SIGNATURE OF P.O.A.

STAMP OF APPROVAL OF PLAN

SHEET NO. 01/01

PROFORMA - I

A		AREA STATEMENT.	SQ. MTS.
1	a	TOTAL AREA OF PLOT	160542.39
	b	NET AREA OF PLOT	139531.39
	c	AREA OF PLOT ALLOTTED BY APMC	892.00
	d	AREA OF PLOT UNDER CONSIDERATION (1c)	892.00
	e	AS PER SITE	892.00
2		DEDUCTION FOR	
	a	AREA NOT IN POSSESSION	NIL.
	b	SET-BACK AREA 30. MT. W. ROAD	NIL.
	c	TOTAL (2a - 2b)	NIL.
3	a	BALANCE AREA OF PLOT (2c)	892.00
4		AMENITY SPACE 5% OF	NIL.
	a	REQUIRED	NIL.
	b	ADJUSTMENT OF 2(b), IF ANY	N.A.
	c	BALANCE PROPOSED	N.A.
5		NET PLOT AREA (3a - 4c)	892.00
6		RECREATIONAL OPEN SPACE (IF APPLICABLE)	N.A.
	a	REQUIRED 10%	N.A.
7		INTERNAL ROAD AREA	NIL.
8		PLOT ABLE AREA (5)	892.00
9		BUILT UP AREA WITH REFERENCE TO BASIC F.S.I. AS PER (6.2.2 F.S.I. PERMISSIBLE) = 892.00 x 0.25	223.00
10		ADDITION OF F.S.I. ON PAYMENT OF PREMIUM	N.A.
11		IN SITU FSI / T.D.R. LOADING	N.A.
12		ADDITION FSI AREA UNDER CHAPTER NO. 7	NIL.
13		TOTAL ENTITLEMENT OF FSI IN THE PROPOSAL	
	a	[9] OR 12 WHICHEVER IS APPLICABLE = (223.00)	223.00
	b	ANCILLARY AREA FSI UPTO 60% WITH PAYMENT OF CHARGES OF BALANCE BUILT UP AREA	NIL.
	c	TOTAL ENTITLEMENT (13a+13b)	223.00
14		MAXIMUM UTILIZATION LIMIT OF F.S.I. (OTHER BUILDING) PERMISSIBLE(AS PER REGULATION NO. 6.2.2 APPLICABLE)= 0.25	0.25
15		TOTAL PERMISSIBLE BULT-UP AREA IN PROPOSAL (13c)	223.00
	a	EXISTING BULT-UP AREA	NIL.
	b	PROPOSED BULT-UP AREA (AS PER 'P-LINE')	49.52
	c	TOTAL (a + b) =	49.52
16		F.S.I. CONSUMED 15c/3a	0.038
17		AREA FOR INCLUSIVE HOUSING	NIL.
		TENEMENT STATEMENT.	
	a	PROPOSED BULT-UP AREA	49.52
	b	LESS DEDUCTION OF NON RES AREA(SHOPS ECT.)	NIL.

SIGNATURE

NAME OF R.C.C CONSULTANT

SATISH KANADE
ARCHITECT
CA/82/6998

ARCHITECTS INC.
SIDDHI APTS , GR.FLOOR ,
OPP LOURDES CHURCH ,
MURBAD ROAD , KALYAN.

DRN BY	CHKD BY	DATE	DRG. NO	JOB NO
TAUHID	S.V. KANADE	30/07/2024	MA-1	K -

Signature valid

Digitally signed by Surendra Pandurang Jangle
Date: 2024.11.28 16:53:57 IST
Reason: Approved Building Plan
Designation : Assistant Director of Town Planning
Location: Kalyan Dombivli Municipal Corporation
Project Code : KDMCC-
Application Number : KDMCC/BP/2400102
Proposal Number : 260019
Certificate Number : KDMCC/B/2024/APL/00831

EXECUTIVE ENGINEER/TOWN DEVELOPMENT OFFICER
Date: 28/11/2024

Town Planner
Date: 28/11/2024

Assistant Town Planner
Date: 28/11/2024

Assistant Engineer
Date: 28/11/2024

Proforma I Area Statement	
1. Area of plot (Minimum area of a, b, c to be considered) or area of subplot with sanctioned layout No. and subplot No.	892.00
(a) As per ownership document (7/12, CTS extract)	892.00
(b) as per TILR or City Survey measurement sheet	892.00
(c) as per Demarcated drawing area	892.00
LESS	
2.Area not in possession	0.00
3. Entire area (1-2)	892.00
4.Deductions for	-
(a) Proposed D.P./ D.P. Road widening Area /Service Road / Highway widening	0.00
(b) Any D.P. Reservation area	0.00
(Total a+b)	0.00
5.Balance area of plot (3-4)	892.00
6. Amenity Space	0.00
(Applicable if (1) > 20000 sqmt	-
(Required -(a) Upto 20000 sqmt - Nil	-
(b) Above 20000 sqmt - (a) + 5 % of Total area	0.00
7. Net Plot Area (5-6)	892.00
8. Recreational Open Space	-
(a) If area (6) is more than 4000 sqmt - 10 % of (6) is required.	0.00
Proposed	0.00
(b) If area is less than 4000 sqmt -Check -	-
i) If it is full number like 1,2,125,419 etc. As per 7.12 /abstract or City Survey Number - No Recreational open space is required	-
ii) If it is subdivision like 1/2 ,2/5 , 125/1 419/1 etc.then recreational open space is required.	-
(A) 10 % Subject to minimum 200 sqmt	0.00
Proposed	0.00
(B) Exemption to leave open space subject to availing basic F.S.I. of 75 %	-
(C) Exemption to leave open space subject to payment of 10 % land value of land at (7) as per annual statement of rate.	-

Certificate of Area:
Certified that the plot under reference was surveyed by me on 2024-04-01 and the dimensions of sides etc. of plot stated onplan are as measured on site and the area so worked out tallies with the area stated in document of Ownership/ T.P. Scheme Records/Land Records Department/City Survey records.
Signature
(Name of Architect/ Licensed Engineer/ Supervisor.)

Owner's Declaration -
I/We undersigned hereby confirm that I/We would abide by plans approved by Authority / Collector. I/We would execute the structure as per approved plans. Also I/We would execute the work under supervision of proper technical person so as to ensure the quality and safety at the work site.

Owner (s) name and signature

Architect/ Licensed Engineer/ Supervisor name and signature

Job No.

Name Of : Owner KIRAN ANKUSH PATIL

Postal Address : ROOM NO.822 VITHAI NIWAS NEAR L.I.G 1/47 OPP BIRLA COLLEGE,PATIL NAGAR CHIKANGHAR,KALYAN WEST,Thane,Maharashtra-421301
Phone No.:8652857432

DESCRIPTION OF PROJECT :

Type of Proposal : Commercial
BUILDING ON CTS. NO./SURVEY NO.- 297

SITE ADDRESS :
PRO PETROL PUMP PLAN ON PLOT BEARING S.NO.297 H.NO. 01 AT VIL.- KALYAN , TAL.- KALYAN ,

Name Of Architect : Mr.Satish V. Kanade

LOGO

ADDRESS OF OFFICE
OFFICE -
Ground Floor Ashirwad Apt, Next To Hotel Ambika Near Railway Station Badalpur (E)

OWNERS SIGN - Verified by applicant

TECHNICAL PERSON SIGN
Signature valid

SCALE - 1:100 | Date : 18/04/24
JOB NO - KDMCC-24-39620 | CHECK BY - -

SUBMISSION DRAWING