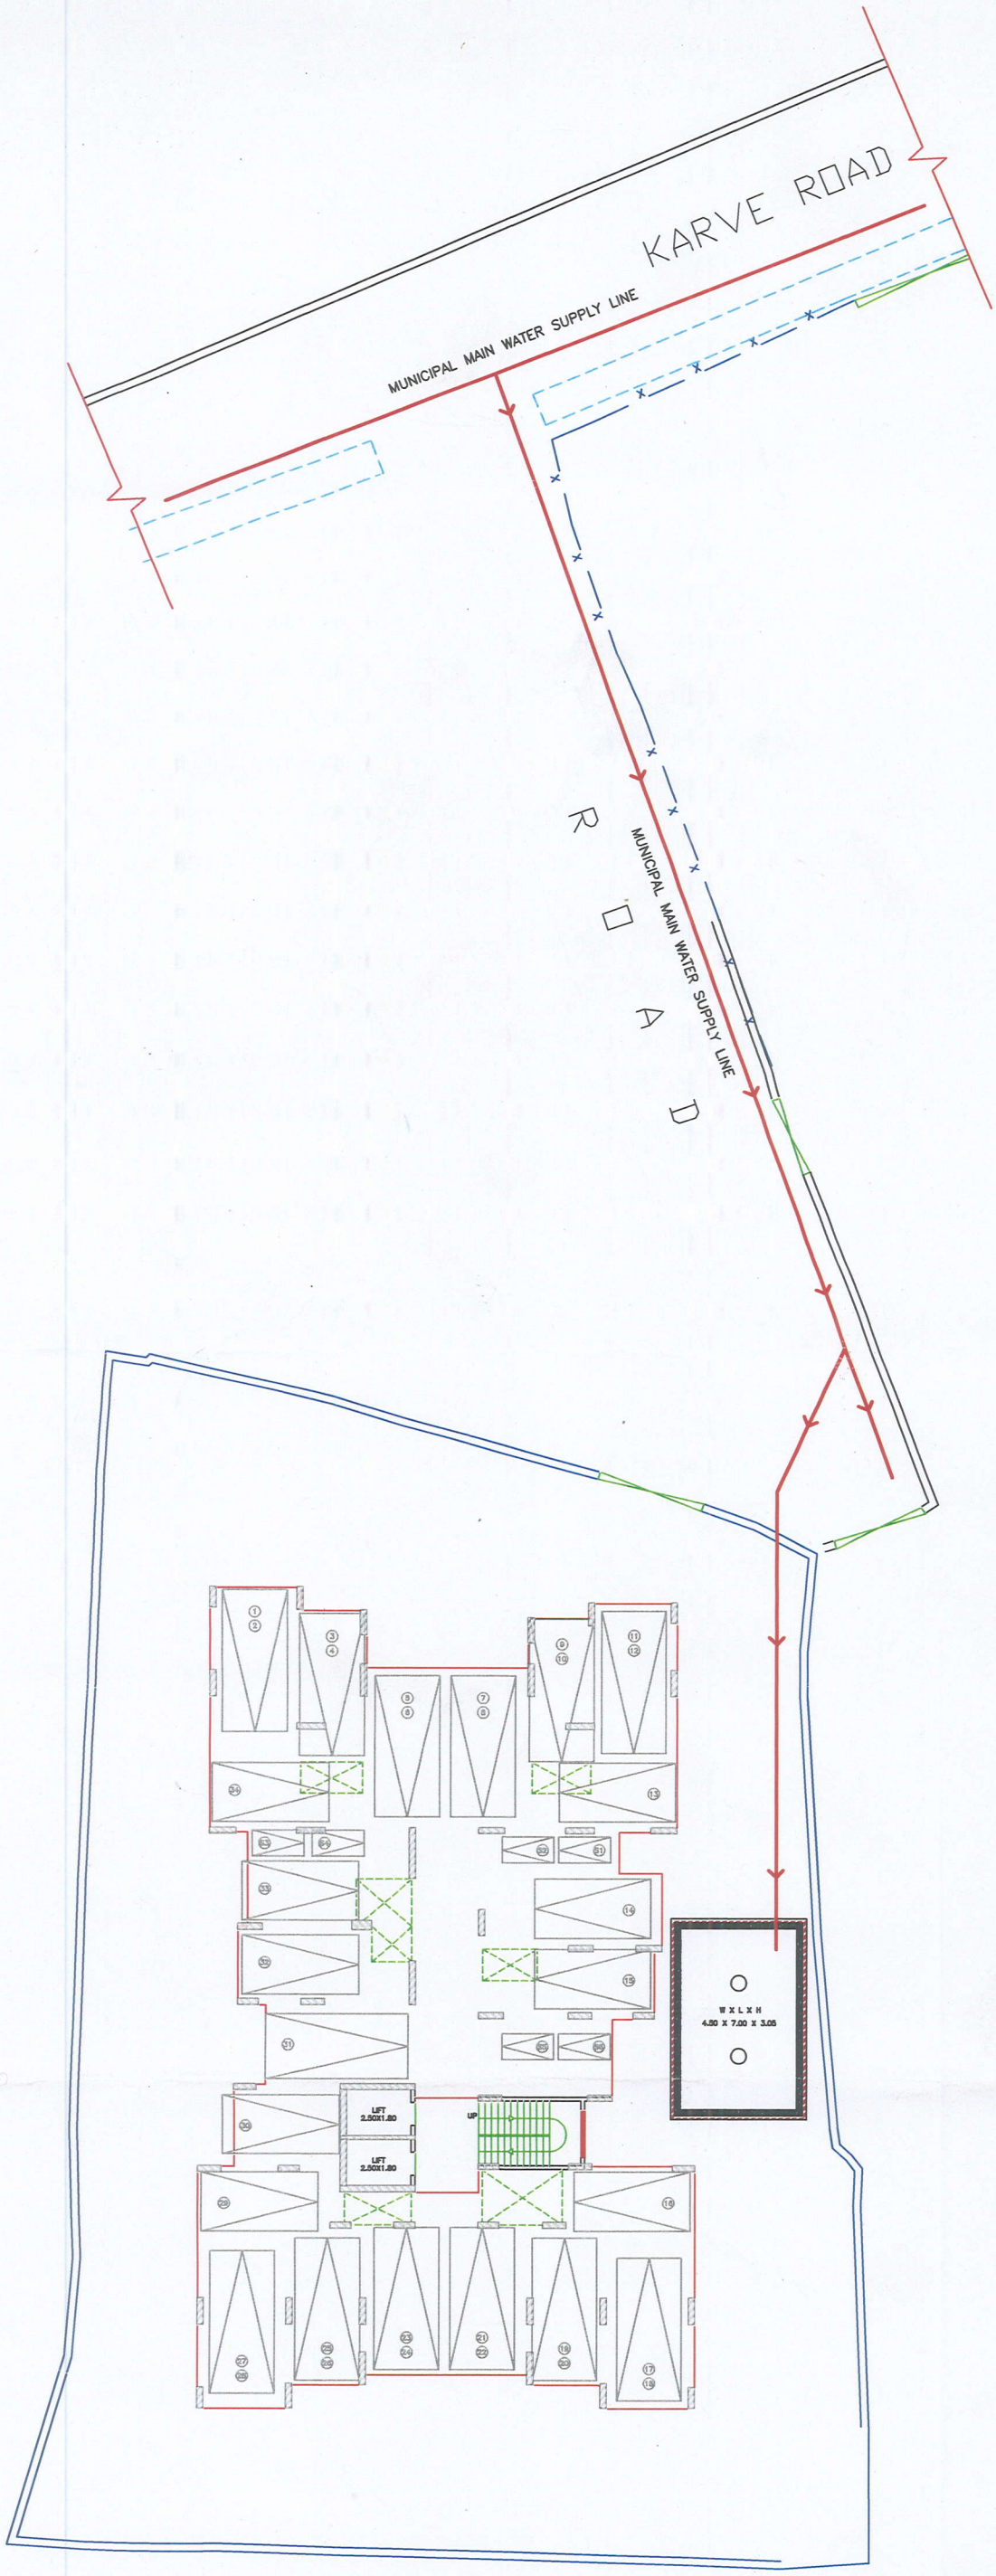

WATER SUPPLY LAYOUT PLAN

कल्याण डोंबिवली महानगरपालिका
पाणी पुरवठा विभाग
नळ कारागीर परवाना
दिपक गंगाराम दांडेकर
परवाना क्र. KDMC/WS/PL NO./242
सही :-

DESCRIPTION OF PROPOSAL AND PROPORTY
PROPOSED RESI BLDG. ON PLOT BEARING, C.T.S.NO. 2319 & 2320, VILLAGE – NAVAGAON DOMBIVLI (W)TALUKA – KALYAN, DIST. – THANE.
PLOT AREA – 994.30 SQ.MT.
NUMBER OF FLAT – 40 FLATS
UNDER GROUND WATER TANK CAPACITY – 96075.00 LTR
OVER HAND WATER TANK CAPACITY – 44883.00 LTR.
FIRE TANK CAPACITY (LTR) 25200.00 LTR.
OWNER'S SIGNATURE & STAMP : –
Evergreen Developers M/S EVERGREEN DEVELOPERS P.O.A. HOLDER – SACHIN CHITNIS & OTHERS Partner
PLUMBER'S SIGNATURE & STAMP : –
NAME AND ADDRESS OF ARCHITECT
ARCHITECT: UDAY M. CHOPDA CA/2017/88339 UC ASSOCIATES ARCHITECT & INTERIOR DESIGNER
A/202, SARVODAY AANGAN, PANDURANG WADI, NEAR SAI BABA TEMPLE, MANPADA ROAD, DOMBIVLI (EAST) – 421201. EMAIL : ucassociates29@gmail.com MOB : 7666283464