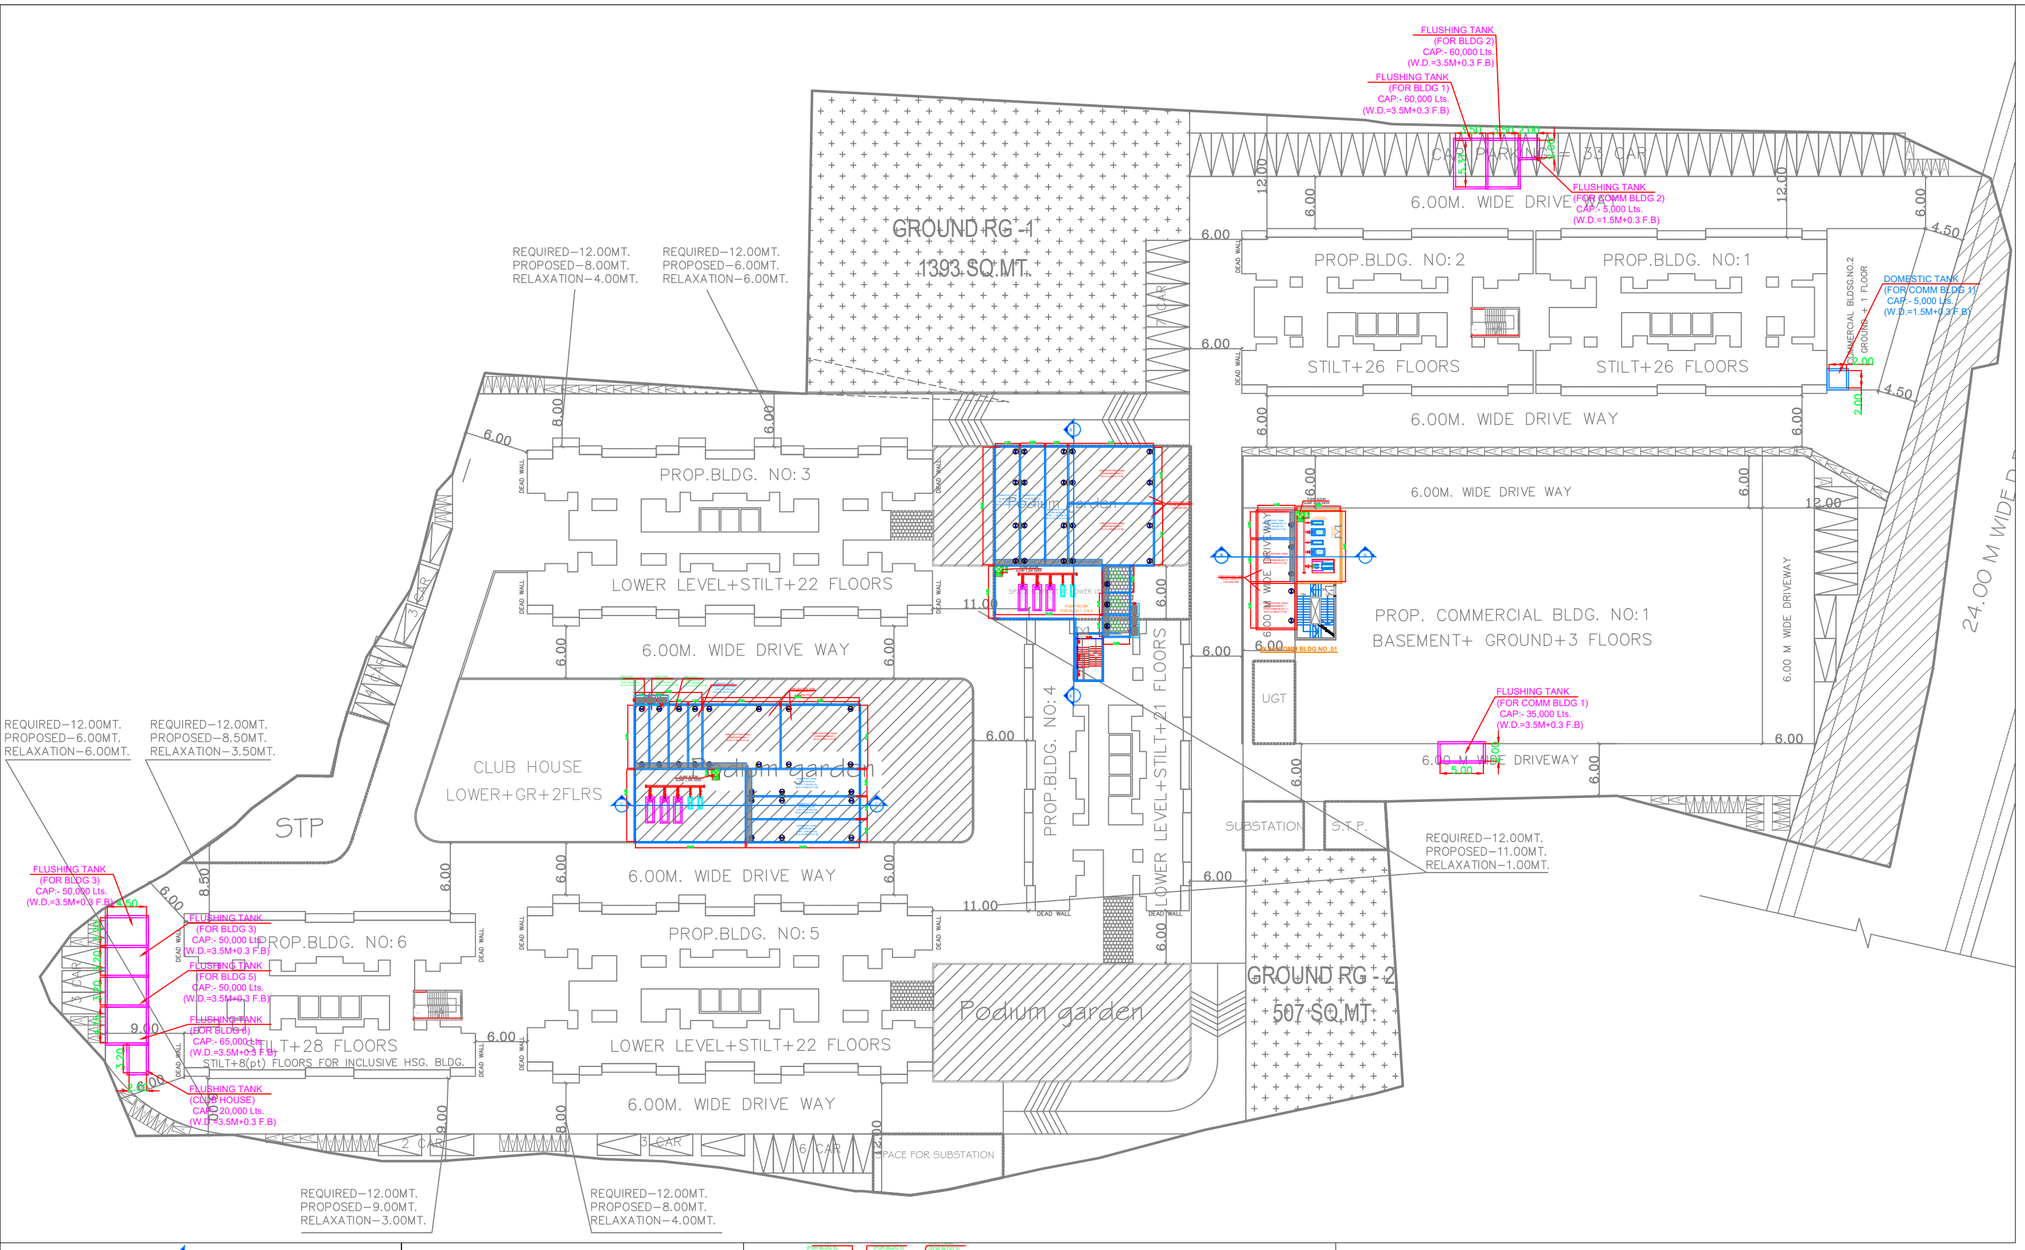

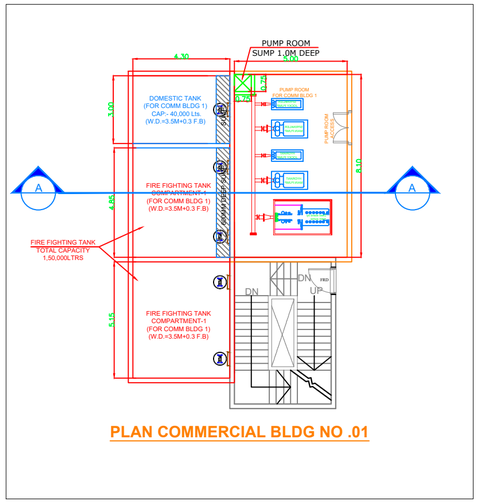

PLAN COMMERCIAL BLDG NO .01

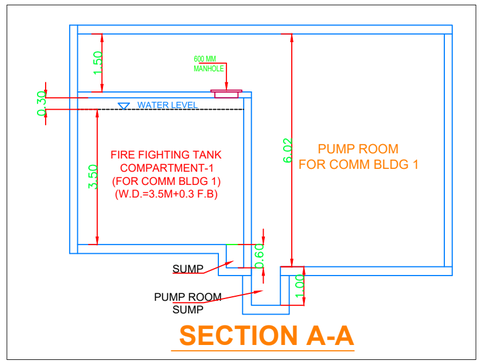

SECTION A-A

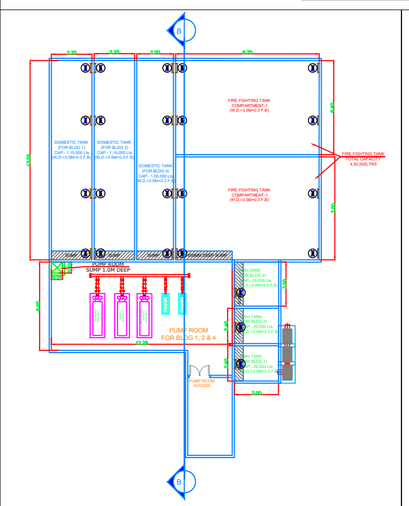

PLAN BLDG NO .01,02 & 04

SECTION B-B

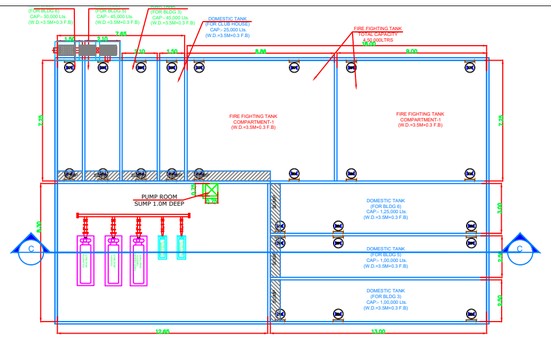

PLAN BLDG NO .03,05, 06 & CLUB HOUSE

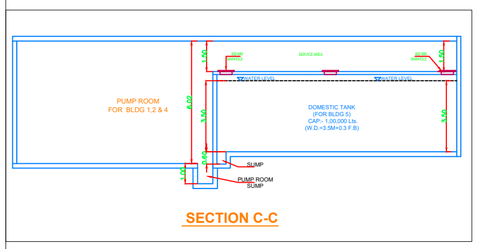

SECTION C-C

ARCHITECT–

VITAN CONSULTANTS
ARCHITECTS & ENGINNERS
5TH FLOOR,MIDTOWN EMBASSY,BEHIND VASANT VALLEY BUS DEPOT,OPP.NARAYNA SCHOOL,VASANT VALLEY GANDHARE KALYAN (W)

PLUMBING CONSULTANT:–

ENGINEERING CREATIONS
PUBLIC HEALTH CONSULTANCY (P) LTD.
Office No. 703, 8th Floor, Ecstacy Business Park
Near Mulund East–West Flyover, Jatashankar Dosa Road,
Mulund (West), Mumbai–400080
Tel. 022 25918279/25918227 TELE–FAX. 25918203
E–mail :engcreat@vsnl.com

PROJECT:–

PROPOSED BUILDING LAYOUT ON PLOT BEARING ON S.NO:67/1/2, 67/1/3,68/6,68/7,68/8 VILLAGE–DAVDI, TALUKA–KALYAN, DIST–THANE FOR

TITLE:–

UNDERGROUND WATER TANK LOCATION LAYOUT

DATE	SCALE	REV. NO.	DRAWN BY	CHKD. BY
09.02.2026	NTS	R.0	GANESH	KAVI

DRG. No.	CAD. No.
REGENCY GROUP DEMART/ECPH/ UNDERGROUND TANK LOCATION LAYOUT	REGENCY GROUP DEMART/ECPH/ UNDERGROUND TANK LOCATION LAYOUT

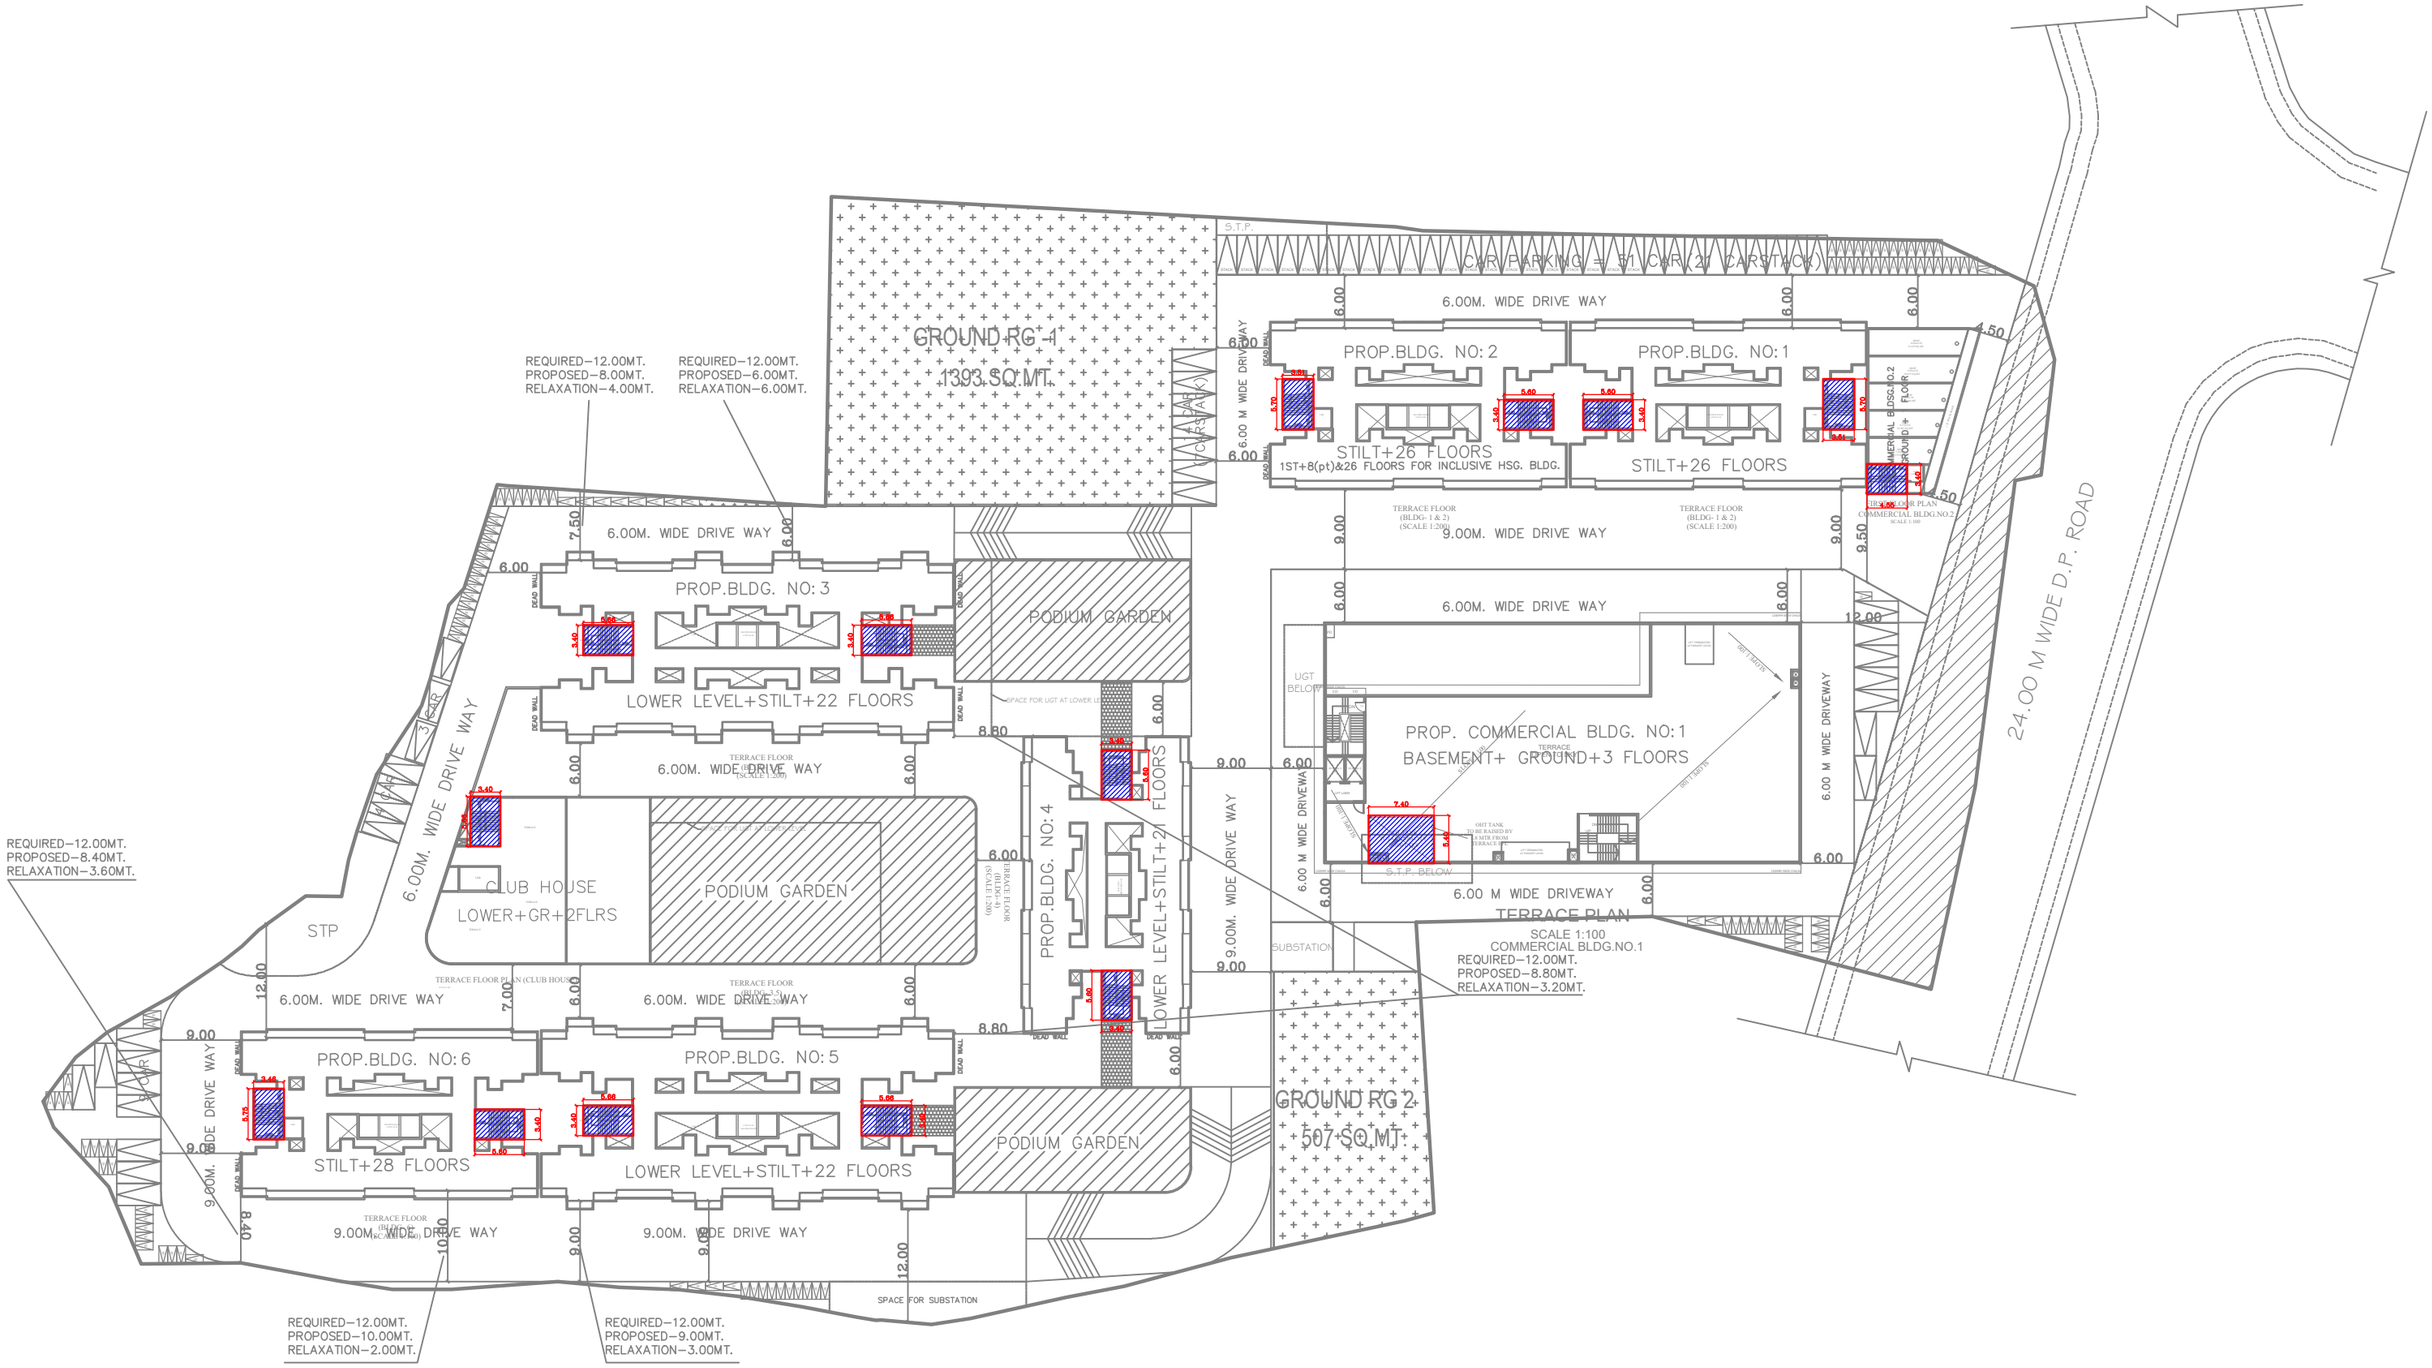

OHT LAYOUT PLAN

OVERHEAD TANK