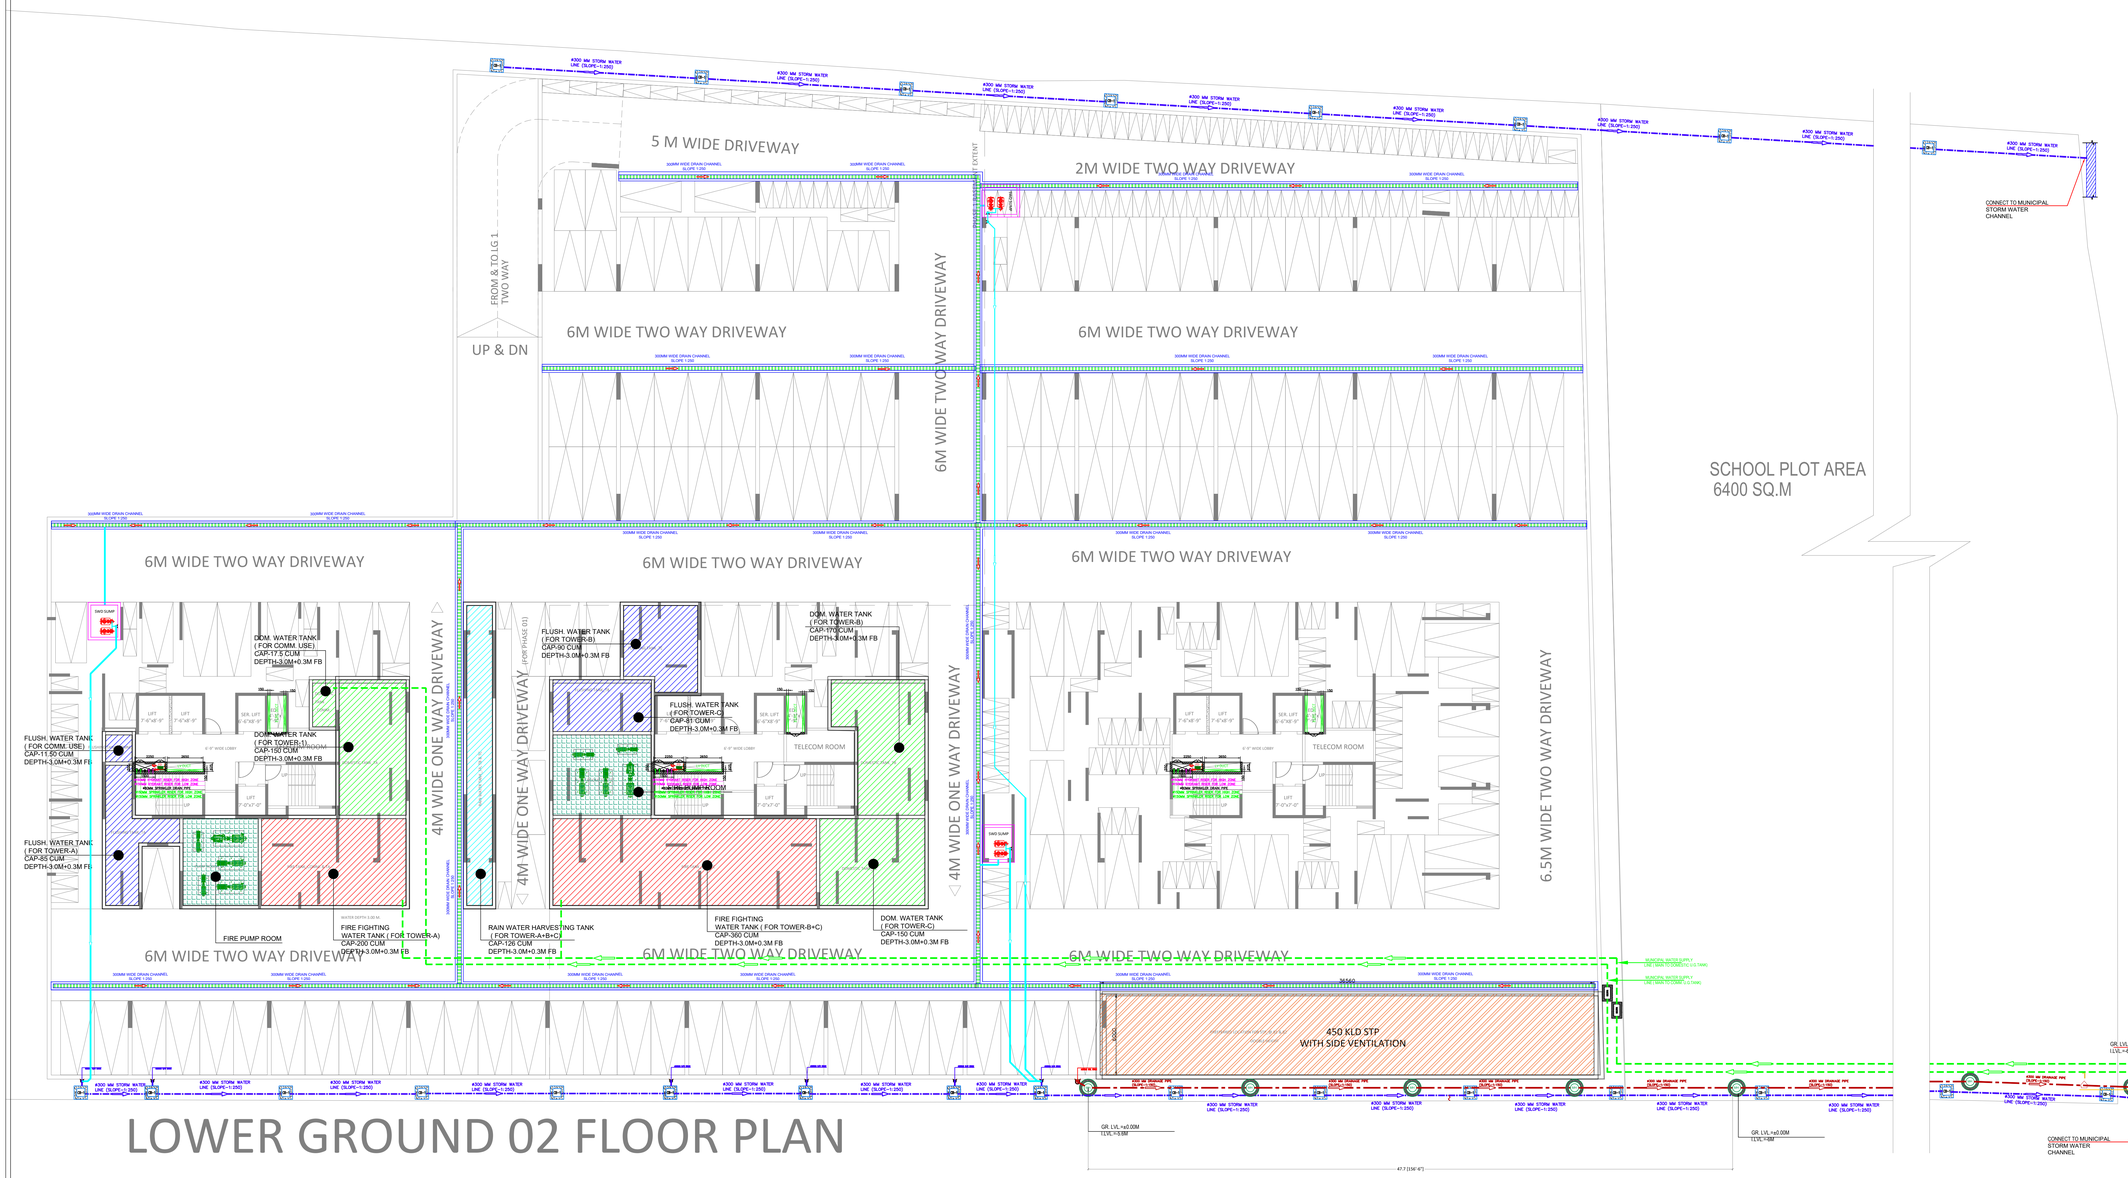

LOWER GROUND 02 FLOOR PLAN

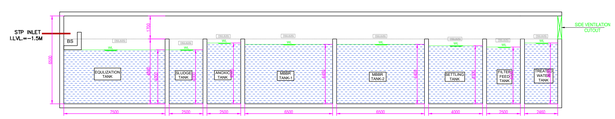

SECTION-AA

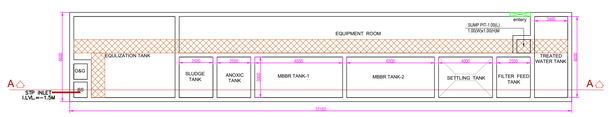

450 KLD STP PLAN

TANK DETAILS

TOTAL AREA :220sqm

Sr. NO	NAME OF TANK	CAPACITY (VOLUME)	WATER DEPTH	TANK AREA	TANK DEPTH	RETENTION TIME
1	EQUALIZATION TANK	180KL	4.0mtr	45sqm	4.8mtr	9hr
2	ANOXIC TANK	33.75KL	4.5mtr	7.5sqm	4.0mtr	2hr
3	MBBR TANK-1	85.8KL	4.4mtr	19.5sqm	4.0mtr	8hr
4	MBBR TANK-2	85.8KL	4.4mtr	19.5sqm	4.0mtr	2hr
5	SETTLING TANK	51.6KL	4.3mtr	12sqm	4.0mtr	2hr
6	FILTER FEED TANK	31.5KL	4.2mtr	7.50sqm	4.0mtr	2hr
7	SLUDGE TANK	30KL	4.0mtr	7.5sqm	4.0mtr	2hr
7	TREATED WATER TANK	66KL	4.5mtr	14.75sqm	4.0mtr	5hr

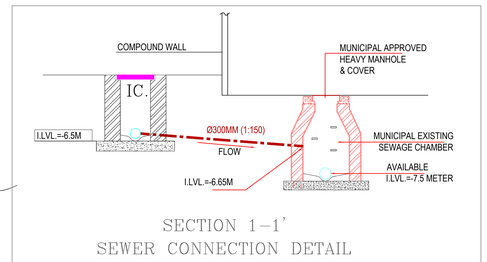

SECTION 1-1'
SEWER CONNECTION DETAIL

COMMENTS :		APPROVAL :	✓				
ADVANCE COPY :		TENDER COPY :					
GFC :		AS BUILT :					
DESIGN DETAIL:		DBR :					

REV.	DESCRIPTION	DATE	DRN BY	CHK BY	APP BY

ARCHITECT: APICES studio pvt. ltd. — APICES Studio Pvt. Ltd

CLIENT: PV VENTURES

PROJECT NAME : PROPOSED RESIDENTIAL DEVELOPMENT AT VILLAGE BHAL ,DOMBIVILI (EAST)

TITLE : PLUMBING LAYOUT FOR LOWER GROUND - 02 FLOOR PLAN

MEP CONSULTANTS
Sourabh Sheth
Mr. Sourabh Ashok Sheth
AQUA CORP CO.
2803,2804 PLAN-S BUSINESS PARK
MIDC INDUSTRIAL AREA, OPP DY PATIL STADIUM
NERUL, NAVI MUMBAI - 400706
Tel. : +91 022-20871359 / Mob : +91 9833.00.6842
Email ID : Sourabh.S@AquaCorp.in / Website : www.AquaCorp.in

DRAWN BY	CHECKED BY	APPROVED BY	DATE
PRASHANT	RAKESH K. M.	SOURABH SIR	11.03.2026

JOB No. AQC-....

DRAWING No. AQC....

REF. DRAWING No.

SIZE : A0 | SCALE : NTS | REV. No. R6

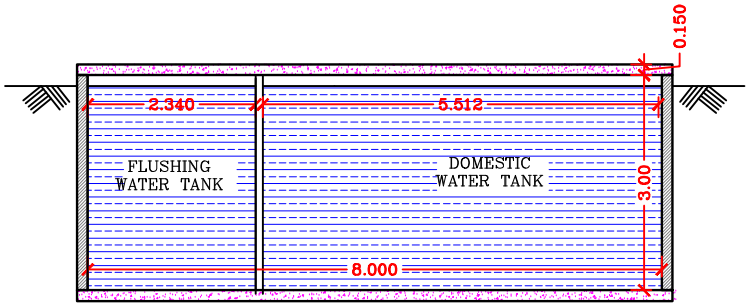

SECTION AA'

SCALE 1:100

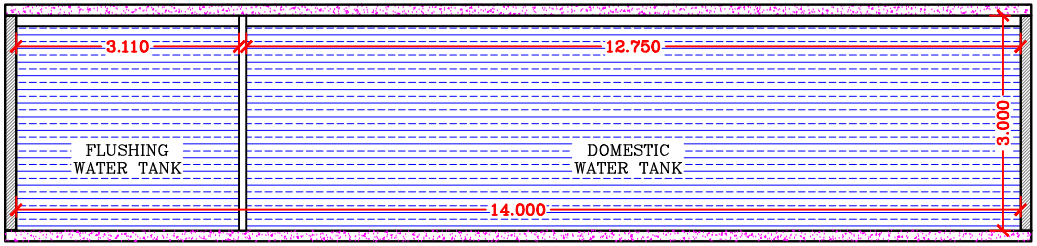

SECTION AA'

SCALE 1:100

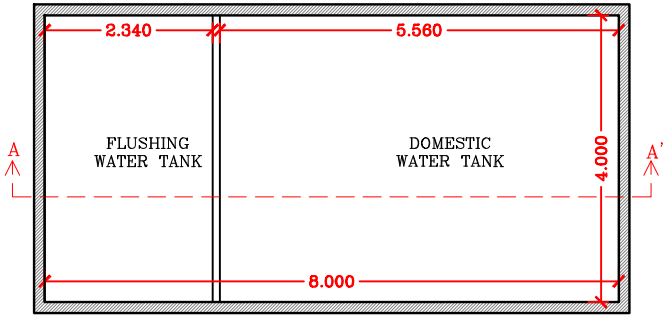

OVER HEAD WATER TANK PLAN

SCALE 1:100

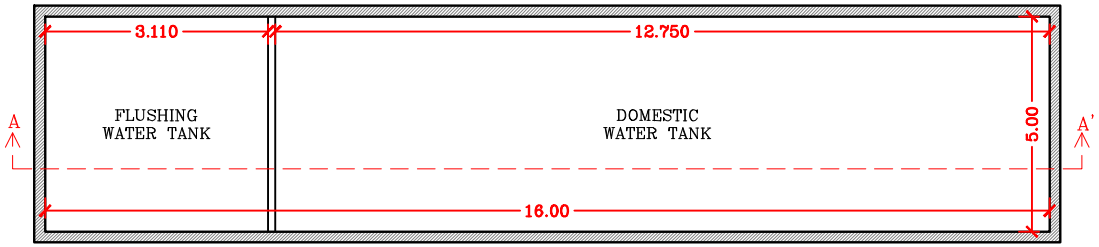

UNDER GROUND WATER TANK PLAN

SCALE 1:100

NAME OF ARCHITECT : TEJAS ANIL NIRGUDE NAME OF CLIENT : PV VENTURES	DATE 16-03-2026	SCALE AS SHOWN	LOGO	DESCRIPTION OF PROJECT : PROPOSED RESIDENTIAL DEVELOPMENT ON PLOT BEARING S.NO. 26,H.NO.2/1 AT VILLAGE BHAL ,DOMBIVILI (EAST)