PRODUCED BY AN AUTODESK EDUCATIONAL PRODUCT

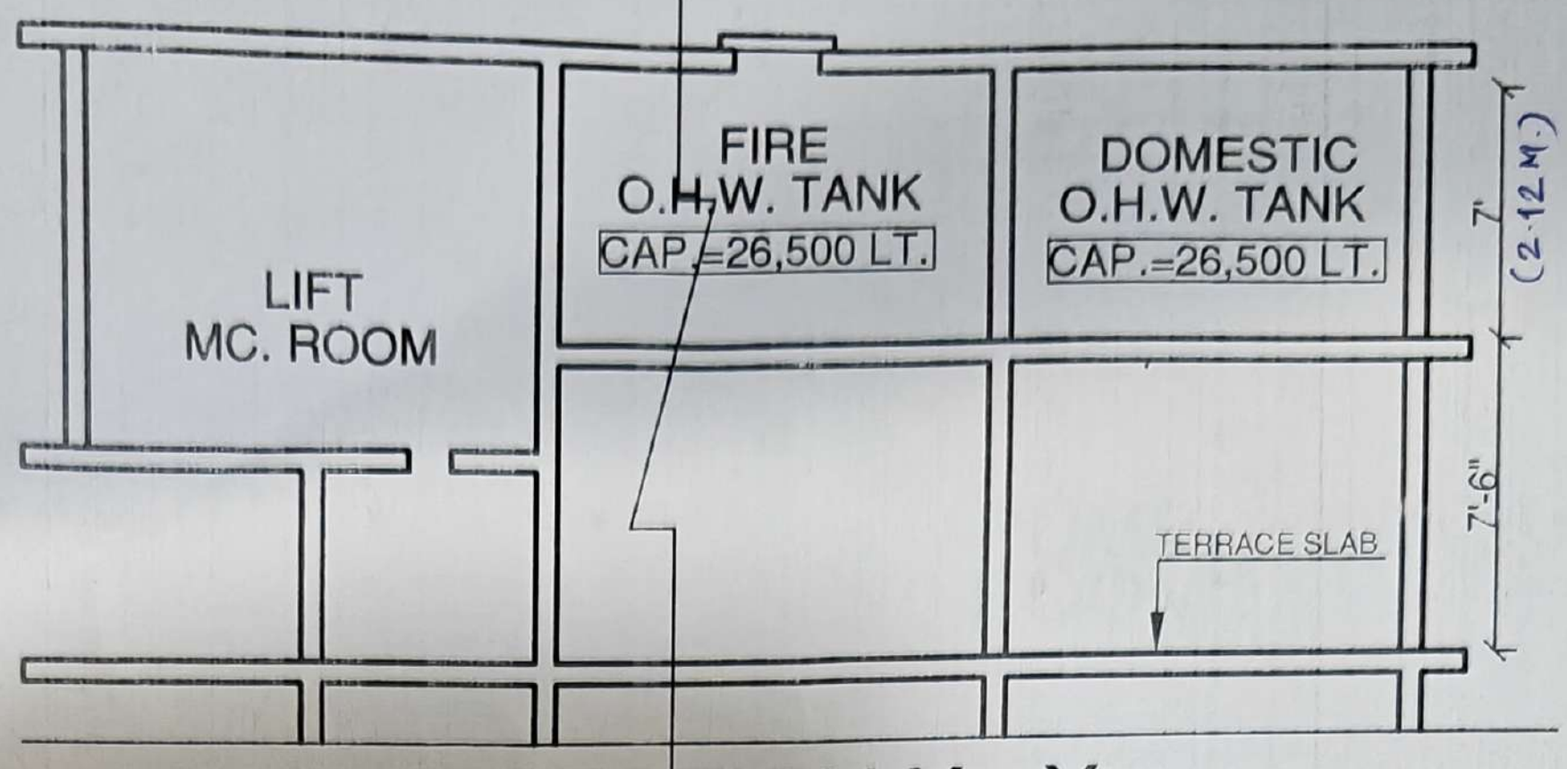

SECTION X - X

SCALE 1 : 100

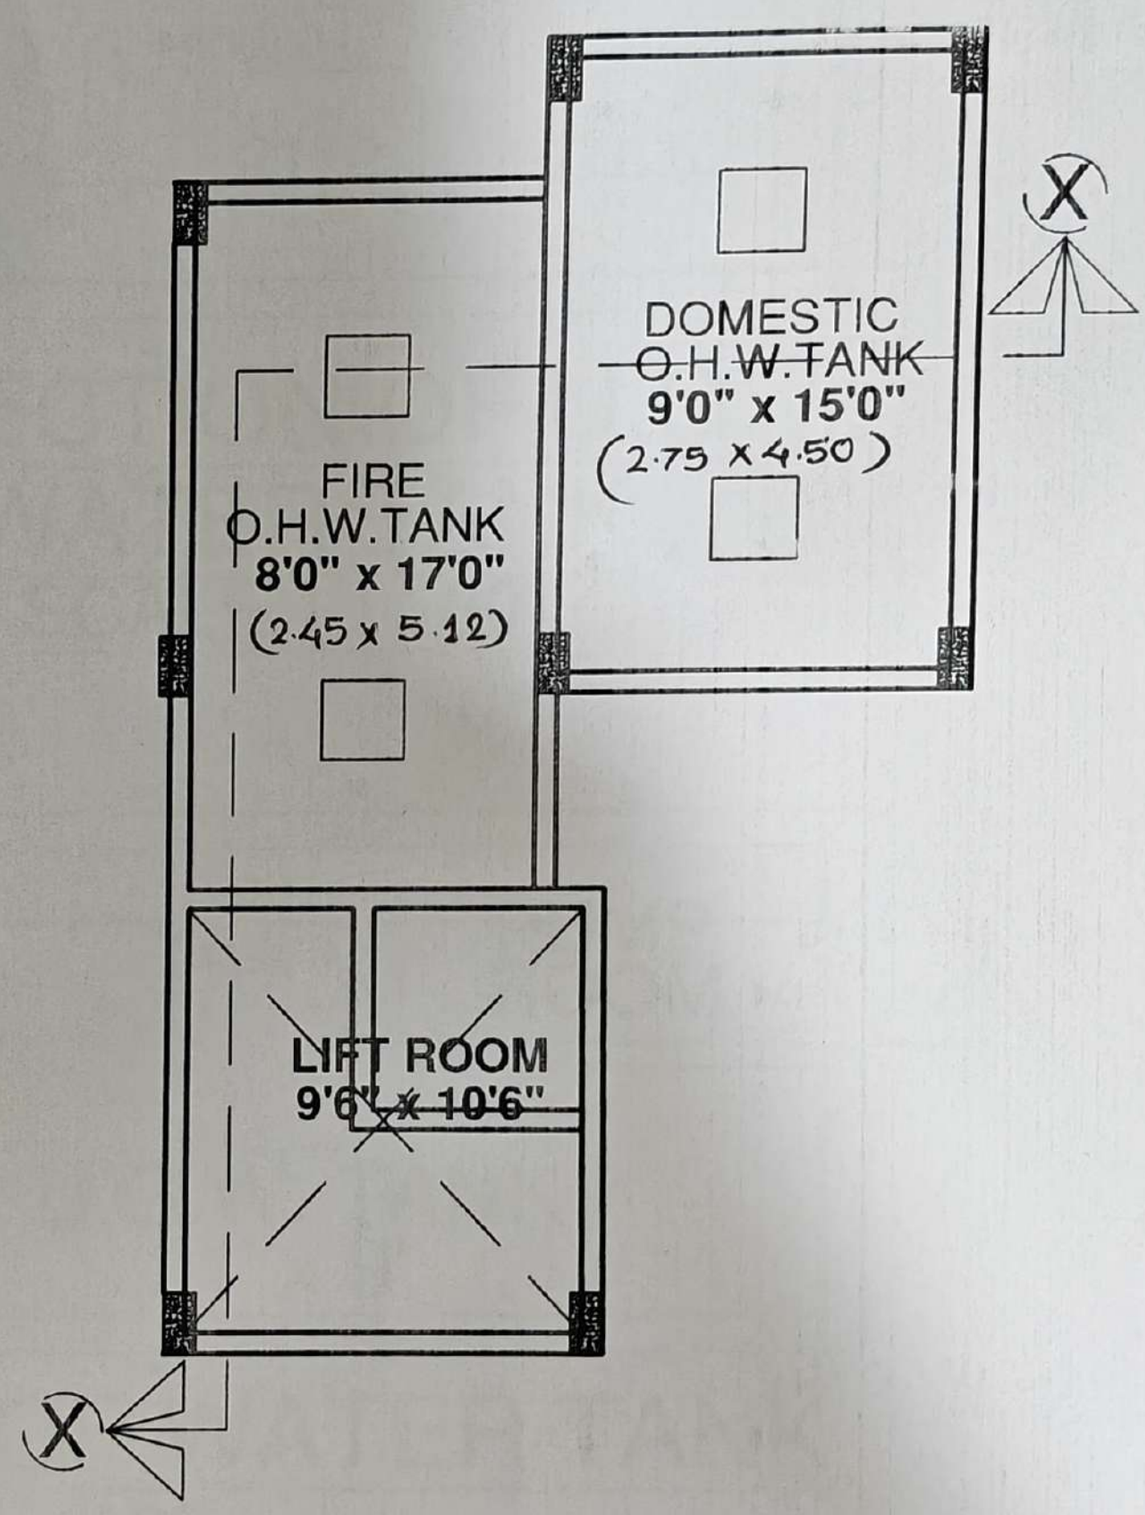

PLAN OF O.H.WATER TANK

SCALE 1 : 100

DESCRIPTION OF PROPERTY & PROPOSAL	ARCHITECT
O.H. WATER TANK DETAILS FOR PROPOSED REDEVELOPMENT BUILDING "SUJAY HEIGHTS" ON PLOT BEARING C.T.S.NO.2955/B/2 AT VILLAGE - KALYAN, TAL.- KALYAN, DIST.- THANE.	Pradeep M Kamble and associates architects, valuers, interior designers B/101, 1st FLOOR, JAKH BAUTERA COMPLEX, PT.MALVIYA PATH, RAMNAGAR, DOMBIVLI(E) 3, BASEMENT, NILKANTH TOWER, OPP. ICICI BANK, RAM MARUTI ROAD, THANE(W).

PRODUCED BY AN AUTODESK EDUCATIONAL PRODUCT
PRODUCED BY AN AUTODESK EDUCATIONAL PRODUCT
PRODUCED BY AN AUTODESK EDUCATIONAL PRODUCT

PRODUCED BY AN AUTODESK EDUCATIONAL PRODUCT

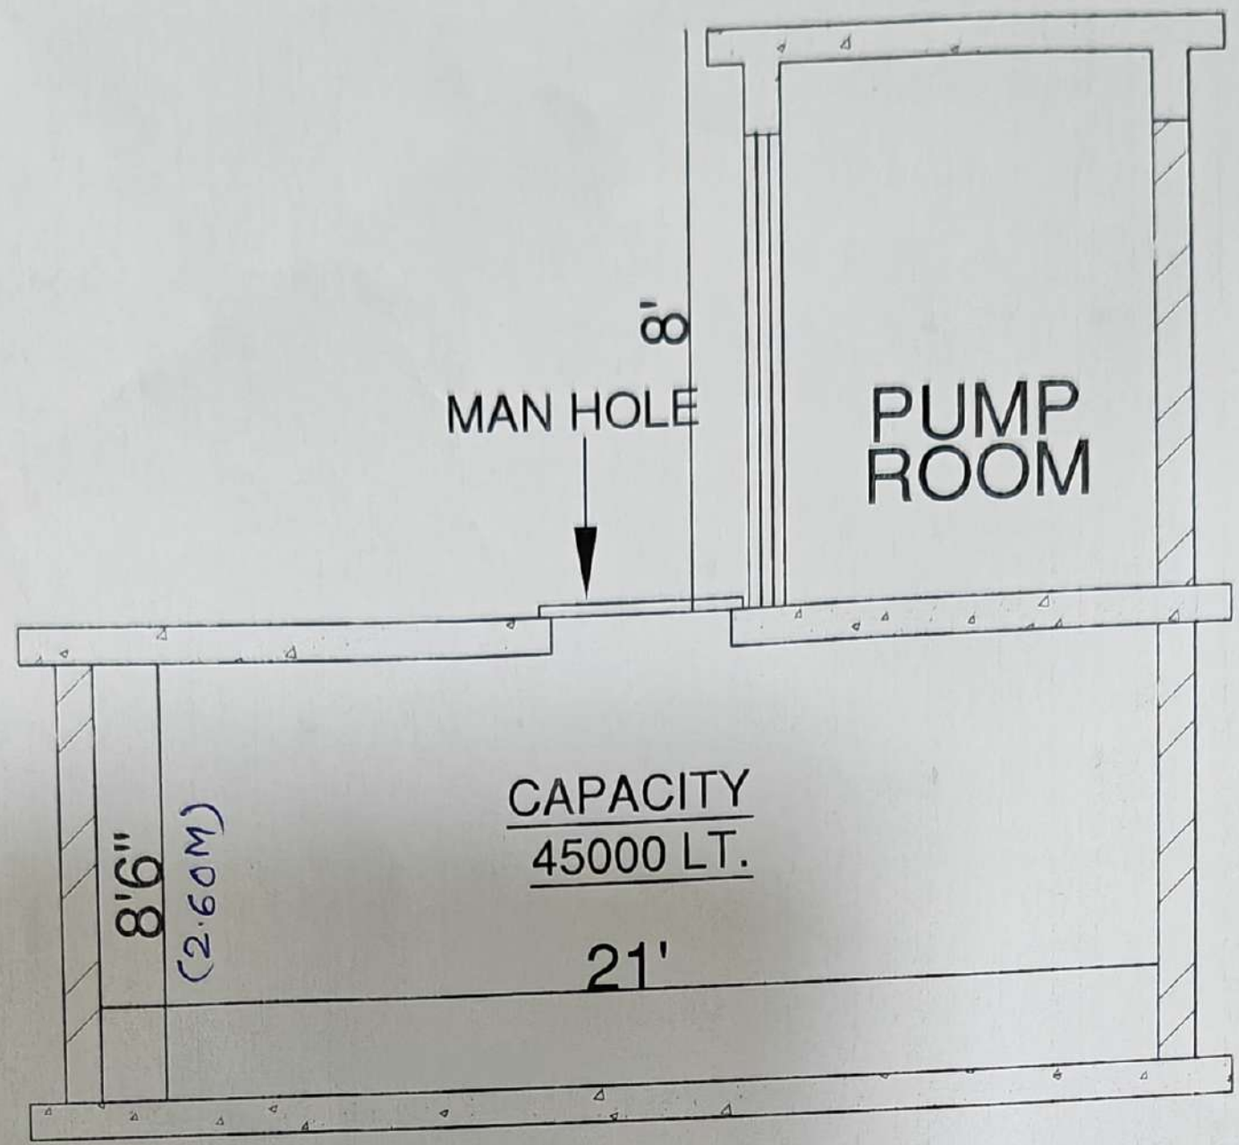

SECTION OF U.G. WATER TANK

SCALE 1 : 100

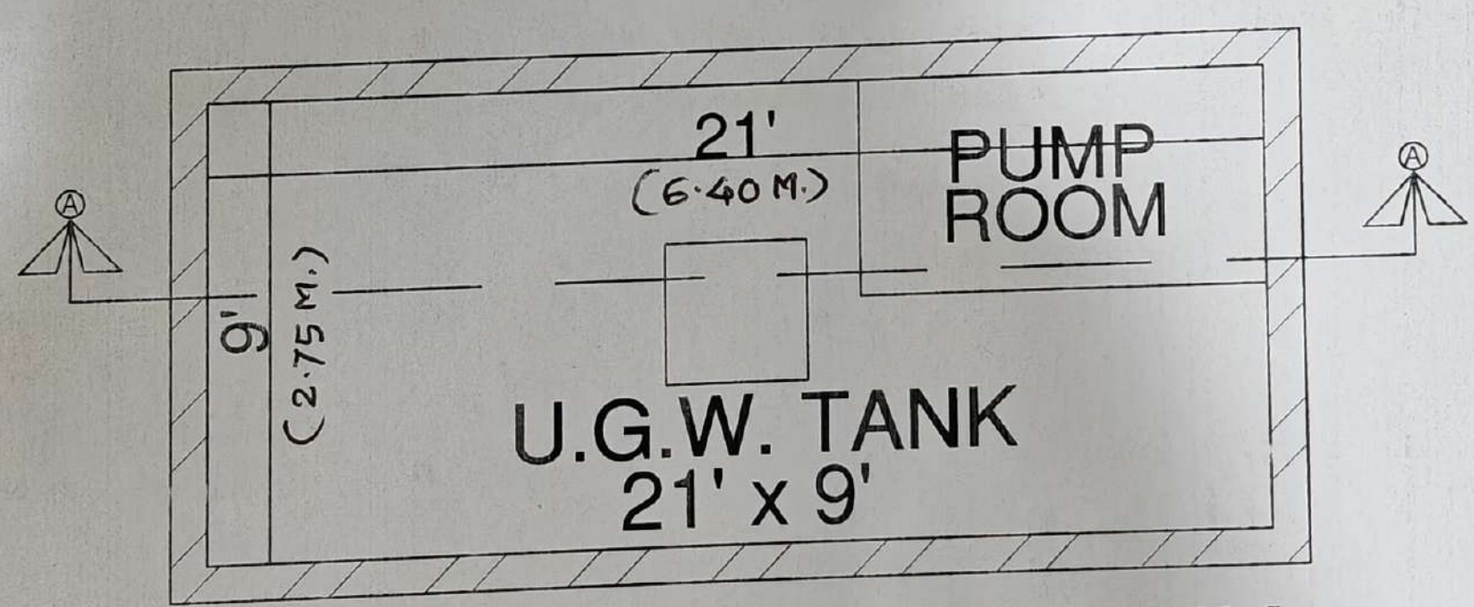

PLAN OF WATER TANK

SCALE 1 : 100

DESCRIPTION OF PROPERTY & PROPOSAL	ARCHITECT
O.H. WATER TANK DETAILS FOR PROPOSED REDEVELOPMENT BUILDING "SUJAY HEIGHTS" ON PLOT BEARING C.T.S.NO.2955/B/2 AT VILLAGE - KALYAN, TAL.- KALYAN, DIST.- THANE.	Pradeep M Kamble and associates architects, valuers, interior designers B/101, 1st FLOOR, JAKH BAUTERA COMPLEX, PT.MALVIYA PATH, RAMNAGAR, DOMBIVLI(E) 3, BASEMENT, NILKANTH TOWER, OPP. ICICI BANK, RAM MARUTI ROAD, THANE(W).

PRODUCED BY AN AUTODESK EDUCATIONAL PRODUCT
PRODUCED BY AN AUTODESK EDUCATIONAL PRODUCT
PRODUCED BY AN AUTODESK EDUCATIONAL PRODUCT