VITAN CONSULTANTS

ARCHITECTS & INTERIOR DESIGNERS

5TH FLOOR, MIDTOWN EMBASSY, BEHIND VASANT VALLEY BUS DEPOT,
OPP. NARAYANA SCHOOL, VASANT VALLEY, GANDHARE KALYAN (W).

TEJAS ANIL NIRGUDE
B. ARCH & INTERIOR DESIGNER

E-mail : vitanconsultants@yahoo.com
M.:8451985999

संदर्भ क्र.९८४
दि.२७/०१/२०२६

प्रति,
मा.कार्यकारी अभियंता
पाणी पुरवठा विभाग
क.डो.म.पा
कल्याण.

विषय :- सि.स.नं.३३६०,३३६१,३३६३ मौजे: कल्याण,ता.कल्याण ,अंबर को.ऑ.हौ.सो.व जी.एच कोलते व इतर,कुमुपधा. मे .मिडास क्रियटर तर्फे श्री. प्रणव प्रकाश पेणकर या भुखंडावर बांधण्यात येणाऱ्या इमारतीच्या बांधकाम परवानगीच्या दाखल्यासाठी जलनि:सारण विभागचा नाहरकत दाखला मिळणे बाबत.

१) भूखंडाचे विवरण- सि.स.नं.३३६०,३३६१,३३६३ मौजे: कल्याण,
२) विकसीत करावयाचे क्षेत्र – ३८८६.५५चौ.मी.प्रस्तावित सदनिका इमारत - अ ८२,इमारत - बी.८५ व गाळे इमारत –अ ५ इमारत – बी ८ ऑफीस इमारत – अ ८ इमारत - बी १०

		इमारत अ	इमारत ब
३	महापालिकेकडून आवश्यक पाणी पुरवठा	९६०००.००ली.	९६०००.००ली.
४	पाण्याच्या टाकीची लांबी	६ मी.	६ मी.
५	पाण्याच्या टाकीची रुंदी	३ मी.	३ मी.
६	पाण्याच्या टाकीची उंची	४ मी.	४ मी.
७	इमारती वरील पाण्याच्या टाकीची लांबी	८ मी.	६ मी.
८	इमारती वरील पाण्याच्या टाकीची रुंदी	४ मी.	४ मी.
९	इमारती वरील पाण्याच्या टाकीची उंची	३ मी.	४ मी.
१०	पाणी पुरवठा लाईन पासुन चे अंतर	२३ मी.	७ मी.

वितान कन्सल्टंट करिता

वास्तुशिल्पकार

				TYPE A											
BUILDING	FLOORS	COMM	RESI.	FSI AREA	EDU	INS.	MUZZ.	BALCONY	TERRACE	LIFT	LIFTWELL	DUCT	VENT SHAFT	OTHER DEDUCTION	TOTAL FSI AREA
TYPE A	TERRACE FLOOR	0.000	12.300	0.000	0.000	0.000	0.000	0.000	0.000	0.000	0.000	0.000	0.000	0.000	12.300
TYPE A	7TH 12TH 17TH	0.000	1137.165	0.000	0.000	0.000	0.000	16.510	0.000	0.000	26.400	0.000	0.000	174.969	925.196
TYPE A	6TH TO 11TH 16TH TO 18TH 5TH 13TH 15TH 2ND 8TH FLOOR	0.000	3382.695	0.000	0.000	0.000	0.000	27.450	0.000	0.000	79.200	0.000	0.000	129.222	3174.273
TYPE A	4TH TO 6TH 8TH FLOOR	0.000	1525.612	0.000	0.000	0.000	0.000	36.600	0.000	0.000	39.200	0.000	0.000	57.432	1427.580
TYPE A	3RD FLOOR	0.000	473.600	0.000	0.000	0.000	0.000	9.150	0.000	0.000	13.600	0.000	0.000	18.208	432.642
TYPE A	2ND FLOOR	40.500	0.000	0.000	0.000	0.000	0.000	23.000	0.000	0.000	44.000	0.000	0.000	10.500	208.997
TYPE A	1ST FLOOR	430.501	0.000	0.000	0.000	0.000	0.000	0.000	0.000	0.000	14.200	0.000	0.000	10.579	405.481
TYPE A	GROUND FLOOR	142.893	195.375	0.000	0.000	0.000	0.000	0.000	0.000	14.200	0.000	0.000	0.000	2.451	295.525
TYPE A	TOTAL	1022.468	6575.500	0.000	0.000	0.000	0.000	117.659	0.000	14.200	176.120	0.000	0.000	399.942	7029.906

				TYPE B											
BUILDING	FLOORS	COMM	RESI.	FSI AREA	EDU	INS.	MUZZ.	BALCONY PROP	TERRACE	LIFT	LIFTWELL	DUCT	VENT SHAFT	OTHER DEDUCTION	TOTAL FSI AREA
TYPE B	7TH 12TH 17TH FLOOR	0.000	1548.540	0.000	0.000	0.000	0.000	40.075	0.000	0.000	38.400	86.091	0.000	220.324	1202.730
TYPE B	6TH 8TH 10 11TH 16TH TO 18TH 5TH 13TH 15TH 2ND 9TH FLOOR	0.000	6198.180	0.000	0.000	0.000	0.000	221.150	0.000	0.000	153.600	344.364	0.000	95.676	5664.540
TYPE B	5TH FLOOR	0.000	523.269	0.000	0.000	0.000	0.000	24.665	0.000	0.000	12.800	28.697	0.000	7.973	473.795
TYPE B	4TH FLOOR	0.000	528.540	0.000	0.000	0.000	0.000	24.663	0.000	0.000	12.800	28.697	0.000	7.973	477.170
TYPE B	3RD FLOOR	0.000	528.540	0.000	0.000	0.000	0.000	24.663	0.000	0.000	12.800	28.697	0.000	7.973	477.170
TYPE B	2ND FLOOR	396.132	0.000	0.000	0.000	0.000	0.000	35.825	0.000	0.000	14.200	0.000	0.000	18.750	358.782
TYPE B	1ST FLOOR	539.400	0.000	0.000	0.000	0.000	0.000	6.650	0.000	0.000	18.200	0.000	0.000	18.750	522.440
TYPE B	GROUND FLOOR	251.423	190.263	0.000	0.000	0.000	0.000	0.000	0.000	18.200	0.000	0.000	0.000	8.610	425.036
TYPE B	TOTAL	1627.955	9494.428	0.000	0.000	0.000	0.000	360.441	0.000	18.200	258.520	516.546	0.000	385.929	9732.579

FSI CALCULATION

Sl.	Index	Basic FSI (on serial no 7)	Premium FSI (on serial no 3)	TDR/DR on serial no 3)	Permissible for full green building if Applicable (on serial no 7 A)	Ancillary Area(65% of 2 + 3+4+5)	Ancillary Area(65% of 2 + 3+4+5)	Total	Drawing Value
10.1 Permissible Index		1.100	0.000	1.900	50%	0.000	0.000	3.000	0.000
10.2 Total Entitlement of FSI as per 7.A, 7.B, 7.C, 7.D		1.100	0.000	1.900	0.500	0.000	0.000	3.000	0.000
10.3 FSI Permissible in Redevelopment(Sec 40 10.1 and 10.2) Minus Consumed Index		1.100	0.000	1.900	0.500	0.000	0.000	3.000	0.000
10.4 Balance Index Available for Development (10.3) - 10.4)		0.000	0.000	0.000	0.000	0.000	0.000	0.000	-
10.5 Total Permissible FSI Area (Area x Index)		1.100	0.000	1.900	0.500	0.000	0.000	3.000	-
10.6 Total Consumed FSI Area		3495.800	0.000	6038.200	0.001	0.000	5451.296	15029.365	16014.658	0.000
10.7 Proposed FSI (Line Area x Index) Not exceed 10.4)		3495.800	0.000	5523.000	0.001	0.000	5451.296	15029.296	15899.365	16058.256
10.8 Balance Consumed		1.100	0.577	1.296	0.500	0.000	0.000	2.964	0.000

Carpet Area Table

Building Name	Floor Name	Carpet name	Tenament No	Carpet Area	Enclosed Balcony Area(as per 65%)	Normal Balcony Area(as per 40%)	Wesspace Area	Total Carpet Area
TYPE A	GROUND FLOOR	1	1	14.261	0.000	0.000	0.000	14.261
TYPE A	GROUND FLOOR	2	1	19.088	0.000	0.000	0.000	19.088
TYPE A	GROUND FLOOR	3	1	20.134	0.000	0.000	0.000	20.134
TYPE A	GROUND FLOOR	4	1	25.080	0.000	0.000	0.000	25.080
TYPE A	GROUND FLOOR	5	1	18.057	0.000	0.000	0.000	18.057
TYPE A	1ST FLOOR	1	1	81.573	0.000	0.000	0.000	81.573
TYPE A	1ST FLOOR	2	1	62.880	0.000	0.000	0.000	62.880
TYPE A	1ST FLOOR	3	1	52.863	0.000	0.000	0.000	52.863
TYPE A	1ST FLOOR	4	1	64.538	0.000	0.000	0.000	64.538
TYPE A	2ND FLOOR	1	1	82.530	3.000	0.000	0.000	85.530
TYPE A	2ND FLOOR	2	1	63.960	4.500	0.000	0.000	70.560
TYPE A	2ND FLOOR	3	1	73.535	12.762	0.000	0.000	86.297
TYPE A	2ND FLOOR	4	1	65.530	2.887	0.000	0.000	68.417
TYPE A	3RD FLOOR	1	1	46.530	4.170	0.000	0.000	50.700
TYPE A	3RD FLOOR	2	1	46.530	4.170	0.000	0.000	50.700
TYPE A	3RD FLOOR	3	1	51.370	0.000	0.000	0.000	51.370
TYPE A	3RD FLOOR	4	1	56.548	0.000	0.000	0.000	56.548
TYPE A	3RD FLOOR	5	1	47.942	3.000	0.000	0.000	50.992
TYPE A	4TH TO 6TH 8TH	1	4	41.903	0.000	0.000	0.000	41.903
TYPE A	4TH TO 6TH 8TH FLOOR	2	4	48.530	6.170	0.000	0.000	54.700
TYPE A	4TH TO 6TH 8TH FLOOR	3	4	51.370	0.000	0.000	0.000	51.370
TYPE A	4TH TO 6TH 8TH FLOOR	4	4	56.548	0.000	0.000	0.000	56.548
TYPE A	4TH TO 6TH 8TH FLOOR	5	4	47.942	3.000	0.000	0.000	50.992
TYPE A	9TH TO 11TH 16TH TO 18TH FLOOR	1	9	37.200	0.000	0.000	0.000	37.200
TYPE A	9TH TO 11TH 16TH TO 18TH FLOOR	2	9	48.530	0.000	0.000	0.000	48.530
TYPE A	9TH TO 11TH 16TH TO 18TH FLOOR	3	9	51.370	0.000	0.000	0.000	51.370
TYPE A	9TH TO 11TH 16TH TO 18TH FLOOR	4	9	56.548	0.000	0.000	0.000	56.548
TYPE A	9TH TO 11TH 16TH TO 18TH FLOOR	5	9	47.942	3.000	0.000	0.000	50.992
TYPE A	7TH 12TH 17TH	1	3	37.200	0.000	0.000	0.000	37.200
TYPE A	7TH 12TH 17TH	2	3	48.530	6.170	0.000	0.000	54.700
TYPE A	7TH 12TH 17TH	3	3	51.370	0.000	0.000	0.000	51.370
TYPE A	7TH 12TH 17TH	4	3	67.079	0.000	0.000	0.000	67.079

Building Name	Floor Name	Carpet name	Tenament No	Carpet Area	Enclosed Balcony Area(as per 65%)	Normal Balcony Area(as per 40%)	Wesspace Area	Total Carpet Area
TYPE B	GROUND FLOOR	1	1	59.933	0.000	0.000	0.000	59.933
TYPE B	GROUND FLOOR	2	1	22.775	0.000	0.000	0.000	22.775
TYPE B	GROUND FLOOR	3	1	9.408	0.000	0.000	0.000	9.408
TYPE B	GROUND FLOOR	4	1	17.825	0.000	0.000	0.000	17.825
TYPE B	GROUND FLOOR	5	1	19.673	0.000	0.000	0.000	19.673
TYPE B	GROUND FLOOR	6	1	22.000	0.000	0.000	0.000	22.000
TYPE B	GROUND FLOOR	7	1	22.000	0.000	0.000	0.000	22.000
TYPE B	GROUND FLOOR	8	1	23.945	0.000	0.000	0.000	23.945
TYPE B	1ST FLOOR	1	1	67.453	0.000	0.000	0.000	67.453
TYPE B	1ST FLOOR	2	1	48.638	0.000	0.000	0.000	48.638
TYPE B	1ST FLOOR	3	1	71.505	0.000	0.000	0.000	71.505
TYPE B	1ST FLOOR	4	1	64.757	0.000	0.000	0.000	64.757
TYPE B	1ST FLOOR	5	1	102.457	6.650	0.000	0.000	109.107
TYPE B	2ND FLOOR	1	1	68.545	7.250	0.000	0.000	75.795
TYPE B	2ND FLOOR	2	1	46.740	7.350	0.000	0.000	57.090
TYPE B	2ND FLOOR	3	1	71.505	7.350	0.000	0.000	78.855
TYPE B	2ND FLOOR	4	1	69.532	11.625	0.000	0.000	81.157
TYPE B	2ND FLOOR	5	1	102.940	10.200	0.000	0.000	113.190
TYPE B	3RD FLOOR	1	1	86.500	0.000	4.225	0.000	90.725
TYPE B	3RD FLOOR	2	1	58.128	3.400	0.000	0.000	62.528
TYPE B	3RD FLOOR	3	1	69.330	3.400	0.000	0.000	72.730
TYPE B	4TH FLOOR	1	1	62.018	4.000	0.000	0.000	66.018
TYPE B	4TH FLOOR	2	1	58.127	3.400	0.000	0.000	62.527
TYPE B	4TH FLOOR	3	1	58.128	3.400	0.000	0.000	62.528
TYPE B	4TH FLOOR	4	1	71.905	3.400	0.100	0.000	75.405
TYPE B	5TH FLOOR	1	1	62.018	4.000	0.000	0.000	66.018
TYPE B	5TH FLOOR	2	1	58.127	3.400	0.000	0.000	62.527
TYPE B	5TH FLOOR	3	1	86.500	0.000	4.225	0.000	86.500
TYPE B	5TH FLOOR	4	1	58.128	3.400	0.000	0.000	62.528
TYPE B	5TH FLOOR	5	1	69.790	3.400	6.400	0.000	73.190
TYPE B	6TH 8TH 10TH 11TH 16TH TO 18TH AND 18TH TO 20TH FLOOR	1	12	62.018	4.000	0.000	0.000	66.018
TYPE B	6TH 8TH 10 11TH 16TH TO 18TH AND 18TH TO 20TH FLOOR	3	12	86.500	0.000	4.225	0.000	86.500
TYPE B	6TH 8TH 10 11TH 16TH TO 18TH AND 18TH TO 20TH FLOOR	4	12	58.128	3.400	0.000	0.000	62.528
TYPE B	6TH 8TH 10 11TH 16TH TO 18TH AND 18TH TO 20TH FLOOR	5	12	69.330	3.400	0.000	0.000	72.730
TYPE B	7TH 12TH 17TH FLOOR	1	3	62.018	4.000	0.000	0.000	66.018
TYPE B	7TH 12TH 17TH FLOOR	2	3	86.500	0.000	4.225	0.000	86.500
TYPE B	7TH 12TH 17TH FLOOR	3	3	58.128	3.400	0.000	0.000	62.528
TYPE B	7TH 12TH 17TH FLOOR	4	3	69.330	3.400	0.000	0.000	72.730
TYPE B	9TH 11TH 16TH 18TH TO 20TH 19TH FLOOR	1	12	62.018	4.000	0.000	0.000	66.018
TYPE B	9TH 11TH 16TH 18TH TO 20TH 19TH FLOOR	2	12	59.128	3.400	0.000	0.000	62.528
TYPE B	9TH 11TH 16TH 18TH TO 20TH 19TH FLOOR	3	12	69.330	3.400	0.000	0.000	72.730
TYPE B	9TH 11TH 16TH 18TH TO 20TH 19TH FLOOR	4	12	59.128	3.400	0.000	0.000	62.528
TYPE B	9TH 11TH 16TH 18TH TO 20TH 19TH FLOOR	5	12	69.790	3.400	6.400	0.000	73.190

Area Utilisation of Roads and Reservations

Description of area utilisation						
Sq.(Unit)	Reservation type	Reservation no	Authorised Area (Sq.Mtr)	Quantum of DR/TDR generation	Total Quantum of DR/TDR generation	Area considered for DR utilisation	Remaining area for DRC generation
	-		30.000 m DP Road Widening	12.000	24.000	24.000	0.000	0.000
	-		9.00m DP Road Widening	480.000	960.000	960.000	0.000	0.000
			Total	492.000	984.000	984.000	0.000	984.000

Parking Check (Table 6B)

Building Name	USE	TENAMENT AREA	Required FAR/TQ car	Required FAR/TQ scooter	Required NO.OF Tots/Area/Units car	Required NO.OF Tots/Area/Units scooter	Required Transport Tots/Area/Units Mini Bus
TYPE A	Residential	For every two tenament with each tenament having carpet area equal to or above 40 sq.m but less than 80 sq.m.	1	2	66	33.000	66.000	-
TYPE A	Residential	For every two tenament with each tenament having carpet area equal to or above 80 sq.m but less than 40 sq.m.	1	2	13	6.500	13.000	-
TYPE A	Commercial	For every 100 sq.m. of carpet area or fraction thereof	2	6	96.621	1.932	5.797	-
TYPE A	Commercial	For every 200 sq.m. of carpet area or fraction thereof	3	11	552.471	8.287	30.386	1.000
TYPE B	Residential	For every two tenament with each tenament having carpet area equal to or above 80 sq.m but less than 50 sq.m	1	2	64	32.000	64.000	-
TYPE B	Residential	For every tenament having carpet area equal to or above 80 sq.m but less than 160 sq.m	1	1	18	18.000	18.000	-
TYPE B	Commercial	For every 100 sq.m. of carpet area or fraction thereof	2	6	192.792	3.856	11.568	-
TYPE B	Commercial	For every 200 sq.m. of carpet area or fraction thereof	3	11	759.633	11.394	41.790	1.000
Total	-	-	-	-	-	114.970	250.539	2.000
Visitors parking(5%)	-	-	-	-	-	4.475	8.000	-
Total	-	-	-	-	-	119.445	258.580	2.000

Parking Check As Per Multiplying Factor 0.850 (note: TS 8 archtn equals to 1 car, proposed compactly parking for car= 40)

Building Name	Required Car	Required Scooter	Required Transport Vehicle(Auto/Taxi) Mini bus	Provided Car	Provided Scooter	Provided Transport Vehicle(Auto/Taxi) Mini bus	Status
Total	136	0	2	150	31	0	OK

Setback Details

Building	Req. Size	Prop. Size	Status
TYPE A	3.000X3.400	3.000X3.400	OK
TYPE A	3.000X3.400	3.000X3.400	OK
TYPE B	3.000X3.400	3.000X3.400	OK
TYPE B	3.000X3.400	3.000X3.500	OK

SCHEDULE OF OPENING

Sl.n	NAME	HEIGHT	Nos.
TYPE B	V	0.600	0.750	38
TYPE A	V	0.600	0.750	47

Existing Building Tenament Details

Sl.No.	Building/Tenament No	Carpet Area Per Tenament	Mrkt Per Tenament	Name Of Occupant	Number Of Tenements	Residential Non Residential	For Tenament Less than 25 Sq.Mtr 5%Mr Mrkt 25 sf Sqm to be added	Total	Incentive 30%/50% per Tenament for owner	Total incentive	10 Sqm BUA addition per tenament	Total of 10 sqmt Addition	Total
1	1	30.000	35.000	Tenant	70	Residential	0.000	0.000	17.500	0.000	15.000	1050.000	3500.000

Owner details

Owner Name	Owner Address	Contact Number
MIDAS CREATORS	302-Morya Apartment,Titak Chowk,Kalyan,Thane,Maharashtra-421	9664304464
PRANAV PRAKASH PENKAR	1st floor, Shared Complex, Oak Bagh , near kalyan station west, 421301	9664304464

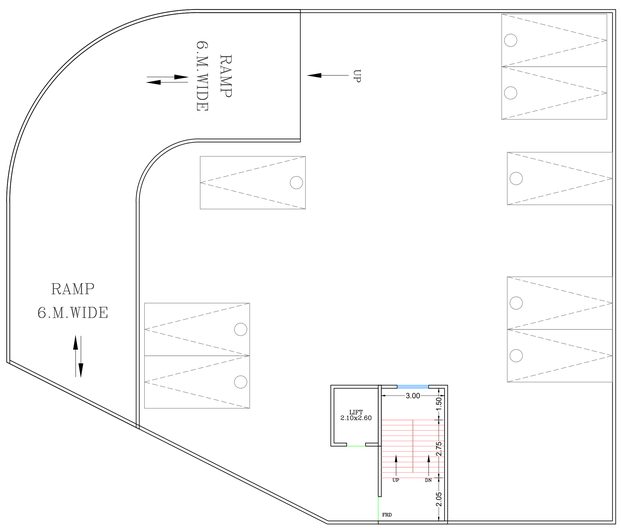

TYPE-A BASEMENT FLOOR PLAN

SCALE 1:100

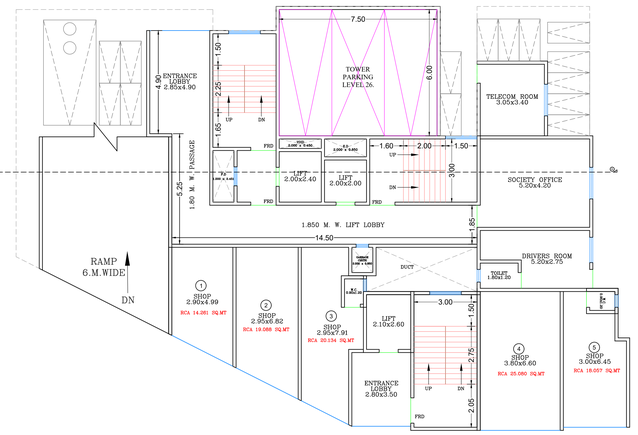

TYPE-A GROUND FLOOR PLAN

SCALE 1:100

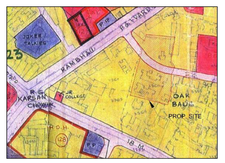

LOCATION PLAN

Project Details
Proposed scheme: KDMCC-26-01792
Zone Type: Residential Zone
Location: Non-Congested
Name of scheme: Redevelopment For Dangerous Building
Sub Scheme: Redevelopment of tenanted buildings
Old No./Survey No.: 3360
Tahsil: section-1
Village: kalyan(PS)
Finalize Value: 0.000
Separation/CRZ Zone Area: -

LEGENDS:
ALL DIMENSIONS IN MILLIMETERS UNLESS OTHERWISE SPECIFIED
PROPOSED WORK SHOWN IN RED
EXISTING WORK SHOWN IN LIGHT WATER LINE SHOWN IN BLUE SCITTED
TOILET BLOCK SHOWN IN YELLOW
TERRACE SHOWN DARK YELLOW
OPEN SAL SHOWN BROWN
EXISTING SHOWN BLUE HATCHED

LAYOUT PLAN | SHEET NO. 1/4

BUILT UP AREA CALCULATION FOR SECTION-1 BLOCK A			
AREA NAME	LENGTH	WIDTH	AHA(SQ.M)
BLOCK	21.200	12.200	158.335
		BLOCK AREA TOTAL =158.335SQ.M	
void20	-	-	2.451
void23	-	-	5.950
void22	-	-	7.250
void21	-	-	7.250
void24	-	-	7.250
void25	-	-	7.250
void26	-	-	7.250
void27	-	-	7.250
void28	-	-	7.250
void29	-	-	7.250
void30	-	-	2.451
		TOTAL Deduction =70.563Sq.M	
		Net Builtup Area =158.335 Sq.M	

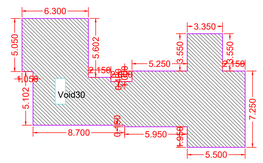

BUILT-UP AREA CALCULATION
GROUND FLOOR TYPE-A

SCALE 1:200

BUILT UP AREA CALCULATION FOR SECTION-1 BLOCK B			
AREA NAME	LENGTH	WIDTH	AHA(SQ.M)
BLOCK	21.200	12.200	158.335
		BLOCK AREA TOTAL =158.335SQ.M	
void29	-	-	2.451
void30	-	-	5.950
void31	-	-	7.250
void32	-	-	7.250
void33	-	-	7.250
void34	-	-	7.250
void35	-	-	7.250
void36	-	-	7.250
void37	-	-	7.250
void38	-	-	2.451
		TOTAL Deduction =70.563Sq.M	
		Net Builtup Area =158.335 Sq.M	

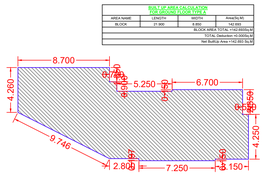

BUILT-UP AREA CALCULATION
GROUND FLOOR TYPE-A

SCALE 1:200

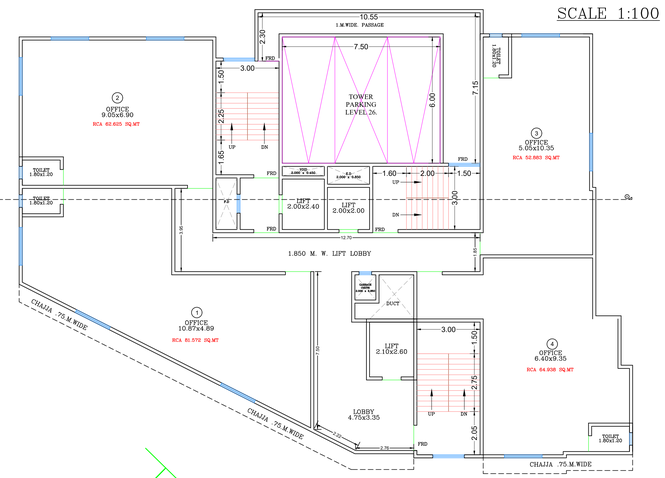

TYPE-A 1ST FLOOR PLAN

SCALE 1:100

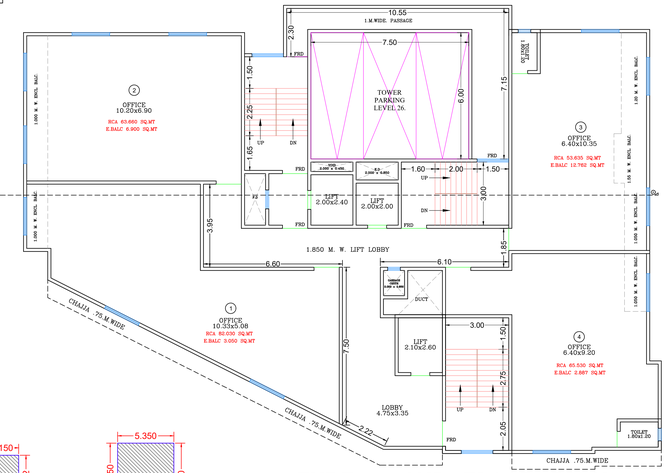

TYPE-A 2ND FLOOR PLAN

SCALE 1:100

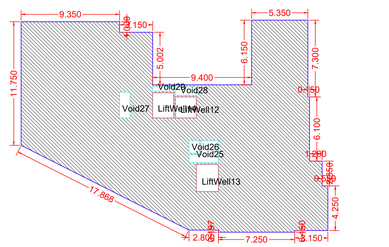

BUILT-UP AREA CALCULATION
1ST FLOOR TYPE-A

SCALE 1:200

BUILT UP AREA CALCULATION FOR SECTION-1 BLOCK C			
AREA NAME	LENGTH	WIDTH	AHA(SQ.M)
BLOCK	35.350	26.150	459.455
		BLOCK AREA TOTAL =459.455Sq.M	
void24	-	-	2.451
void23	-	-	5.950
void22	-	-	7.250
void21	-	-	7.250
LiftWell11	-	-	5.400
LiftWell10	-	-	4.800
LiftWell9	-	-	4.800
		TOTAL Deduction =35.901Sq.M	
		Net Builtup Area =423.554 Sq.M	

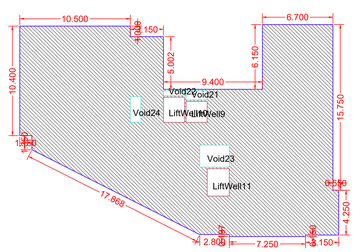

BUILT-UP AREA CALCULATION
2ND FLOOR TYPE-A

SCALE 1:200

PROFORMA - I

A		AREA STATEMENT	IN SQ.MT.
1	A)	AREA OF PLOT	
	a)	AS PER OWNERSHIP DOCUMENT (7/12) (3684.550 + 202.000 = 3886.550)	3886.55
	b)	AS PER MEASUREMENT SHEET	3886.55
	c)	AS PER SITE POSSESION (3468.000 + 202.000 = 3670.000)	3670.00
2		DEDUCTIONS FOR	
	a)	30.00 M. W. D.P. ROAD AREA PROP.	12.00
	b)	9.00 M. W. D.P. ROAD AREA AS PER SANCTION	480.00
	c)	ANY RESERVATION	0.00
		TOTAL (a+b+c)	492.00
3		BALANCE AREA OF PLOT (1 Minus 2)	3178.000
4		AMMENITY SPACE IF APPLICABLE	--
	a)	REQUIRED	--
	b)	ADJUSTMENT OF IF ANY	--
	c)	BALANCE PROPOSED	--
5		NET PLOT AREA (3-4 (C))	3178.000
6		RECREATIONAL OPEN SPACE (IF APPLICABLE)	--
	a)	REQUIRED R.G.	--
	b)	PROPOSED R.G.	--
7		INTERNAL ROAD AREA	--
8		PLOTABLE AREA	--
9		BUILT UP AREA WITH REF. TO BASIC FSI AS PER FRONT ROAD WIDTH (SR.NO.-5 X BASIC FSI) 3178.000 X 1.10 = 3495.800	3495.800
10		ADDITION OF FSI ON PAYMENT PREMIUM	
		MAXIMUM PERMISSIBLE PREMIUM FSI BASED ON ROAD WIDTH/TOD ZONE	
		PROPOSED FSI ON PAYMENT OF PREMIUM 3670.000 X 0.5 = 1835.000	1835.000
11		IN-SITU FSI/TDR LOADING	--
	a)	D.P. ROAD 30.00M & 9.00 M 480.00 X 1.00= 480.00 12.00 X 2.00= 24.00	504.000
	b)	TDR AREA 3670.00 X 1.40 = 5138.000 - 504.000 - 1050.000= 3584.000	3584.000
	c)	TOTAL IN-SITU/TDR LOADING PROPOSED (11 (a)+(b)+(c)	4088.000
12		ADDITIONAL FSI AREA UNDER CHAPTER NO.7 70 TENANTS X 15 = 1050.00	1050.000
13		TOTAL ENTITLEMENT OF FSI IN THE PROPOSAL	
14	a)	[9+10+11(c) or 12 WHICHEVER IS APPLICABLE	10468.800
	b)	ANCILLARY AREA FSI UPTO 60% OR 80% WITH PAYMENT OF CHARGES 10468.800 -109.00 = 10359.800 SQ.MT; COMMERCIAL AREA 1286.701 X 0.8 = 1029.360 SQ.MT; RESIDENTIAL AREA 9085.494 X 0.6 = 5451.296 SQ.MT; TOTAL = 6480.656 SQ.MT; OUT OF THIS = 6402.684 SQ.MT	6402.684
	c)	TOTAL ENTITLEMENT (a+b)	16871.484
15		TOTAL BUILT UP AREA IN PROPOSAL (EXCLUDING AREA AT SR. NO.17(b)	
	a)	PROPOSED BUILT UP AREA (AS PER P LINE)	16762.484
	b)	EXISTING BUILT UP AREA AS PER SANCTION	109.000
	c)	TOTAL (a+b)	16871.484
16		FSI CONSUMED (15/13)	
17		AREA FOR INCLUSIVE HOUSING IF ANY	
	a)	REQUIRED (20% OF SR. NO.-9)	
	b)	PROPOSED (20% OF SR. NO.-9)	

Proforma 1 : Area Statement

1. Area of plot(Minimum area of a, b, c to be considered) or area of subplot with sanctioned layout No. and subplot No.	3670.000
(a) As per ownership document (7/12, CTS extract)	3670.000
(b) as per TILR or City Survey measurement sheet	3670.000
(c) as per Demarcated drawing area	3670.000
LESS	
2.Area not in possession	0.000
3. Area Proposed for development (out of 1-2)	3670.000
4.Deductions for(out of 3)	
(a) Proposed D.P./ D.P. Road widening Area/Proposed DP road, Road under MMC act	492.000
(b) Any D.P. Reservation area	0.000
(c) Green Belt	0.000
(Total a+b+c)	492.000
5. Balance area of plot (3-4)	3178.000
6. Amenity Space Proposed	0.000
(Required -(a) Upto 20,000 sqmt - Nil	-
(b) Above 20,000 and more - (a) + 5% of Total area	0.000
7. Net Plot Area (5-6)	3178.000
8.Recreational Open Space (Not applicable if plots are from sanctioned layout)	-
(a). If area is more than (5) 4000 sqmt - 10 % of (5) is required.	0.000
Proposed	0.000
(A)10 % Subject to minimum 200 sqmt(Not applicable if plots are from sanctioned layout or each plot admeuring less than 4000sq.m regularised under gunthewari act)	0.000
Proposed	0.000
(B)Exemption to leave open space subject to availing basic F.S.I. of 75 %	-
(C)Exemption to leave open space subject to payment of 10 % land value of land at (?) as per annual statement of rate.	-
If (5) > 4000sq.m then Land admeuring 20% of (5) is to be utilised for inclusive housing	0.000
Proposed Area	0.000
Architect/ Licensed Engineer/ Supervisor name and signature	
Registration No. of Architect/ License no. of Licensed Engineer/ Supervisor. CA/2019/106930	

AMBER CO-OP.H.SOCIOETY & G.H.KOLTE & OTHERS.
POA,M/S MIDAS CREATORS.
THROUGH MR.PRANAV PRAKASH PENKAR
Postal Address : 302-Morya Apartment,Titak Chowk,Kalyan,Thane,Maharashtra-421301,1st floor, Shared Complex, Oak

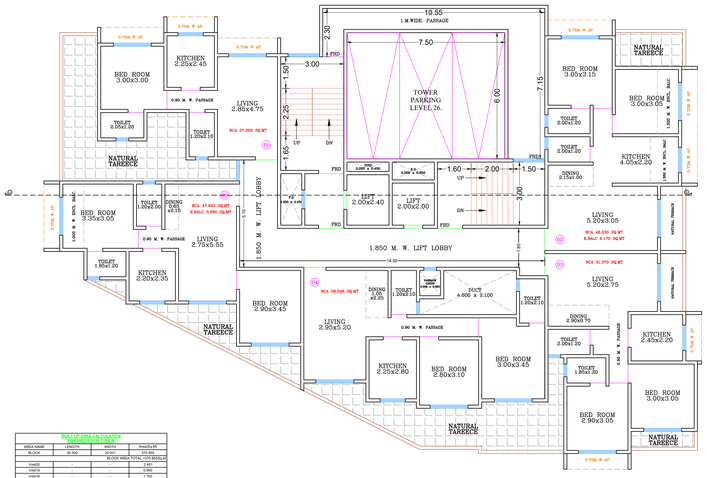

BUILT UP AREA CALCULATION FOR 3RD FLOOR TYPE A

AREA NAME	LENGTH	WIDTH	Area(Sq.M)
BLOCK	30.300	20.001	374.492
		BLOCK AREA TOTAL =374.492Sq.M	
Void10	-	-	2.401
Void18	-	-	2.900
Void19	-	-	1.700
Void17	-	-	1.200
Void16	-	-	8.107
LiftWell6	-	-	4.800
LiftWell7	-	-	4.500
		TOTAL Deduction =23.108Sq.M	
		Net Built-Up Area =351.384 Sq.M	

TYPE–A 3RD FLOOR PLAN
SCALE 1:100

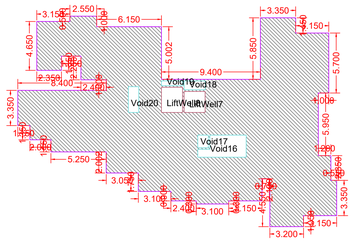

BUILT–UP AREA CALCULATION 3RD FLOOR TYPE–A
SCALE 1:200

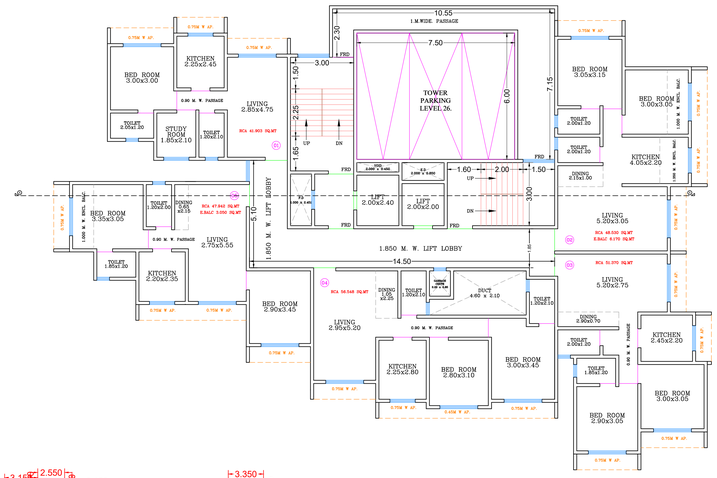

TYPE–A 4TH TO 6TH & 8TH FLOOR PLAN
SCALE 1:100

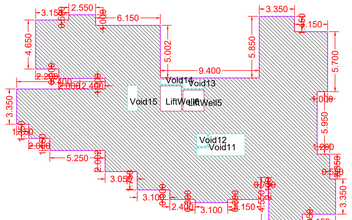

BUILT UP AREA CALCULATION FOR 4TH TO 6TH & 8TH FLOOR TYPE A

AREA NAME	LENGTH	WIDTH	Area(Sq.M)
BLOCK	30.300	20.001	365.153
		BLOCK AREA TOTAL =365.153Sq.M	
Void15	-	-	2.401
Void14	-	-	4.800
Void13	-	-	1.200
Void12	-	-	1.200
Void11	-	-	8.107
LiftWell4	-	-	4.800
LiftWell5	-	-	4.500
		TOTAL Deduction =23.108Sq.M	
		Net Built-Up Area =342.045 Sq.M	

BUILT–UP AREA CALCULATION 4TH TO 6TH & 8TH FLOOR TYPE–A
SCALE 1:200

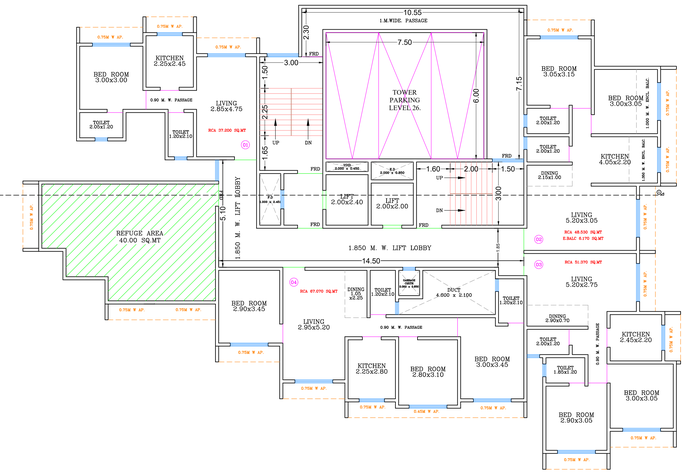

TYPE–A 7TH 12TH & 17TH FLOOR PLAN
SCALE 1:100

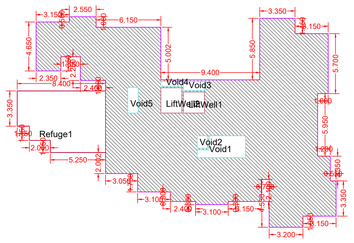

BUILT UP AREA CALCULATION FOR 7TH 12TH & 17TH FLOOR TYPE A

AREA NAME	LENGTH	WIDTH	Area(Sq.M)
BLOCK	30.300	20.001	374.492
		BLOCK AREA TOTAL =374.492Sq.M	
Refuge1	-	-	42.880
Void5	-	-	2.401
Void4	-	-	4.800
Void3	-	-	1.700
Void2	-	-	1.200
Void1	-	-	8.107
LiftWell1	-	-	4.800
LiftWell2	-	-	4.500
		TOTAL Deduction =69.588Sq.M	
		Net Built-Up Area =304.904 Sq.M	

BUILT–UP AREA CALCULATION 7TH 12TH & 17TH FLOOR TYPE–A
SCALE 1:200

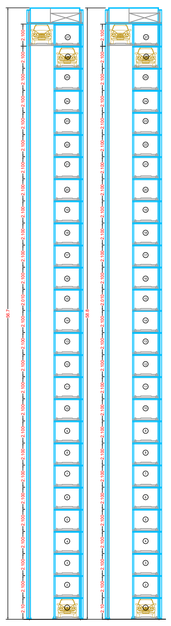

PARKING TOWER TYPE–A
SCALE 1:200

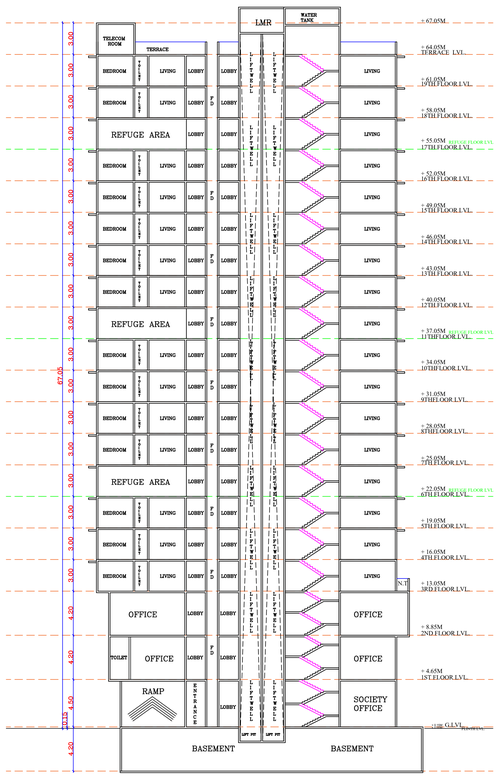

TYPE–A SECTION PLAN A–A
SCALE 1:200

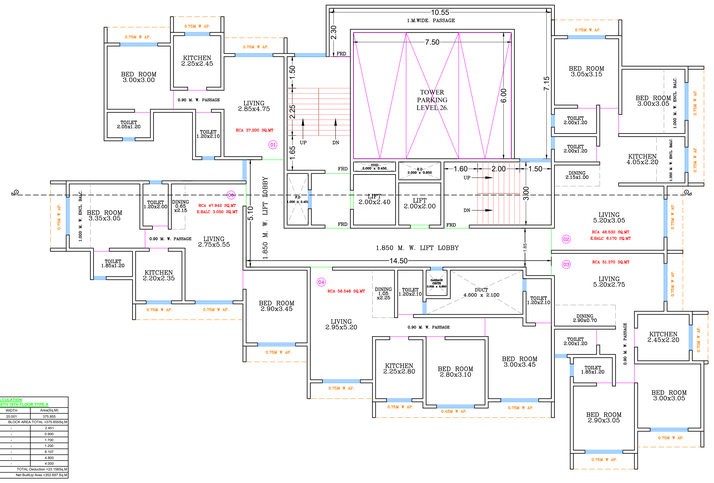

TYPE–A 9TH TO 11TH 13TH TO 16TH 18TH & 19 FLOOR PLAN
SCALE 1:100

BUILT UP AREA CALCULATION FOR 9TH TO 11TH 13TH TO16TH 18TH 19TH FLOOR TYPE A

AREA NAME	LENGTH	WIDTH	Area(Sq.M)
BLOCK	30.300	20.001	374.492
		BLOCK AREA TOTAL =374.492Sq.M	
Void10	-	-	2.401
Void9	-	-	2.900
Void8	-	-	1.700
Void7	-	-	1.200
Void6	-	-	8.107
LiftWell3	-	-	4.800
LiftWell4	-	-	4.500
		TOTAL Deduction =25.108Sq.M	
		Net Built-Up Area =349.384 Sq.M	

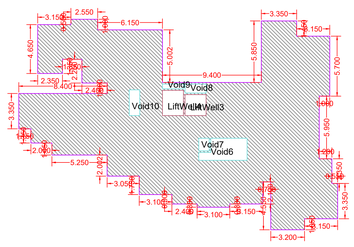

BUILT–UP AREA CALCULATION 9TH TO 11TH 13TH TO16TH 18TH 19TH FLOOR TYPE–A
SCALE 1:200

BUILT UP AREA CALCULATION FOR TERRACE FLOOR TYPE A

AREA NAME	LENGTH	WIDTH	Area(Sq.M)
BLOCK	3.700	3.350	12.395
		BLOCK AREA TOTAL =12.395Sq.M	
		TOTAL Deduction =0.000Sq.M	
		Net Built-Up Area =12.395 Sq.M	

BUILT–UP AREA CALCULATION TERRACE FLOOR TYPE–A
SCALE 1:200

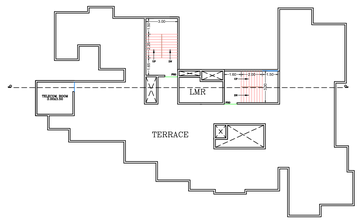

TYPE–A TERRACE FLOOR PLAN
SCALE 1:100

FLOOR PLAN TYPE A | SHEET NO. 2/4

Proforma : I : Area Statement

1. Area of plot(Minimum area of a, b, c to be considered) or area of subplot with sanctioned layout No. and subplot No.	3670.000
(a) As per ownership document (7/12, CTS extract)	3670.000
(b) as per TILR or City Survey measurement sheet	3670.000
(c) as per Demarcated drawing area	3670.000
LESS	
2.Area not in possession	0.000
3. Area Proposed for development (out of 1-2)	3670.000
4.Deductions for(out of 3)	
(a) Proposed D.P./ D.P. Road widening Area/Proposed DP road, Road under MMC act	492.000
(b) Any D.P. Reservation area	0.000
(c) Green Belt	0.000
(Total a+b+c)	492.000
5. Balance area of plot (3-4)	3178.000
6. Amenity Space Proposed	0.000
(Required -(a) Upto 20,000 sqmt - Nil	-
(b) Above 20,000 and more - (a) + 5% of Total area	0.000
7. Net Plot Area (5-6)	3178.000
8.Recreational Open Space (Not applicable if plots are from sanctioned layout)	-
(a). If area is more than (5) 4000 sqmt - 10 % of (5) is required.	0.000
Proposed	0.000
(A)10 % Subject to minimum 200 sqmt(Not applicable if plots are from sanctioned layout or each plot admeuring less than 4000sq.m regularised under gunthewari act)	0.000
Proposed	0.000
(B)Exemption to leave open space subject to availing basic F.S.I. of 75 %	-
(C)Exemption to leave open space subject to payment of 10 % land value of land at (7) as per annual statement of rate.	-
If (5) > 4000sq.m then Land admeuring 20% of (5) is to be utilised for inclusive housing	0.000
Proposed Area	0.000
Architect/ Licensed Engineer/ Supervisor name and signature	
Registration No. of Architect/ License no. of Licensed Engineer/ Supervisor: CA/2019/106930	

AMBER CO-OP.H.SCOCIETY & G.H.KOLTE & OTHERS.
POA M/S MIDAS CREATORS.
THROUGH MR.PRANAV PRAKASH PENKAR
Postal Address : 302-Morya Apartment,Tilak Chowk,Kalyan,Thane,Maharashtra-421301,1st floor, Sharad Complex, Oak Bagh , near kalyan station west, 421301

DESCRIPTION OF PROJECT :

Type of Proposal : Mixed
BUILDING ON CTS. NO. 3360,3361,3362,3363, AT. KALYAN, TAL-KALYAN, DIST-THANE
SITE ADDRESS :
CTS NO. 3360,3361,3362,3363, AT. KALYAN, TAL-KALYAN, DIST-THANE

Name Of Architect : Tejas Anil Nirgude

LOGO	ADDRESS OF OFFICE
	OFFICE - 5TH FLOOR, MIDTOWN EMBASSY, BEHIND VASANT VALLEY BUS DEPOT, OPP. NARAYANA SCHOOL, GANDHARE, KALYAN - 421301

OWNERS SIGN -	TECHNICAL PERSON SIGN
	TEJAS ANIL NIRGUDE Digitally signed by TEJAS ANIL NIRGUDE Date: 2026.01.20 11:46:49 +05'30'
SCALE -	DATE: Date: 20/01/26
JOB NO - KDMCC-26-01792	CHECK BY - ANIL

SUBMISSION DRAWING

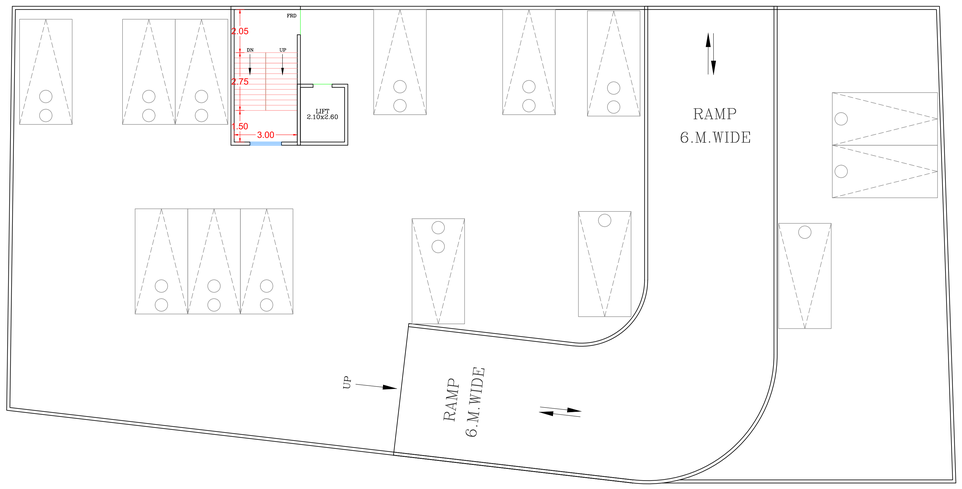

TYPE–B BASEMENT FLOOR PLAN
SCALE 1:100

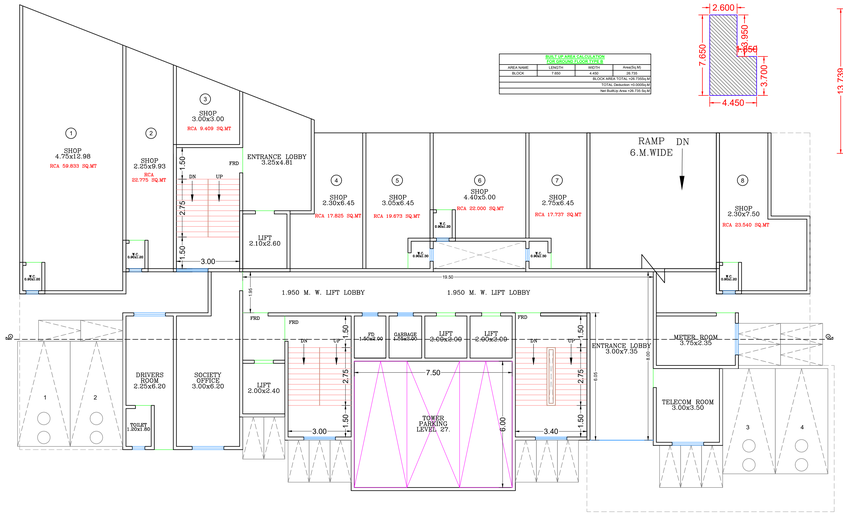

AREA NAME	LENGTH	WIDTH	Area(Sq.M)
BLOCK	2.600	10.700	27.820
		BLOCK AREA TOTAL=27.820SQ.M	
		TOTAL Deduction=0.000SQ.M	
		Net Builtup Area=27.820 Sq.M	

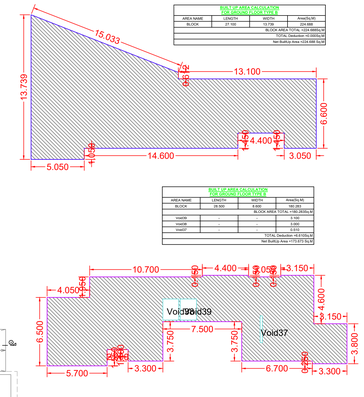

AREA NAME	LENGTH	WIDTH	Area(Sq.M)
BLOCK	39.700	19.200	762.240
		BLOCK AREA TOTAL=762.240SQ.M	
void1	-	-	1.950
void2	-	-	2.340
void3	-	-	3.510
void4	-	-	2.340
void5	-	-	2.340
void6	-	-	4.387
void7	-	-	1.463
void8	-	-	1.463
void9	-	-	3.510
void10	-	-	4.387
void11	-	-	1.463
void12	-	-	1.463
void13	-	-	3.510
void934	-	-	4.387
void935	-	-	1.463
void936	-	-	1.463
void937	-	-

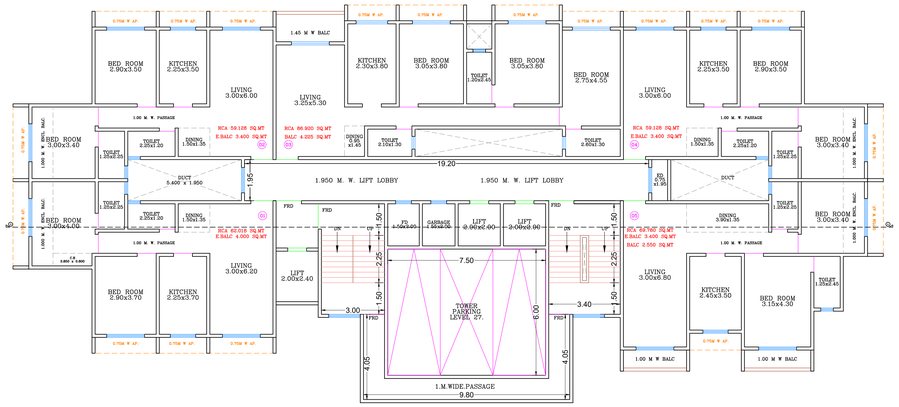

TYPE-B 5TH FLOOR PLAN

SCALE 1:100

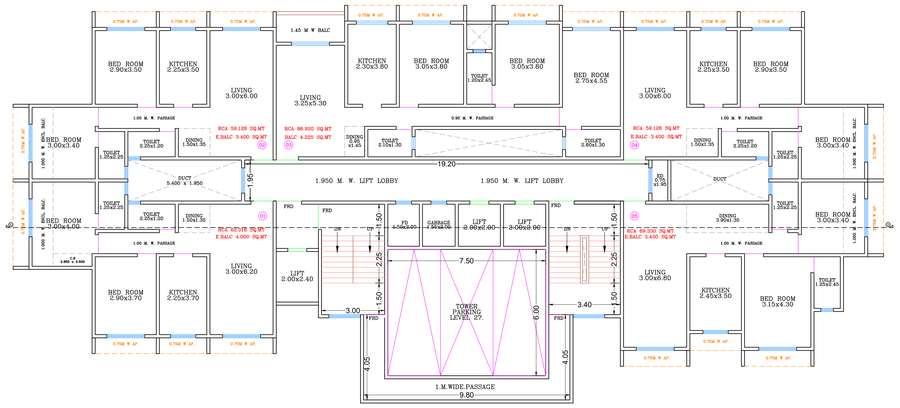

TYPE-B 6TH 8TH TO 11 13 TO 16 & 18TH 20TH FLOOR PLAN

SCALE 1:100

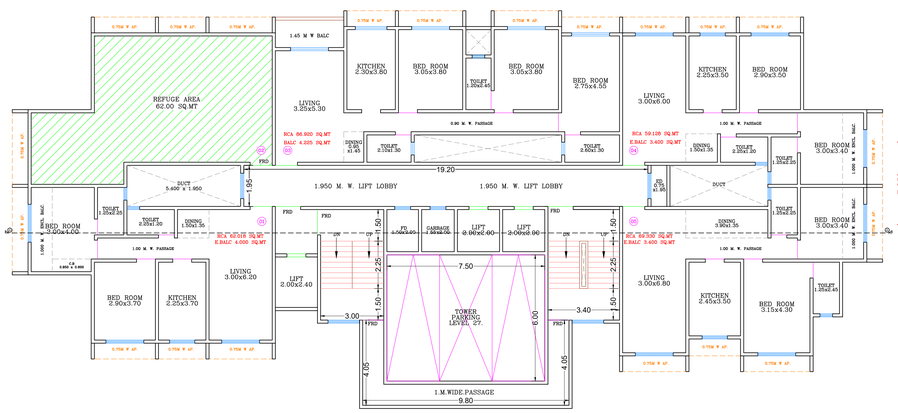

TYPE-B 7TH 12TH 17TH FLOOR PLAN

SCALE 1:100

BUILT UP AREA CALCULATION
FOR STILT FLOOR TYPE-B

AREA NAME	LENGTH	WIDTH	Area(SQ.M)
BLOCK	39.800	15.100	533.205
		BLOCK AREA TOTAL =539.315SQ.M	
Void11	-	-	3.000
Void12	-	-	3.100
Void13	-	-	1.463
Void8	-	-	0.410
LiftWell8	-	-	4.800
LiftWell9	-	-	4.800
LiftWell7	-	-	4.000
Duct8	-	-	10.530
Duct9	-	-	6.150
Duct7	-	-	3.067
TOTAL Deduction =44.319Sq.M			
Net Built Up Area=1471.18 Sq.M			

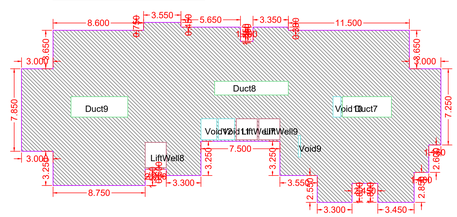

BUILT-UP AREA CALCULATION
5RD FLOOR TYPE-B

SCALE 1:200

BUILT UP AREA CALCULATION
FOR STILT FLOOR TYPE-B

AREA NAME	LENGTH	WIDTH	Area(SQ.M)
BLOCK	39.800	15.100	533.205
		BLOCK AREA TOTAL =539.315SQ.M	
Void6	-	-	3.000
Void7	-	-	3.100
Void8	-	-	1.463
Void9	-	-	0.410
LiftWell6	-	-	4.800
LiftWell7	-	-	4.800
LiftWell4	-	-	4.000
Duct6	-	-	10.530
Duct5	-	-	6.150
Duct4	-	-	3.067
TOTAL Deduction =44.319Sq.M			
Net Built Up Area =1471.18 Sq.M			

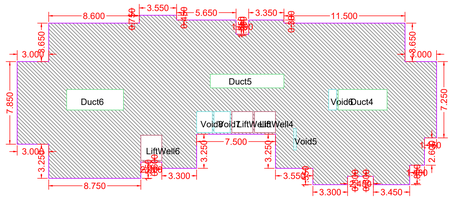

BUILT-UP AREA CALCULATION
6TH 8TH TO 11 13 TO 16
& 20TH FLOOR TYPE-B

SCALE 1:200

BUILT UP AREA CALCULATION
FOR STILT FLOOR TYPE-B

AREA NAME	LENGTH	WIDTH	Area(SQ.M)
BLOCK	39.800	15.100	533.205
		BLOCK AREA TOTAL =539.315SQ.M	
Refuge1	-	-	66.135
void4	-	-	3.000
void5	-	-	3.100
void6	-	-	1.463
void3	-	-	0.410
LiftWell3	-	-	4.800
LiftWell2	-	-	4.800
LiftWell1	-	-	4.000
Duct3	-	-	10.530
Duct2	-	-	6.150
Duct1	-	-	3.067
TOTAL Deduction =110.495Sq.M			
Net Built Up Area =428.819 Sq.M			

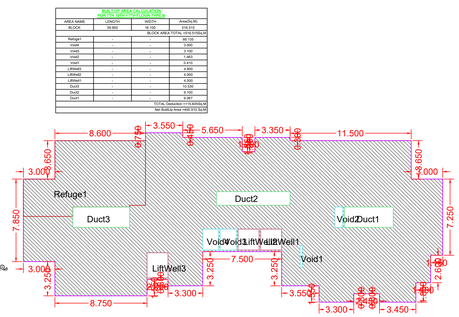

BUILT-UP AREA CALCULATION
7TH 12TH 17TH FLOOR TYPE-B

SCALE 1:200

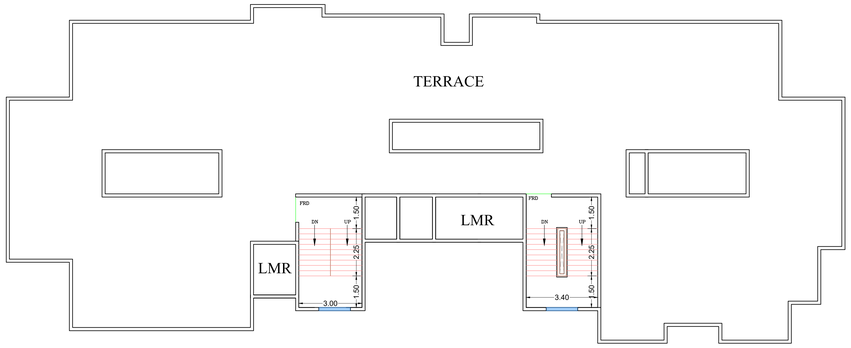

TERRACE FLOOR PLAN

SCALE 1:100

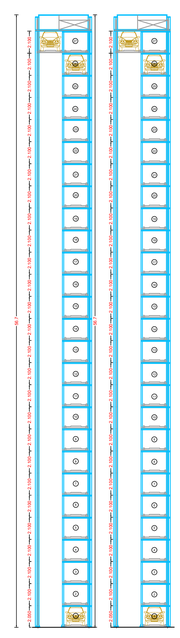

PARKING TOWER TYPE-B

SCALE 1:200

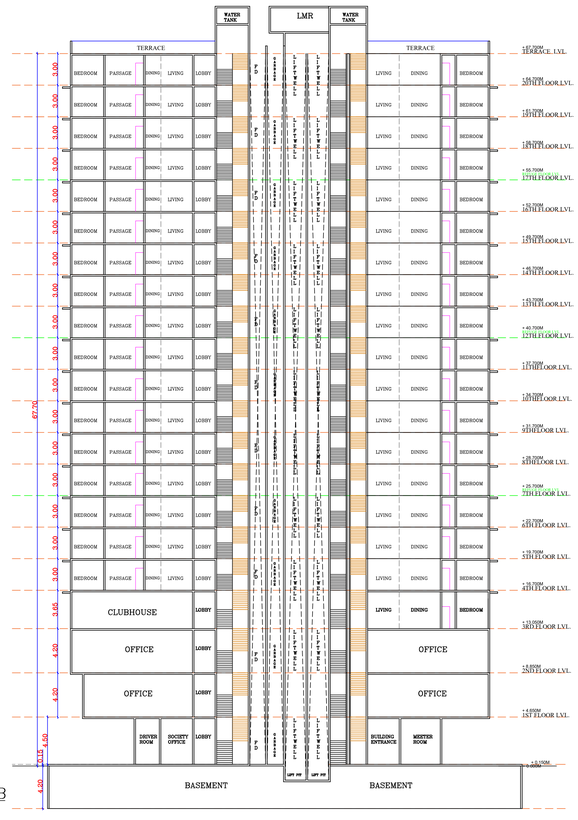

TYPE-B SECTION PLAN A-A

SCALE 1:200

FLOOR PLAN TYPE B | SHEET NO. 4/4

Proforma I : Area Statement

1. Area of plot(Minimum area of a, b, c to be considered) or area of subplot with sanctioned layout No. and subplot No.	3670.000
(a) As per ownership document (7/12, CTS extract)	3670.000
(b) as per TILR or City Survey measurement sheet	3670.000
(c) as per Demarcated drawing area	3670.000
LESS	
2.Area not in possession	0.000
3. Area Proposed for development (out of 1-2)	3670.000
4.Deductions for(out of 3)	
(a) Proposed D.P./ D.P. Road widening Area/Proposed DP road, Road under MMC act	492.000
(b) Any D.P. Reservation area	0.000
(c) Green Belt	0.000
Total a+b+c)	492.000
5. Balance area of plot (3-4)	3178.000
6. Amenity Space Proposed	0.000
(Required -(a) Upto 20,000 sqmt - Nil	-
(b) Above 20,000 and more - (a) + 5% of Total area	0.000
7. Net Plot Area (5-6)	3178.000
8.Recreational Open Space (Not applicable if plots are from sanctioned layout)	- -
(a). If area is more than (5) 4000 sqmt - 10 % of (5) is required.	0.000
Proposed	0.000
(A)10 % Subject to minimum 200 sqmt(Not applicable if plots are from sanctioned layout or each plot admesuring less than 4000sq.m regularised under gunthewari act)	0.000
Proposed	0.000
(B)Exemption to leave open space subject to availing basic F.S.I of 75 %	-
(C)Exemption to leave open space subject to payment of 10 % land value of land at (7) as per annual statement of rate.	-
If (5) > 4000sq m then Land admesuring 20% of (5) is to be utilised for inclusive housing	0.000
Proposed Area	0.000
Architect/ Licensed Engineer/ Supervisor name and signature	
Registration No. of Architect/ License no. of Licensed Engineer/ Supervisor: CA/2019/106930	

AMBER CO-OP.H.SCOCIETY & G.H.KOLTE & OTHERS.
POA,M/S MIDAS CREATORS.
THROUGH MR.PRANAV PRAKASH PENKAR
Postal Address : 302-Morya Apartment,Tilak Chowk,Kalyan,Thane,Maharashtra-421301,1st floor, Sharad Complex, Oak Bagh , near kalyan station west, 421301

DESCRIPTION OF PROJECT :

Type of Proposal : Mixed
BUILDING ON CTS. NO. 3360,3361,3362,3363, AT. KALYAN, TAL-KALYAN, DIST-THANE

SITE ADDRESS :
CTS NO. 3360,3361,3362,3363, AT. KALYAN, TAL-KALYAN, DIST-THANE

Name Of Architect : Tejas Anil Nirgude

LOGO	ADDRESS OF OFFICE
	OFFICE - 5TH FLOOR, MIDTOWN EMBASSY, BEHIND VASANT VALLEY BUS DEPOT, OPP. NARAYANA SCHOOL, GANDHARE, KALYAN - 421301

OWNERS SIGN -	TECHNICAL PERSON SIGN
	TEJAS ANIL NIRGUDE Digitally signed by TEJAS ANIL NIRGUDE Date: 2026.01.20 17:42:20 +05'30'

SCALE -	DATE: Date: 20/01/26
JOB NO - KDMCC-26-01792	CHECK BY - ANIL

SUBMISSION DRAWING