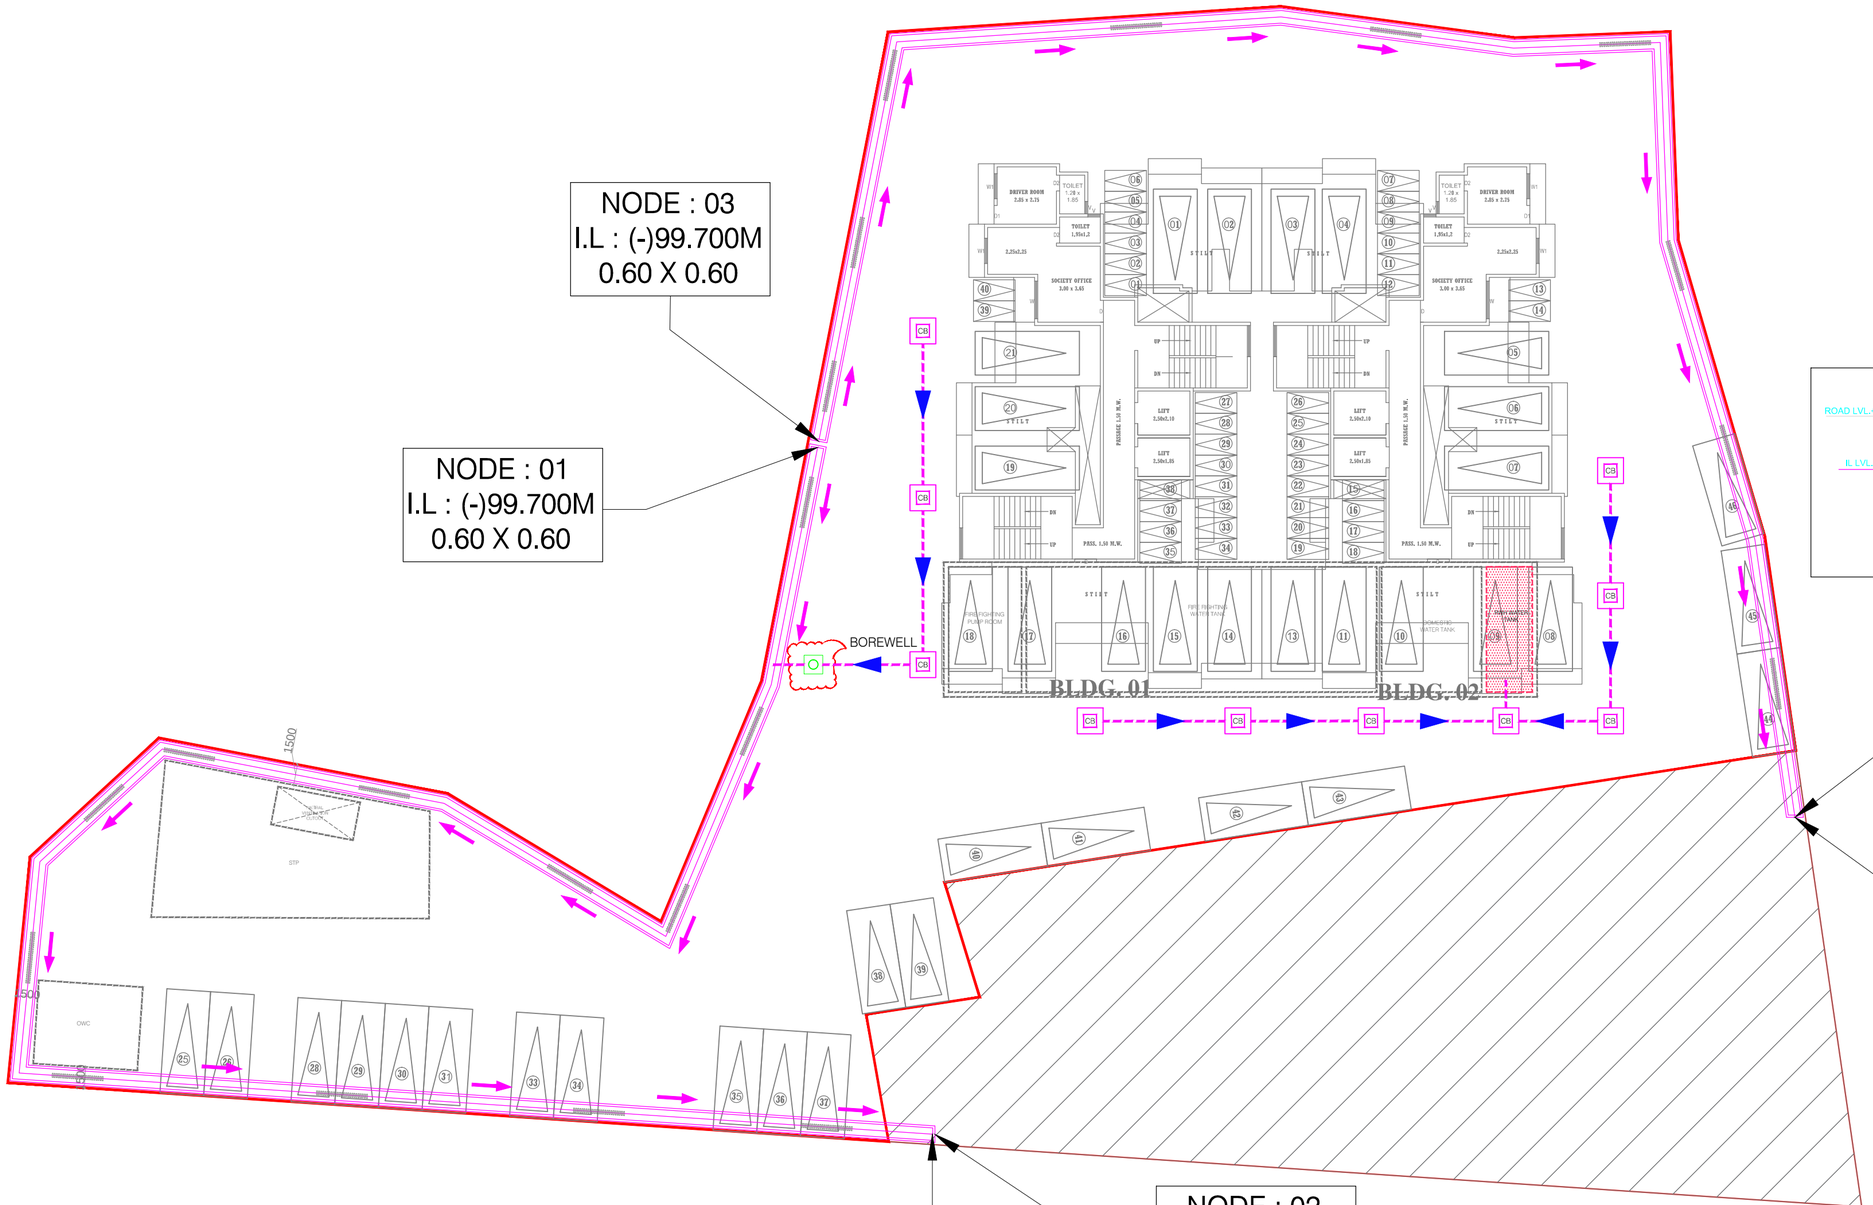

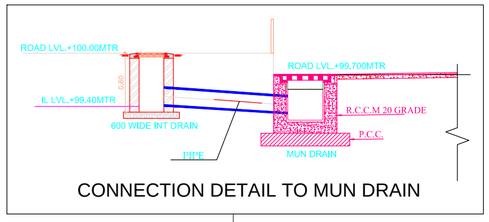

CONNECTION DETAIL TO MUN DRAIN

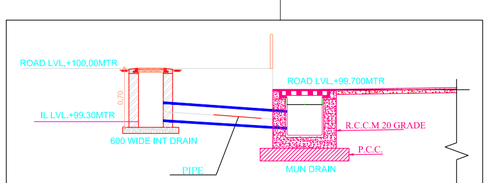

CONNECTION DETAIL TO MUN DRAIN

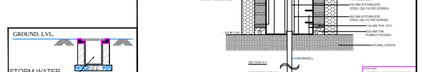

SWD CHANNEL DETAIL

TECHNICAL SPECIFICATIONS				
DIA IN INCH	MOC	SLOT SIZE IN MM	TOTAL LENGTH OF SCREEN SINGLE PIECE	TOTAL LENGTH OF SCREEN WITH END CONNECTION
6"	SS 304	00.50	1.0 MT.	1.9 MT.
12"	SS 304	00.75	1.0 MT.	1.6 MT.

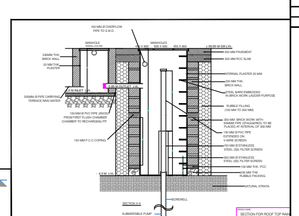

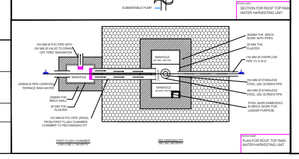

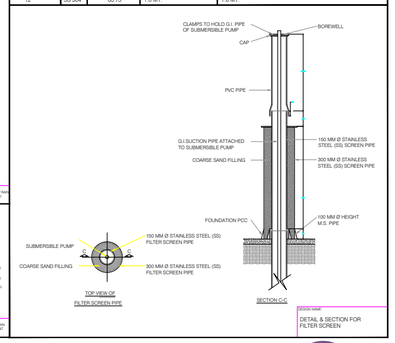

LEGEND :

SR. NO.	SYMBOL	DESCRIPTION
01.		150Ø SN8 FOAM CORE RW PIPE
02.	CB	300X300 CATCH BASIN

STORM WATER DRAIN & R.W.H. LAYOUT PLAN

LEGEND :

SR. NO.	SYMBOL	DESCRIPTION
01.		DOMESTIC TANK
02.		RWH TANK
03.		FIRE TANK
05.		PUMP ROOM

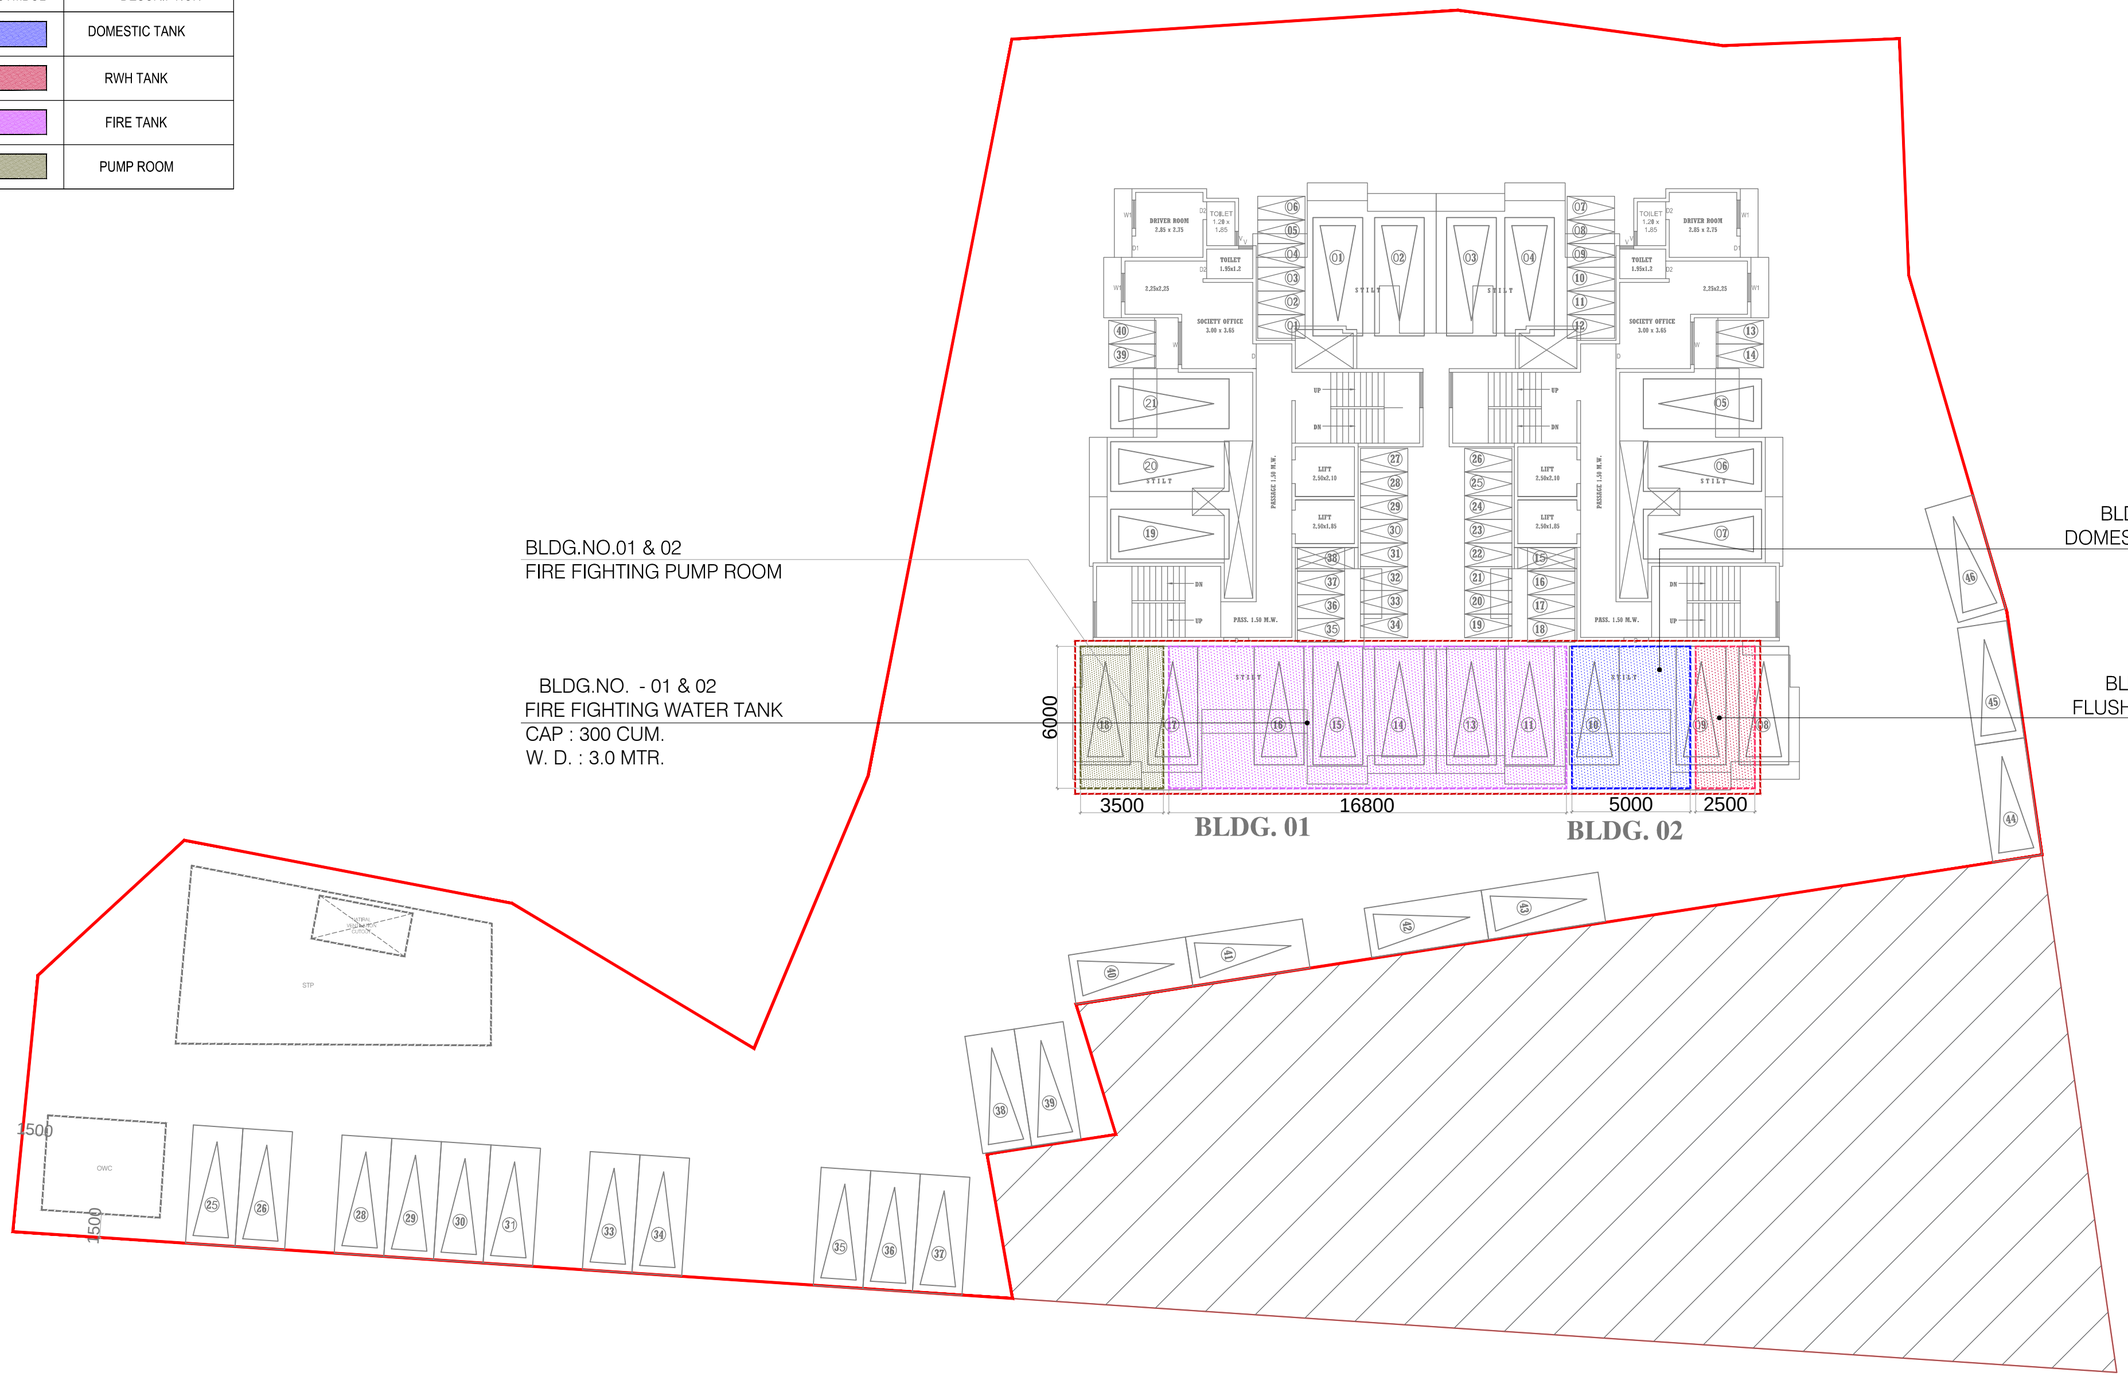

U.G.TANK DETAILS PLAN

ELCON ENGINEERS DOMBIVLI

H SKAR

Digitally signed by SUBODH GOTHOSKAR
DN: c=IN, o=PERSONAL, title=2743, pseudonym=a6b2cf06642f4e609443a721bd66f67f, 2.5.4.20=183ac62810c4ef7a873fc39d4297045bd3a4e2852f3a34bf1bd70cb479d7ad8a, postalCode=421301, st=Maharashtra, serialNumber=ef390763b4f8c691911fe25800f5aca39ca0755c25ec0b054694914168 7dd8988, cn=SUBODH GOTHOSKAR
Date: 2026.03.10 18:25:02 +05'30'