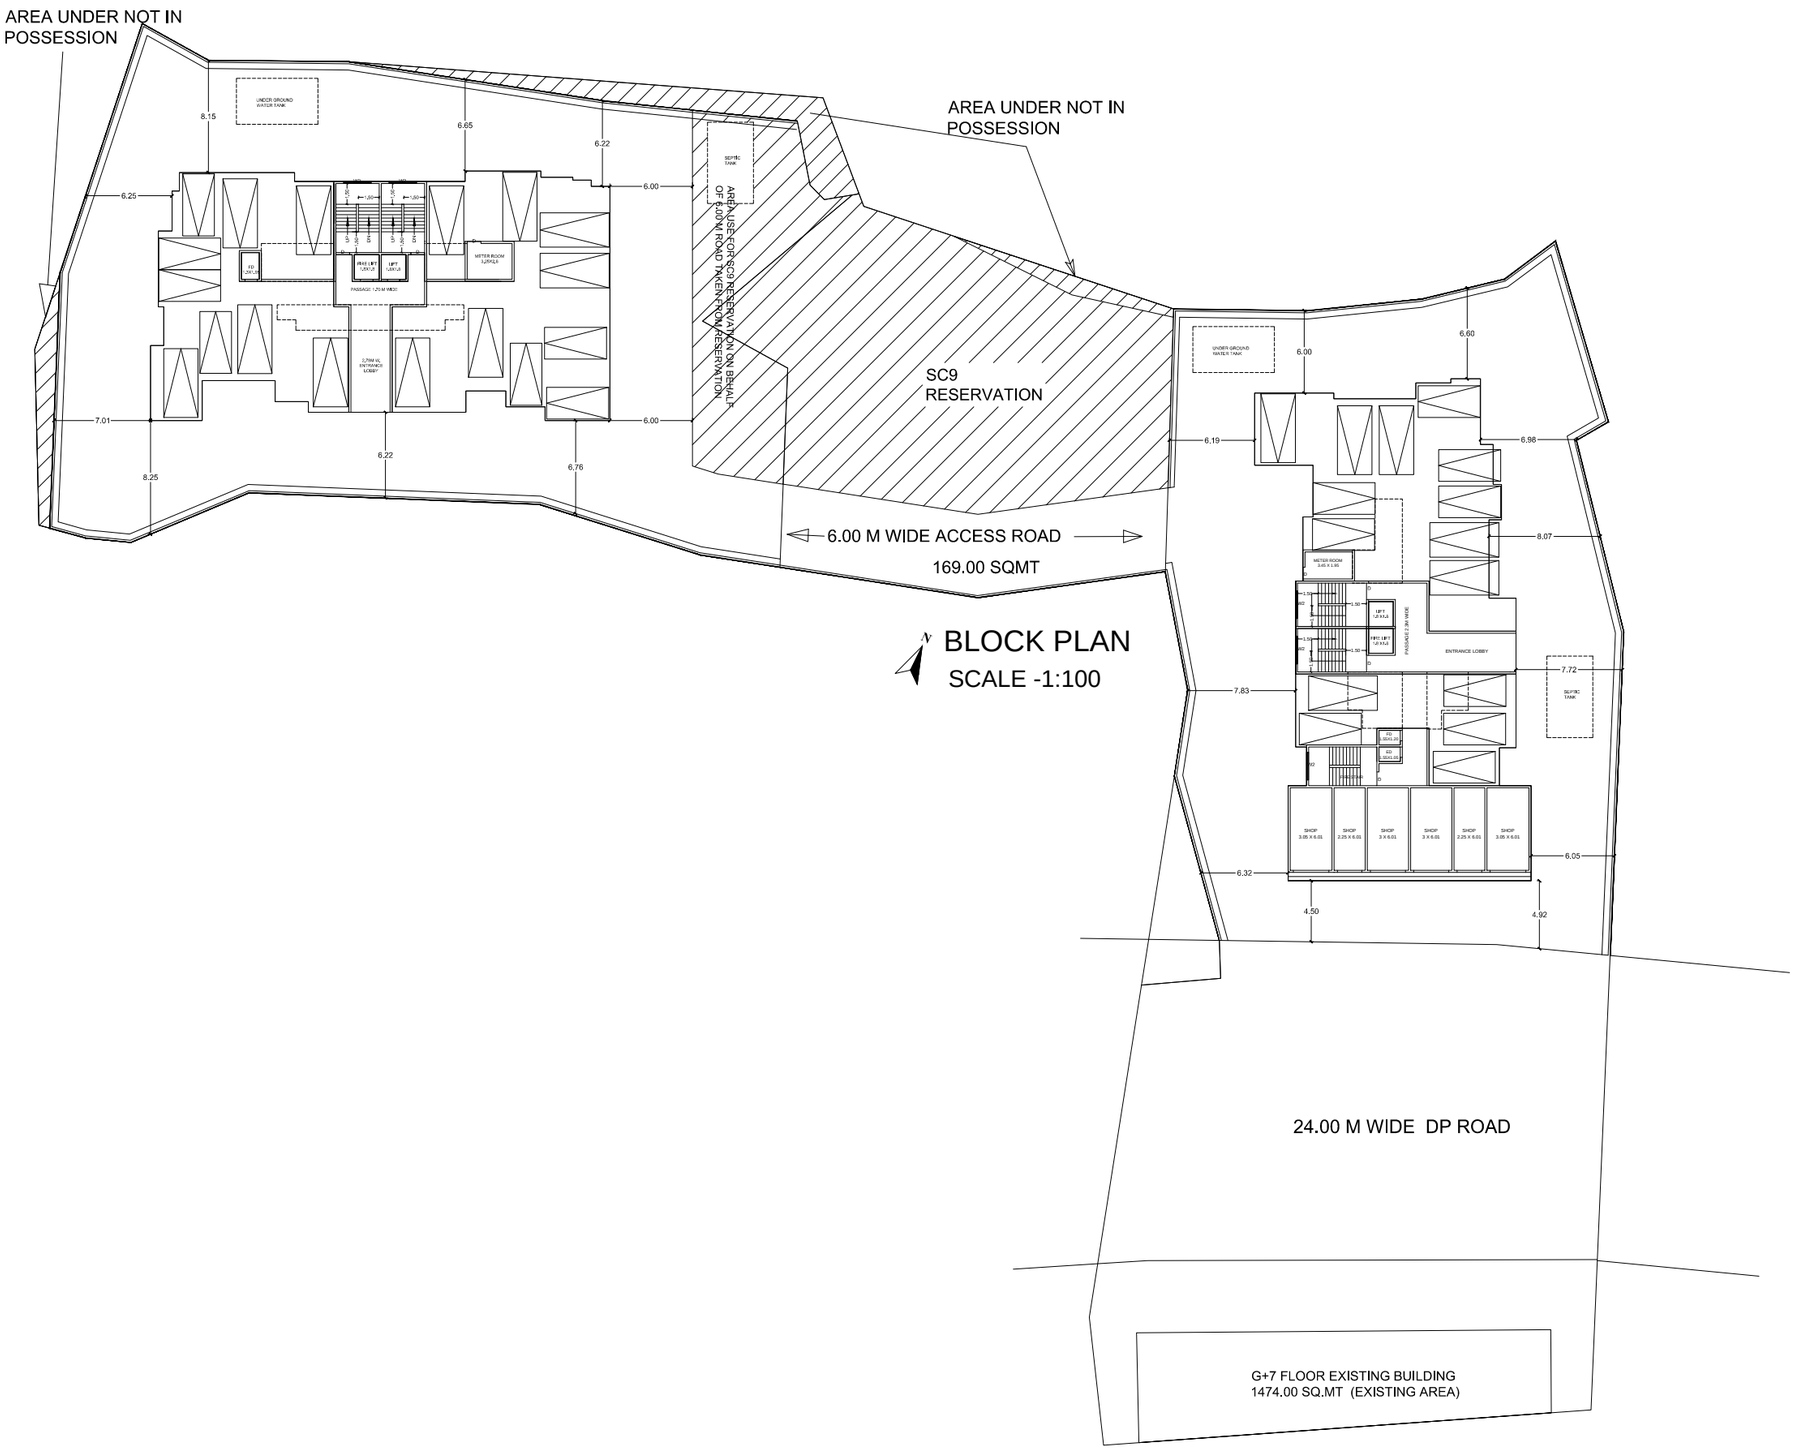
AREA UNDER NOT IN POSSESSION
AREA UNDER NOT IN POSSESSION
UNDER GROUND WATER TANK
SEPTIC TANK
AREA USE FOR SC9 RESERVATION ON BEHALF OF 6.00 M ROAD TAKEN FROM RESERVATION
SC9 RESERVATION
6.00 M WIDE ACCESS ROAD
169.00 SQMT
BLOCK PLAN
SCALE -1:100
METER ROOM 1.25X1.5
ENTRANCE LOBBY
PASSAGE 1.20 M WIDE
ENTRANCE LOBBY
SHOP 3.05 X 6.01
SHOP 2.25 X 6.01
SHOP 3 X 6.01
24.00 M WIDE DP ROAD
G+7 FLOOR EXISTING BUILDING
1474.00 SQ.MT (EXISTING AREA)

# BUILDING NO.01

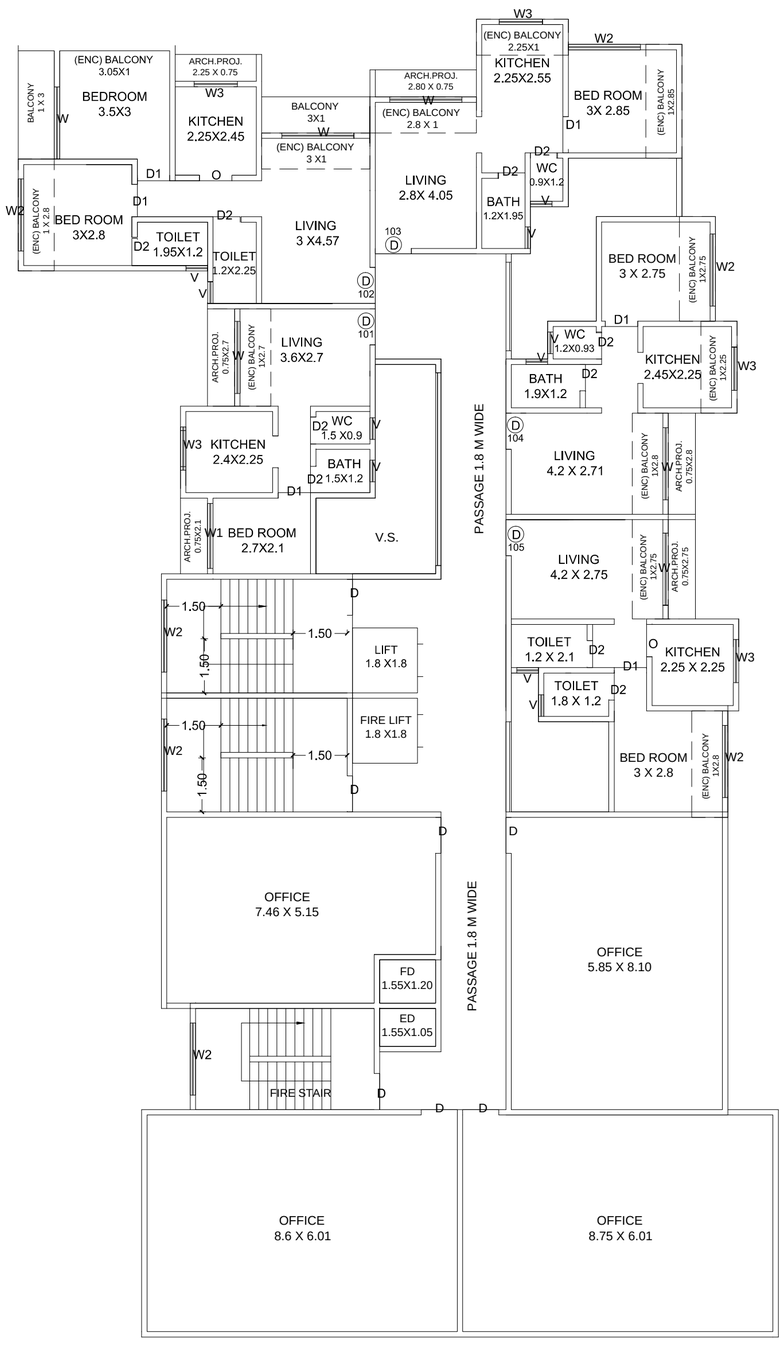


FIRST FLOOR

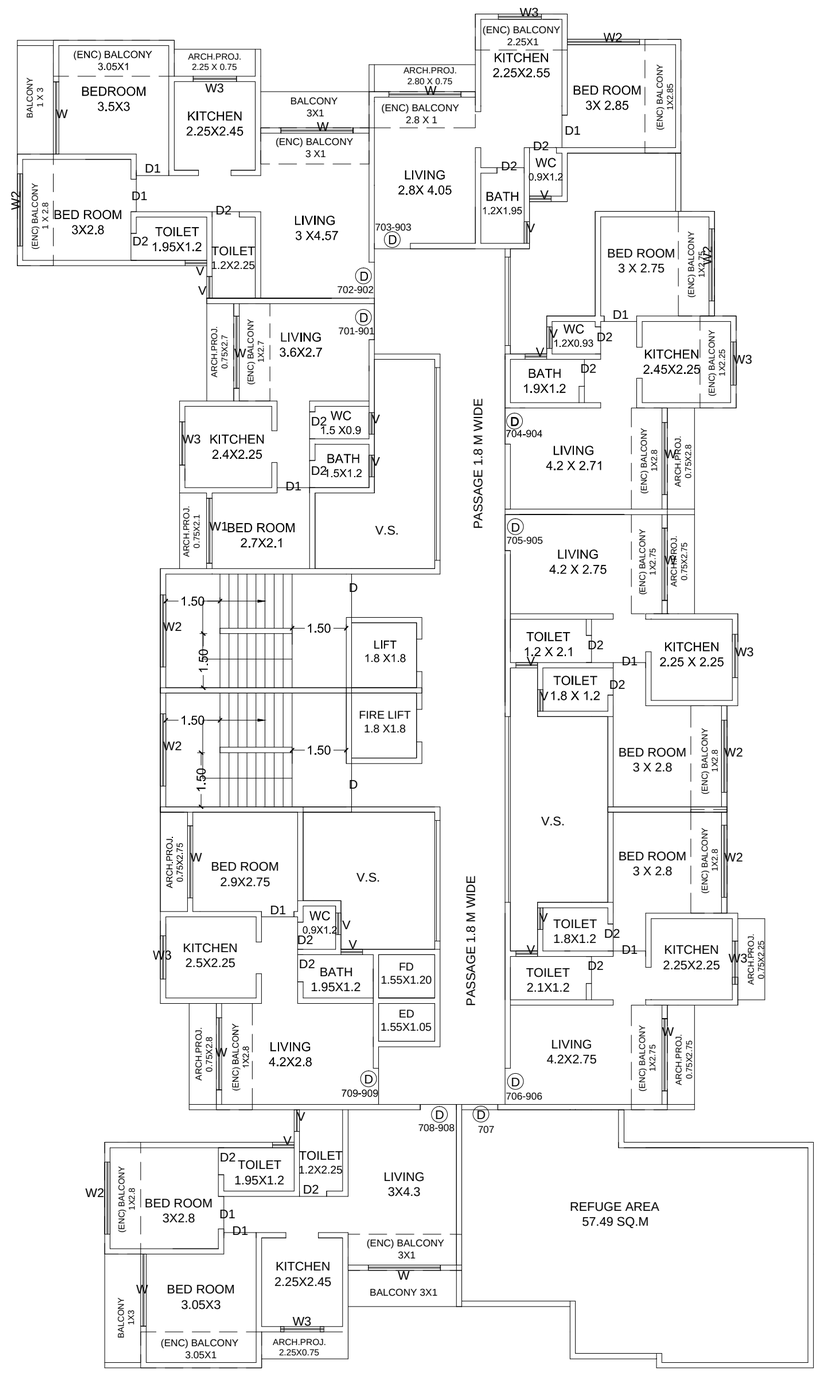


7TH & 13th REFUGE FLOOR

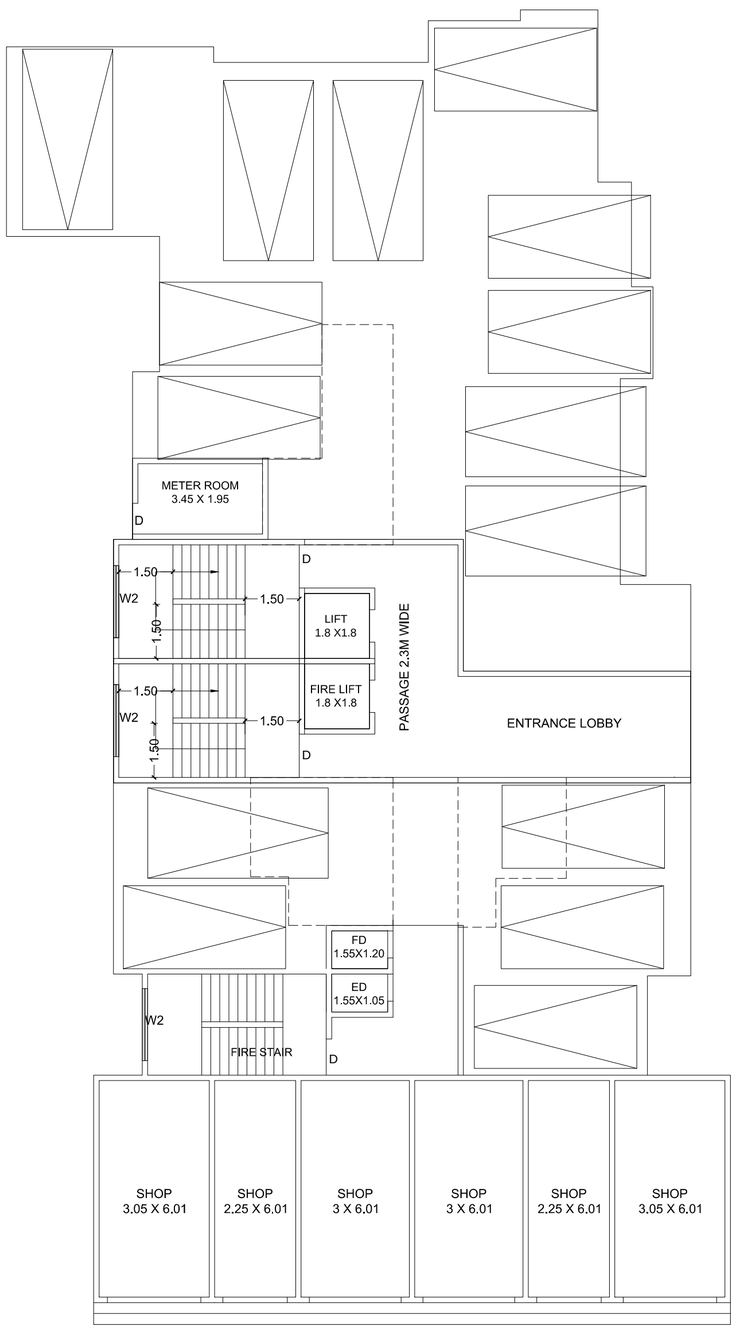


GROUND FLOOR

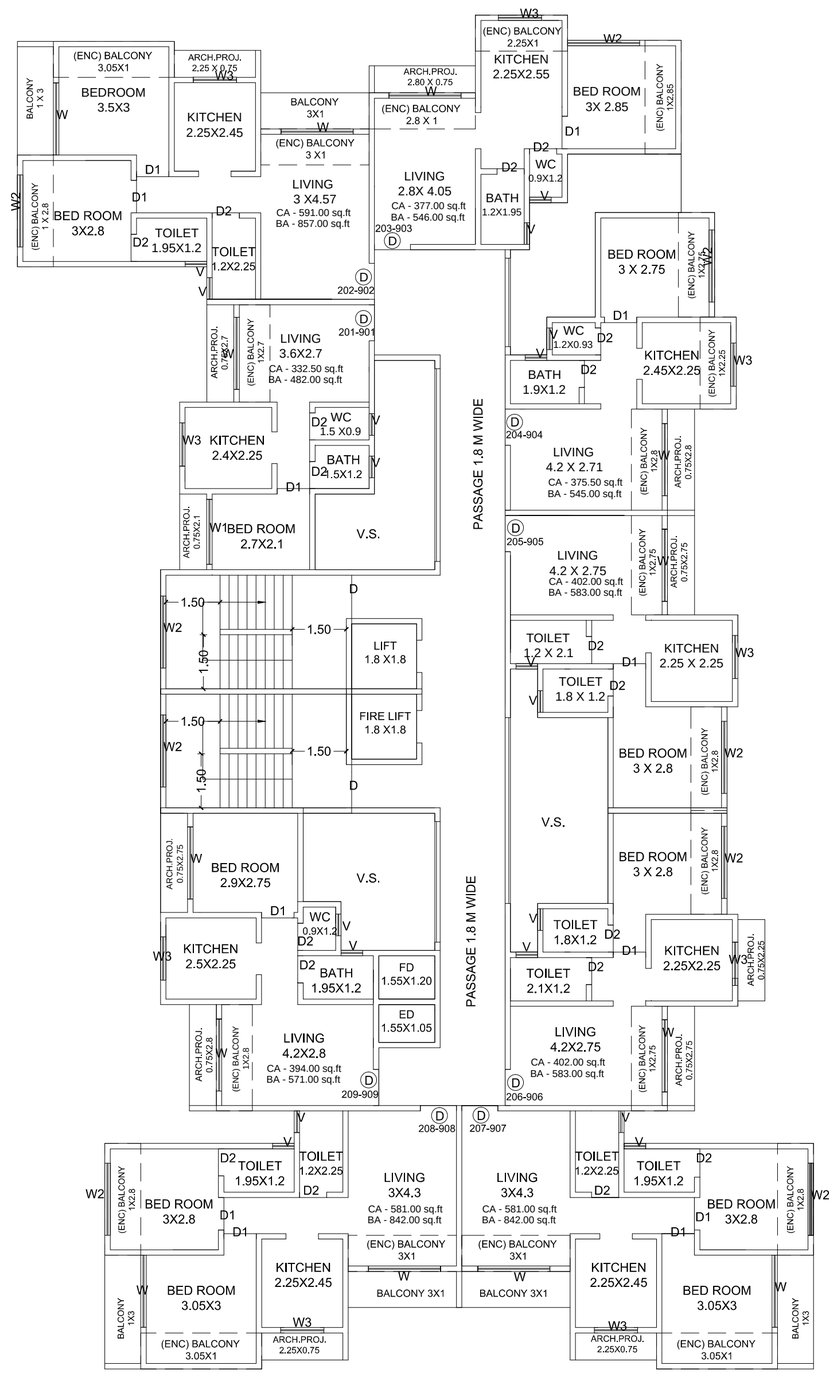


TYPICAL FLOOR(2ND-6TH & 8TH-12TH &14TH -18TH FLOOR)

# BUILDING NO.02

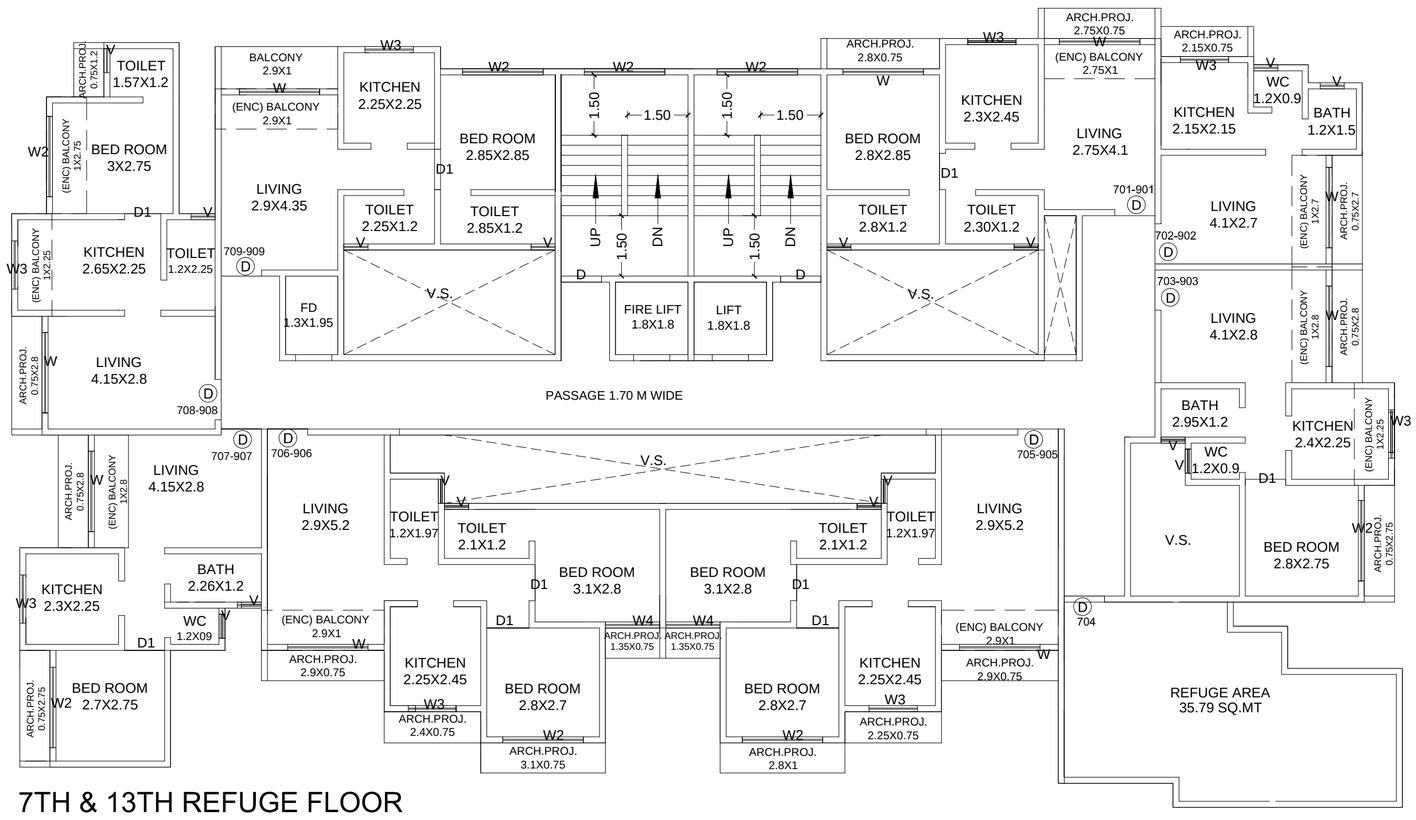


## 7TH & 13TH REFUGE FLOOR

SCALE 1:100

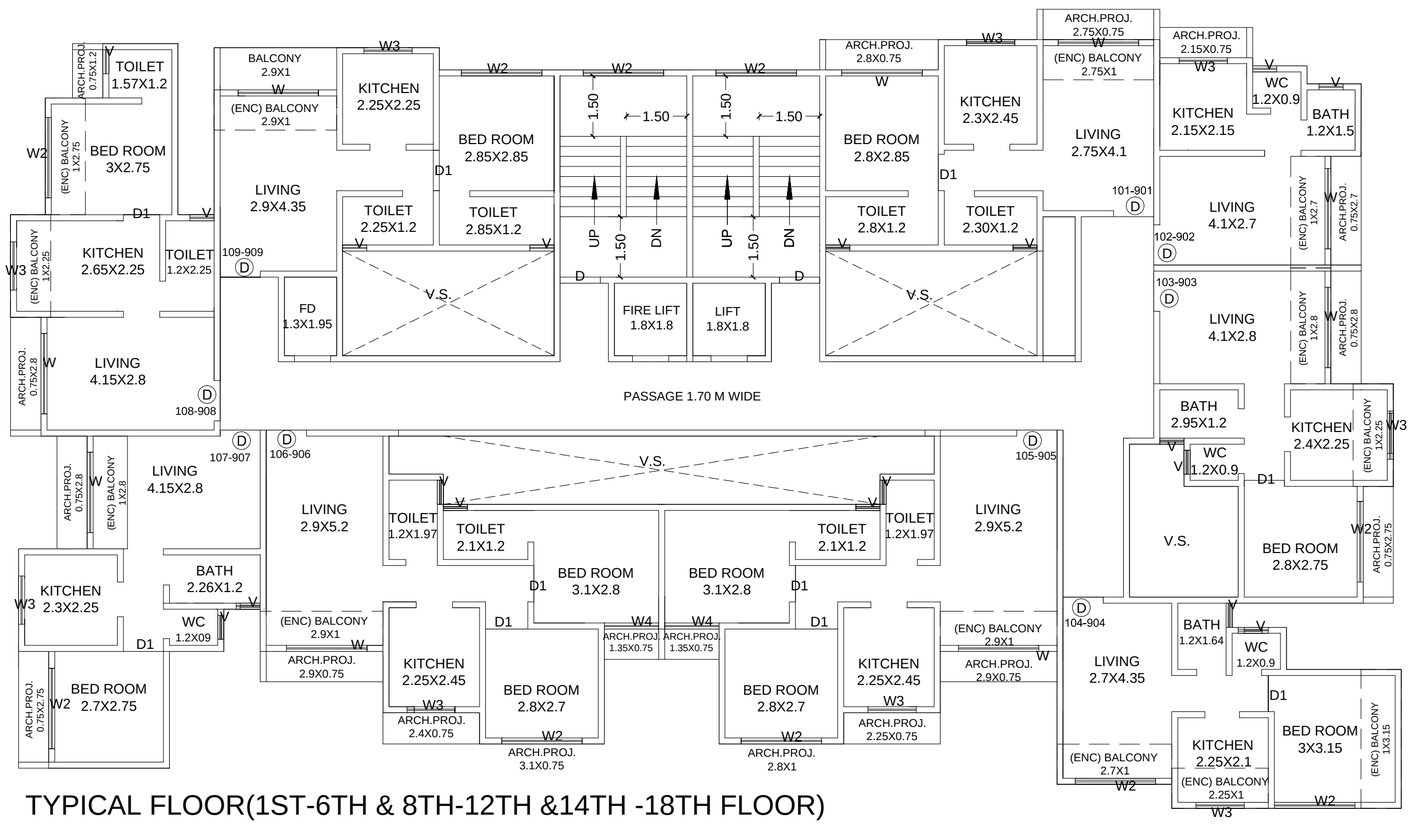


## TYPICAL FLOOR(1ST-6TH & 8TH-12TH &14TH -18TH FLOOR)

SCALE 1:100

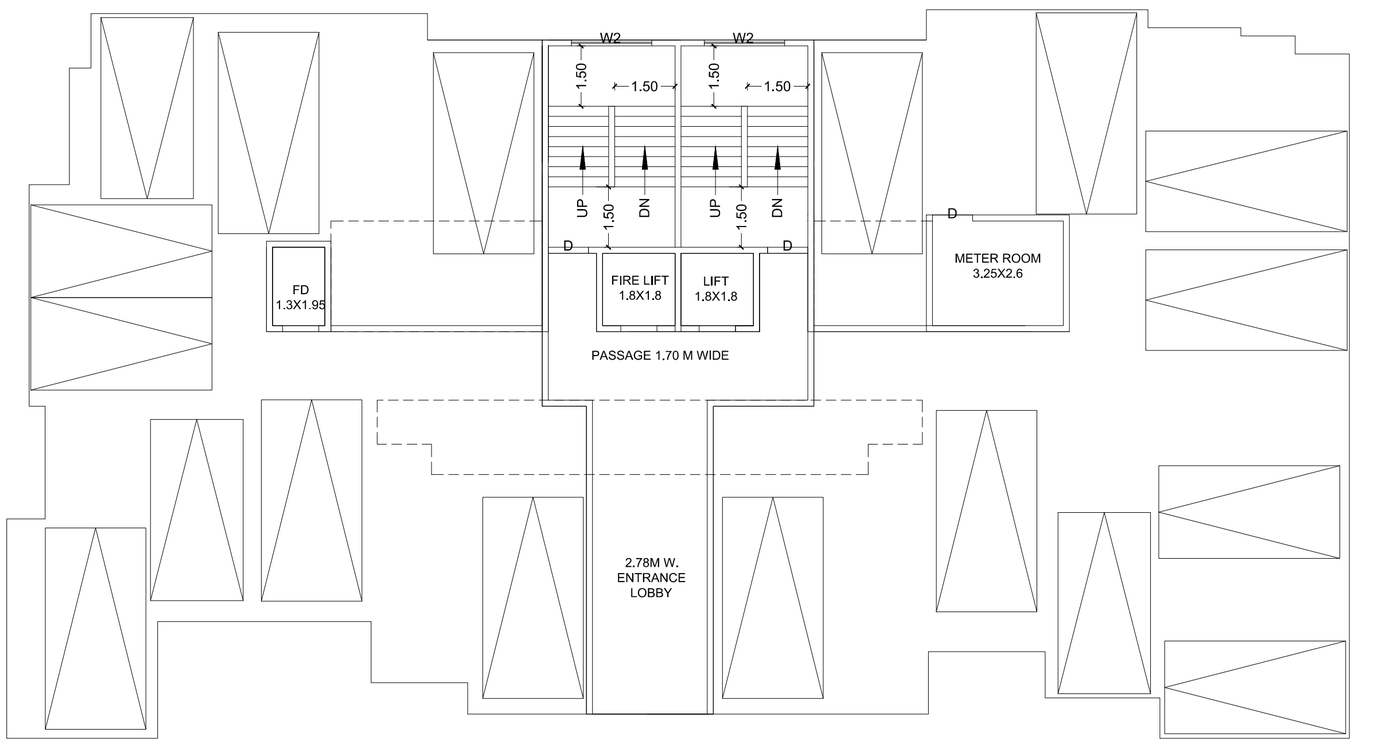


## GROUND FLOOR

SCALE 1:100