BUILDING	FLOORS	COMM.	RESI.	FSI AREA IMD.	EDU.	INS.	MUZZ.	TYPE A BALCONY	TERRACE	LIFT	LIFTWELL	DUCT	VENT SHAFT	OTHER DEDUCTION	TOTAL FSI AREA
TYPE A	TERRACE FLOOR	0.000	12.365	0.000	0.000	0.000	0.000	0.000	0.000	0.000	0.000	0.000	0.000	0.000	12.365
TYPE A	7TH 12TH 17TH	0.000	1137.165	0.000	0.000	0.000	0.000	16.510	0.000	0.000	0.000	26.400	0.000	174.969	925.196
TYPE A	8TH TO 11TH 13TH TO 16TH 18TH TO 20TH FLOOR	0.000	3382.695	0.000	0.000	0.000	0.000	27.450	0.000	0.000	79.200	0.000	0.000	129.222	3174.273
TYPE A	6TH TO 5TH 4TH FLOOR	0.000	1525.612	0.000	0.000	0.000	0.000	36.600	0.000	0.000	26.200	0.000	0.000	57.432	1427.580
TYPE A	3RD FLOOR	0.000	473.600	0.000	0.000	0.000	0.000	0.000	0.000	0.000	14.800	0.000	0.000	14.208	458.592
TYPE A	2ND FLOOR	40.500	0.000	0.000	0.000	0.000	0.000	23.000	0.000	0.000	64.000	0.000	0.000	87.000	240.500
TYPE A	1ST FLOOR	430.501	0.000	0.000	0.000	0.000	0.000	0.000	0.000	0.000	14.200	0.000	0.000	10.579	405.701
TYPE A	GROUND FLOOR	142.955	195.375	0.000	0.000	0.000	0.000	0.000	0.000	14.200	0.000	0.000	0.000	2.451	356.880
TYPE A	TOTAL	1022.468	6575.500	0.000	0.000	0.000	0.000	117.659	0.000	14.200	178.120	0.000	0.000	399.942	7029.906

BUILDING	FLOORS	COMM.	RESI.	FSI AREA IMD.	EDU.	INS.	MUZZ.	TYPE B BALCONY	TERRACE	LIFT	LIFTWELL	DUCT	VENT SHAFT	OTHER DEDUCTION	TOTAL FSI AREA
TYPE B	7TH 12TH 17TH FLOOR	0.000	1048.540	0.000	0.000	0.000	0.000	40.075	0.000	0.000	38.400	86.091	0.000	220.324	1582.730
TYPE B	8TH 9TH 10 11TH 13TH 14TH 15TH 16TH 18TH 19TH 20TH FLOOR	0.000	6198.180	0.000	0.000	0.000	0.000	221.150	0.000	0.000	153.600	344.364	0.000	95.676	5664.540
TYPE B	5TH FLOOR	0.000	523.269	0.000	0.000	0.000	0.000	24.665	0.000	0.000	12.800	28.697	0.000	7.973	473.795
TYPE B	4TH FLOOR	0.000	528.540	0.000	0.000	0.000	0.000	24.663	0.000	0.000	12.800	28.697	0.000	7.973	477.170
TYPE B	3RD FLOOR	0.000	528.540	0.000	0.000	0.000	0.000	24.663	0.000	0.000	12.800	28.697	0.000	7.973	477.170
TYPE B	2ND FLOOR	398.132	0.000	0.000	0.000	0.000	0.000	35.825	0.000	0.000	14.200	0.000	0.000	18.750	359.782
TYPE B	1ST FLOOR	539.400	0.000	0.000	0.000	0.000	0.000	6.650	0.000	0.000	18.200	0.000	0.000	18.750	522.440
TYPE B	GROUND FLOOR	251.423	190.263	0.000	0.000	0.000	0.000	0.000	0.000	18.200	0.000	0.000	0.000	8.610	425.036
TYPE B	TOTAL	1627.955	9494.428	0.000	0.000	0.000	0.000	360.441	0.000	18.200	268.920	516.546	0.000	365.929	9732.579

FSI DETAILS

Sl.	Index	Basic FSI (on serial no 7)	Premium FSI (on serial no 3)	TDR/DR (on serial no 3)	Permissible for full green building if Applicable (on serial no 7.4)	Ancillary Area(65% of 2 + 3+4+5)	Ancillary Area(65% of 2 + 3+4+5)	Total	Drawing Value
10.1 Permissible Index		1.100	0.000	1.900	50%	0.000	0.000	3.000	0.000
10.2 Total Entitlement of FSI as per 7.0 + 7.1 + 7.2 + 7.3		1.100	0.000	1.900	0.500	0.000	0.000	3.000	0.000
10.3 FSI Permissible in Redevelopment(Sec 40 10.1 and 10.2)		1.100	0.000	1.900	0.500	0.000	0.000	3.000	0.000
10.4 Total Consumed Index		0.000	0.000	0.000	0.000	0.000	0.000	0.000	-
10.5 Balance Index Available(10.3 - 10.4)		1.100	0.000	1.900	0.500	0.000	0.000	3.000	-
10.6 Total Permissible F.Loor Area		3495.800	0.000	6038.200	0.001	0.000	5451.296	15029.365	16014.658	0.000
10.7 Proposed F.Loor Area (Afford not exceed 10.4)		3495.800	0.000	5923.000	0.001	0.000	5451.296	15029.296	15899.365	16014.296
10.8 Total Consumed		1.100	0.577	1.296	0.500	0.000	0.000	0.000	2.964	0.000

Carpet Area Table

Building Name	Floor Name	Carpet name	Tenement No	Carpet Area	Enclosed balcony Area(Ac/Nac)	Normal Balcony Area(Ac/Nac)	Wesspace Area	Total Carpet Area
TYPE A	GROUND FLOOR	1	1	14.261	0.000	0.000	0.000	14.261
TYPE A	GROUND FLOOR	2	1	19.088	0.000	0.000	0.000	19.088
TYPE A	GROUND FLOOR	3	1	20.134	0.000	0.000	0.000	20.134
TYPE A	GROUND FLOOR	4	1	25.080	0.000	0.000	0.000	25.080
TYPE A	GROUND FLOOR	5	1	18.057	0.000	0.000	0.000	18.057
TYPE A	1ST FLOOR	1	1	81.573	0.000	0.000	0.000	81.573
TYPE A	1ST FLOOR	2	1	62.883	0.000	0.000	0.000	62.883
TYPE A	1ST FLOOR	3	1	52.863	0.000	0.000	0.000	52.863
TYPE A	1ST FLOOR	4	1	64.538	0.000	0.000	0.000	64.538
TYPE A	2ND FLOOR	1	1	82.590	3.000	0.000	0.000	85.590
TYPE A	2ND FLOOR	2	1	63.960	4.500	0.000	0.000	70.560
TYPE A	2ND FLOOR	3	1	73.535	12.762	0.000	0.000	86.297
TYPE A	2ND FLOOR	4	1	65.530	2.887	0.000	0.000	68.417
TYPE A	3RD FLOOR	1	1	82.590	3.000	0.000	0.000	85.590
TYPE A	3RD FLOOR	2	1	46.530	4.170	0.000	0.000	50.700
TYPE A	3RD FLOOR	3	1	51.370	0.000	0.000	0.000	51.370
TYPE A	3RD FLOOR	4	1	56.548	0.000	0.000	0.000	56.548
TYPE A	3RD FLOOR	5	1	47.942	3.000	0.000	0.000	50.992
TYPE A	4TH TO 6TH 8TH	1	4	41.903	0.000	0.000	0.000	41.903
TYPE A	4TH TO 6TH 8TH FLOOR	2	4	48.530	6.170	0.000	0.000	54.700
TYPE A	4TH TO 6TH 8TH FLOOR	3	4	51.370	0.000	0.000	0.000	51.370
TYPE A	4TH TO 6TH 8TH FLOOR	4	4	56.548	0.000	0.000	0.000	56.548
TYPE A	4TH TO 6TH 8TH FLOOR	5	4	47.942	3.050	0.000	0.000	50.992
TYPE A	9TH TO 11TH 13TH TO 16TH 18TH FLOOR	1	9	37.200	0.000	0.000	0.000	37.200
TYPE A	9TH TO 11TH 13TH TO 16TH 18TH FLOOR	2	9	48.530	0.000	0.000	0.000	48.530
TYPE A	9TH TO 11TH 13TH TO 16TH 18TH FLOOR	3	9	51.370	0.000	0.000	0.000	51.370
TYPE A	9TH TO 11TH 13TH TO 16TH 18TH FLOOR	4	9	56.548	0.000	0.000	0.000	56.548
TYPE A	9TH TO 11TH 13TH TO 16TH 18TH FLOOR	5	9	47.942	3.050	0.000	0.000	50.992
TYPE A	7TH 12TH 17TH	1	3	37.200	0.000	0.000	0.000	37.200
TYPE A	7TH 12TH 17TH	2	3	48.530	6.170	0.000	0.000	54.700
TYPE A	7TH 12TH 17TH	3	3	51.370	0.000	0.000	0.000	51.370
TYPE A	7TH 12TH 17TH	4	3	67.079	0.000	0.000	0.000	67.079

Carpet Area Table

Building Name	Floor Name	Carpet name	Tenement No	Carpet Area	Enclosed balcony Area(Ac/Nac)	Normal Balcony Area(Ac/Nac)	Wesspace Area	Total Carpet Area
TYPE B	GROUND FLOOR	1	1	59.933	0.000	0.000	0.000	59.933
TYPE B	GROUND FLOOR	2	1	22.775	0.000	0.000	0.000	22.775
TYPE B	GROUND FLOOR	3	1	9.408	0.000	0.000	0.000	9.408
TYPE B	GROUND FLOOR	4	1	17.825	0.000	0.000	0.000	17.825
TYPE B	GROUND FLOOR	5	1	19.673	0.000	0.000	0.000	19.673
TYPE B	GROUND FLOOR	6	1	22.000	0.000	0.000	0.000	22.000
TYPE B	GROUND FLOOR	7	1	19.673	0.000	0.000	0.000	19.673
TYPE B	GROUND FLOOR	8	1	23.045	0.000	0.000	0.000	23.045
TYPE B	1ST FLOOR	1	1	67.453	0.000	0.000	0.000	67.453
TYPE B	1ST FLOOR	2	1	48.638	0.000	0.000	0.000	48.638
TYPE B	1ST FLOOR	3	1	71.505	0.000	0.000	0.000	71.505
TYPE B	1ST FLOOR	4	1	64.797	0.000	0.000	0.000	64.797
TYPE B	1ST FLOOR	5	1	102.457	6.650	0.000	0.000	109.107
TYPE B	2ND FLOOR	1	1	68.545	7.250	0.000	0.000	75.795
TYPE B	2ND FLOOR	2	1	48.745	7.350	0.000	0.000	57.095
TYPE B	2ND FLOOR	3	1	71.505	7.350	0.000	0.000	78.855
TYPE B	2ND FLOOR	4	1	69.532	11.625	0.000	0.000	81.157
TYPE B	2ND FLOOR	5	1	102.840	10.200	0.000	0.000	113.190
TYPE B	3RD FLOOR	1	1	86.500	0.000	4.225	0.000	90.725
TYPE B	3RD FLOOR	2	1	58.128	3.400	0.000	0.000	62.528
TYPE B	3RD FLOOR	3	1	69.330	3.400	0.000	0.000	72.730
TYPE B	4TH FLOOR	1	1	82.018	4.000	0.000	0.000	86.018
TYPE B	4TH FLOOR	2	1	58.128	3.400	0.000	0.000	62.528
TYPE B	4TH FLOOR	3	1	69.330	3.400	0.000	0.000	72.730
TYPE B	4TH FLOOR	4	1	71.826	3.400	0.000	0.000	75.226
TYPE B	5TH FLOOR	1	1	82.018	4.000	0.000	0.000	86.018
TYPE B	5TH FLOOR	2	1	58.127	3.400	0.000	0.000	62.527
TYPE B	5TH FLOOR	3	1	86.920	0.000	4.225	0.000	86.920
TYPE B	5TH FLOOR	4	1	58.128	3.400	0.000	0.000	62.528
TYPE B	5TH FLOOR	5	1	69.790	3.400	6.458	0.000	73.190
TYPE B	6TH 7TH 8TH 9TH 10TH 11TH 13TH TO 16TH AND 18TH TO 20TH FLOOR	1	12	82.018	4.000	0.000	0.000	86.018
TYPE B	6TH 7TH 8TH 9TH 10TH 11TH 13TH TO 16TH AND 18TH TO 20TH FLOOR	2	12	58.128	3.400	0.000	0.000	62.528
TYPE B	6TH 7TH 8TH 9TH 10TH 11TH 13TH TO 16TH AND 18TH TO 20TH FLOOR	3	12	86.920	0.000	4.225	0.000	86.920
TYPE B	6TH 7TH 8TH 9TH 10TH 11TH 13TH TO 16TH AND 18TH TO 20TH FLOOR	4	12	58.128	3.400	0.000	0.000	62.528
TYPE B	6TH 7TH 8TH 9TH 10TH 11TH 13TH TO 16TH AND 18TH TO 20TH FLOOR	5	12	69.330	3.400	0.000	0.000	72.730
TYPE B	7TH 12TH 17TH FLOOR	1	3	82.018	4.000	0.000	0.000	86.018
TYPE B	7TH 12TH 17TH FLOOR	2	3	86.920	0.000	4.225	0.000	86.920
TYPE B	7TH 12TH 17TH FLOOR	3	3	58.128	3.400	0.000	0.000	62.528
TYPE B	7TH 12TH 17TH FLOOR	4	3	69.330	3.400	0.000	0.000	72.730

Area Utilisation of Roads and Reservations

Description of area utilisation						
Sl.No.(Only)	Reservation type	Reservation no	Authorised Area Quantum of DP/TDR Issued	Quantum of DP/TDR generation	Total Quantum of DP/TDR generation	Area considered for DP utilisation	Remaining area for DPC generation
	-		30.000 m DP Road Widening	12.000	24.000	24.000	0.000	0.000
	-		9.00m DP Road Widening	480.000	960.000	960.000	0.000	0.000
			Total	492.000	984.000	984.000	0.000	984.000

Parking Check (Table 6B)

Building Name	USE	TENAMENT AREA	Required car	Required scooter	NO.OF Tons/AreaUnits	car	scooter	Transport Vans/Autos/Buses Mini Bus
TYPE A	Residential	For areas two tenements with each tenement having carpet area equal to or above 40 sq.m but less than 80 sq.m.	1	2	66	33.000	66.000	-
TYPE A	Residential	For areas two tenements with each tenement having carpet area equal to or above 80 sq.m but less than 40 Sq.m. but more than 30 sq.m.	1	2	13	6.500	13.000	-
TYPE A	Commercial	For every 100 sq.m. of Floor area (Action thereof	2	6	96.621	1.932	5.797	-
TYPE A	Commercial	For every 200 sq.m. of Floor area (Action thereof	3	11	552.471	8.287	33.386	1.000
TYPE B	Residential	For areas two tenements with each tenement having carpet area equal to or above 40 sq.m but less than 80 sq.m.	1	2	64	32.000	64.000	-
TYPE B	Residential	For areas two tenements having carpet area equal to or above 80 Sq.m. but less than 160 sq.m.	1	1	18	18.000	18.000	-
TYPE B	Commercial	For every 100 sq.m. of Floor area (Action thereof	2	6	192.792	3.856	11.568	-
TYPE B	Commercial	For every 200 sq.m. of Floor area (Action thereof	3	11	759.633	11.394	41.790	1.000
Total	-	-	-	-	-	114.970	233.539	2.000
Visitors parking(5%)	-	-	-	-	-	4.575	8.000	-
Total	-	-	-	-	-	119.445	258.580	2.000

Parking Check As Per Multiplying Factor 0.850 (note: 15 & ecnhr equals to 1 car, proposed compactly parking for car= 40)

Building Name	Required Car	Required Scooter	Required Vans/Autos/Buses Mini bus	Provided Car	Provided Scooter	Provided Vans/Autos/Buses Mini bus	Status
Total	136	0	2	150	31	0	OK

Building	Req. Size	Prop. Size	Status
TYPE A	3.000X3.400	3.050X3.400	OK
TYPE A	3.000X3.400	3.050X3.400	OK
TYPE B	3.000X3.400	3.050X3.400	OK
TYPE B	3.000X3.400	3.050X3.500	OK

SCHEDULE OF OPENING

Sl.No.	NAME	HEIGHT	Nos.
TYPE B	V	0.600	0.750	38
TYPE A	V	0.600	0.750	47

Existing Building/ Tenement Details

Sl.No.	Building/Tenement No	Carpet Area Per Tenement	Block Per Tenement	Name Of Occupant	Number Of Tenements	Residential/Non Residential	For Tenement Less than 30 Sq.m. STAIR Min 21 if Sqm is ha added	Total	Incentive 30%/50% per Tenement for owner	Total incentive	10 Sqm BUA addition per tenement	Total of 10 sqmt Addition	Total
0	0	30.000	35.000	Tenant	70	Residential	0.000	0.000	17.500	0.000	15.000	1050.000	3500.000

Owner Details

Owner Name	Owner Address	Contact Number
MIDAS CREATORS	302-Morya Apartment,Titak Chowk,Kalyan,Thane,Maharashtra-421	9664304464
PRANAV PRAKASH PENKAR	1st floor, Shared Complex, Oak Bagh , near kalyan station west, 421301	9664304464

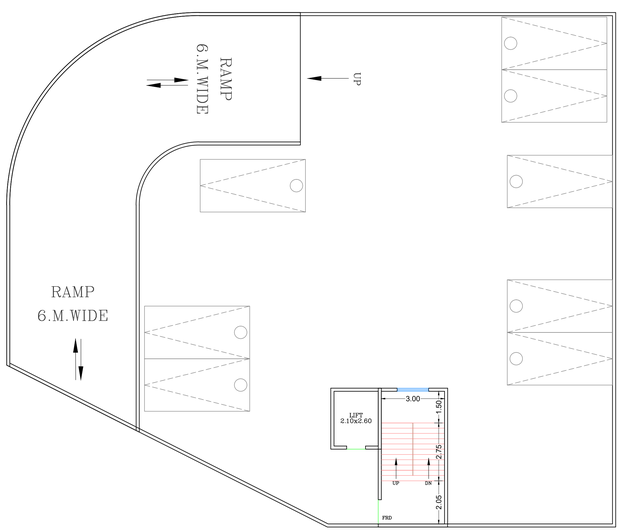

TYPE-A BASEMENT FLOOR PLAN

SCALE 1:100

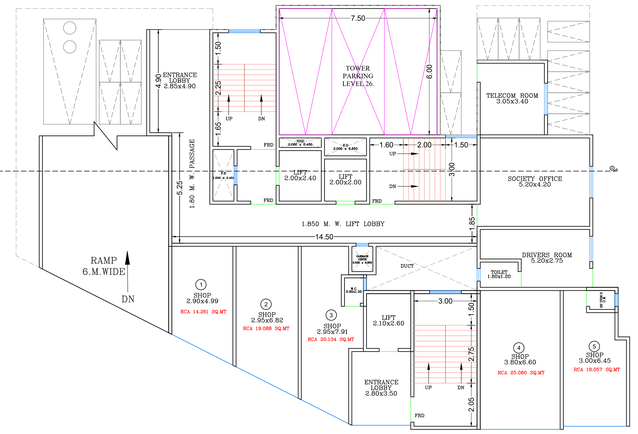

TYPE-A GROUND FLOOR PLAN

SCALE 1:100

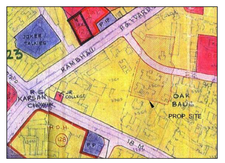

LOCATION PLAN

Project Details	
Proposal code: KDMCC-26-01792	
Zone Type: Residential Zone	
Location: Non-Congested	
Name of Action: Redevelopment For Dangerous Building	
Sub Name: Redevelopment of tenanted buildings	
CTS/Survey No.: 3360	
Taluka: section-1	
Village: KALYAN(PT)	
Private Value: 0.000	
Separation/OSZ Zone Area: -	

LEGENDS:
ALL DIMENSIONS IN MILLIMETERS
PROPOSED WORK SHOWN IN RED
EXISTING WORK TO BE REMOVED LIGHT
WATER LINE SHOWN IN BLUE SCITITED
SEWER LINE SHOWN IN BROWN
TERRACE WATERLINE SHOWN YELLOW
OPEN SAL SHOWN BROWN
EXISTING SHOWN BLUE HATCHED

LAYOUT PLAN | SHEET NO. 1/4

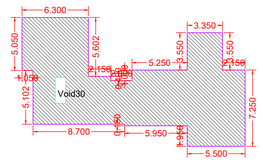

BUILT UP AREA CALCULATION FOR GROUND FLOOR AREA			
AREA NAME	LENGTH	WIDTH	AreaSq.Mt.
BLOCK	21.200	12.250	198.378
		BLOCK AREA TOTAL =198.378Sq.Mt	
void30	-	-	2.451
		TOTAL Deduction =2.451Sq.Mt	
		Net Builtup Area =195.927 Sq.Mt	

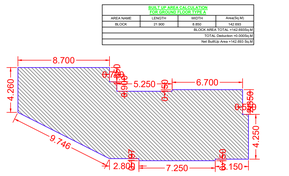

BUILT UP AREA CALCULATION FOR GROUND FLOOR AREA			
AREA NAME	LENGTH	WIDTH	AreaSq.Mt.
BLOCK	21.200	12.250	198.378
		BLOCK AREA TOTAL =198.378Sq.Mt	
void30	-	-	2.451
void31	-	-	1.750
void32	-	-	1.750
void33	-	-	0.400
void34	-	-	1.000
void35	-	-	4.000
void36	-	-	0.400
void37	-	-	2.451
void38	-	-	1.000
void39	-	-	4.328
void40	-	-	4.800
void41	-	-	0.400
void42	-	-	0.400
		TOTAL Deduction =25.855Sq.Mt	
		Net Builtup Area =169.523 Sq.Mt	

BUILT-UP AREA CALCULATION
GROUND FLOOR TYPE-A

SCALE 1:200

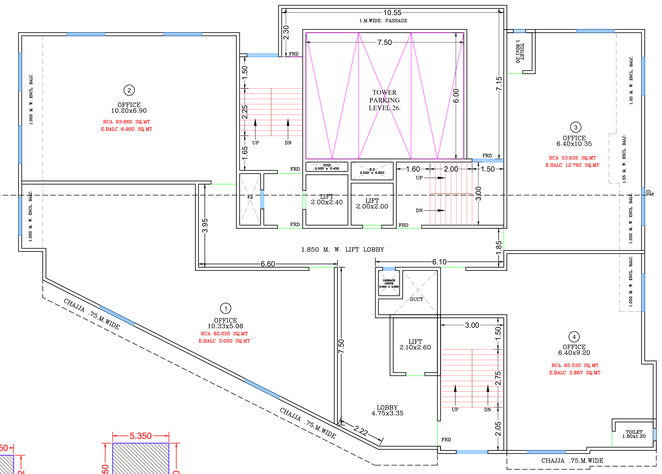

TYPE-A 2ND FLOOR PLAN

SCALE 1:100

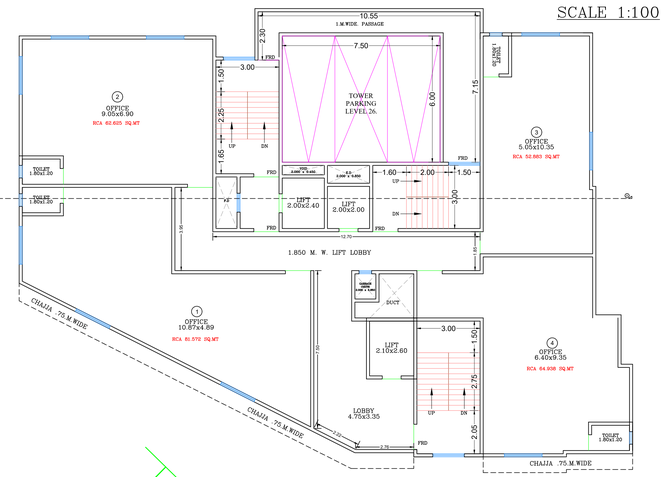

TYPE-A 1ST FLOOR PLAN

SCALE 1:100

BUILT UP AREA CALCULATION FOR 1ST FLOOR TYPE-A			
AREA NAME	LENGTH	WIDTH	AreaSq.Mt.
BLOCK	21.200	12.250	198.378
		BLOCK AREA TOTAL =198.378Sq.Mt	
void26	-	-	2.451
void27	-	-	1.750
void28	-	-	1.750
void29	-	-	0.400
void30	-	-	1.000
void31	-	-	4.000
void32	-	-	0.400
void33	-	-	0.400
void34	-	-	2.451
void35	-	-	1.000
void36	-	-	4.328
void37	-	-	4.800
void38	-	-	0.400
void39	-	-	0.400
void40	-	-	4.800
void41	-	-	0.400
void42	-	-	0.400
		TOTAL Deduction =29.855Sq.Mt	
		Net Builtup Area =168.523 Sq.Mt	

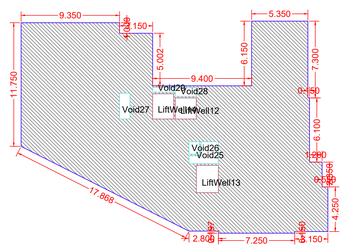

BUILT-UP AREA CALCULATION
1ST FLOOR TYPE-A

SCALE 1:200

BUILT UP AREA CALCULATION FOR 2ND FLOOR TYPE-A			
AREA NAME	LENGTH	WIDTH	AreaSq.Mt.
BLOCK	21.200	12.250	198.378
		BLOCK AREA TOTAL =198.378Sq.Mt	
void43	-	-	2.451
void44	-	-	1.750
void45	-	-	1.750
void46	-	-	0.400
void47	-	-	1.000
void48	-	-	4.000
void49	-	-	0.400
void50	-	-	0.400
void51	-	-	2.451
void52	-	-	1.000
void53	-	-	4.328
void54	-	-	4.800
void55	-	-	0.400
void56	-	-	0.400
void57	-	-	4.800
void58	-	-	0.400
void59	-	-	0.400
void60	-	-	2.451
void61	-	-	1.000
void62	-	-	4.000
void63	-	-	0.400
void64	-	-	0.400
void65	-	-	2.451
void66	-	-	1.000
void67	-	-	4.000
void68	-	-	0.400
void69	-	-	0.400
void70	-	-	2.451
void71	-	-	1.000
void72	-	-	4.000
void73	-	-	0.400
void74	-	-	0.400
void75	-	-	2.451
void76	-	-	1.000
void77	-	-	4.000
void78	-	-	0.400
void79	-	-	0.400
void80	-	-	2.451
void81	-	-	1.000
void82	-	-	4.000
void83	-	-	0.400
void84	-	-	0.400
void85	-	-	2.451
void86	-	-	1.000
void87	-	-	4.000
void88	-	-	0.400
void89	-	-	0.400
void90	-	-	2.451
void91	-	-	1.000
void92	-	-	4.000
void93	-	-	0.400
void94	-	-	0.400
void95	-	-	2.451
void96	-	-	1.000
void97	-	-	4.000
void98	-	-	0.400
void99	-	-	0.400
void100	-	-	2.451
void101	-	-	1.000
void102	-	-	4.000
void103	-	-	0.400
void104	-	-	0.400
void105	-	-	2.451
void106	-	-	1.000
void107	-	-	4.000
void108	-	-	0.400
void109	-	-	0.400
void110	-	-	2.451
void111	-	-	1.000
void112	-	-	4.000
void113	-	-	0.400
void114	-	-	0.400
void115	-	-	2.451
void116	-	-	1.000
void117	-	-	4.000
void118	-	-	0.400
void119	-	-	0.400
void120	-	-	2.451
void121	-	-	1.000
void122	-	-	4.000
void123	-	-	0.400
void124	-	-	0.400
void125	-	-	2.451
void126	-	-	1.000
void127	-	-	4.000
void128	-	-	0.400
void129	-	-	0.400
void130	-	-	2.451
void131	-	-	1.000
void132	-	-	4.000
void133	-	-	0.400
void134	-	-	0.400
void135	-	-	2.451
void136	-	-	1.000
void137	-	-	4.000
void138	-	-	0.400
void139	-	-	0.400
void140	-	-	2.451
void141	-	-	1.000
void142	-	-	4.000
void143	-	-	0.400
void144	-	-	0.400
void145	-	-	2.451
void146	-	-	1.000
void147	-	-	4.000
void148	-	-	0.400
void149	-	-	0.400
void150	-	-	2.451
void151	-	-	1.000
void152	-	-	4.000
void153	-	-	0.400
void154	-	-	0.400
void155	-	-	2.451
void156	-	-	1.000
void157	-	-	4.000
void158	-	-	0.400
void159	-	-	0.400
void160	-	-	2.451
void161	-	-	1.000
void162	-	-	4.000
void163	-	-	0.400
void164	-	-	0.400
void165	-	-	2.451
void166	-	-	1.000
void167	-	-	4.000
void168	-	-	0.400
void169	-	-	0.400
void215	-	-	2.451
void216	-	-	1.000
void217	-	-	4.000
void218	-	-	0.400
void219	-	-	0.400
void220	-	-	2.451
void221	-	-	1.000
void222	-	-	4.000
void223	-	-	0.400
void224	-	-	0.400
void225	-	-	2.451
void226	-	-	1.000
void227	-	-	4.000
void228	-	-	0.400
void229	-	-	0.400
void230	-	-	2.451
void231	-	-	1.000
void232	-	-	4.000
void233	-	-	0.400
void234	-	-	0.400
void235	-	-	2.451
void236	-	-	1.000
void237	-	-	4.000
void238	-	-	0.400
void239	-	-	0.400
void240	-	-	2.451
void241	-	-	1.000
void242	-	-	4.000
void243	-	-	0.400

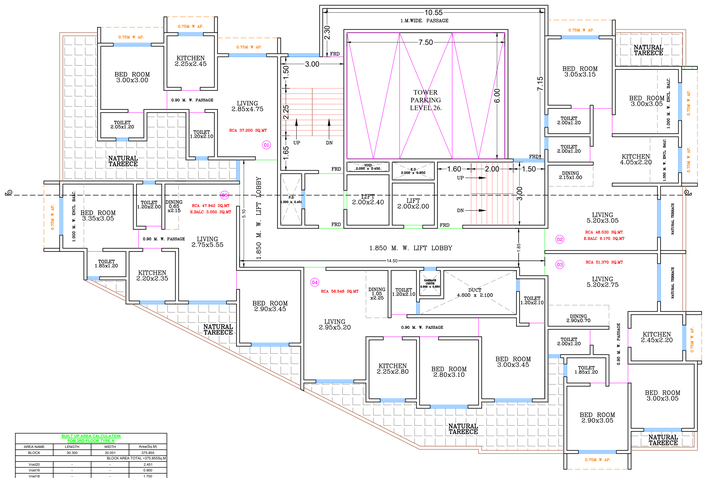

BUILT UP AREA CALCULATION
FOR 3RD FLOOR TYPE A

AREA NAME	LENGTH	WIDTH	Area(Sq.M)
BLOCK	30.300	20.001	374.492
		BLOCK AREA TOTAL =374.492Sq.M	
Void10	-	-	2.401
Void18	-	-	2.900
Void20	-	-	1.700
Void17	-	-	1.200
Void16	-	-	8.107
LiftWell6	-	-	4.800
LiftWell7	-	-	4.800
		TOTAL Deduction =23.108Sq.M	
		Net Builtup Area =351.384 Sq.M	

TYPE–A 3RD FLOOR PLAN
SCALE 1:100

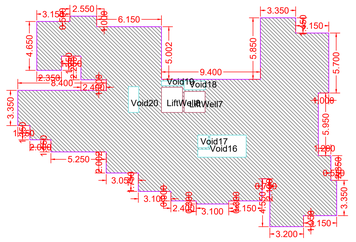

BUILT–UP AREA CALCULATION 3RD FLOOR TYPE–A
SCALE 1:200

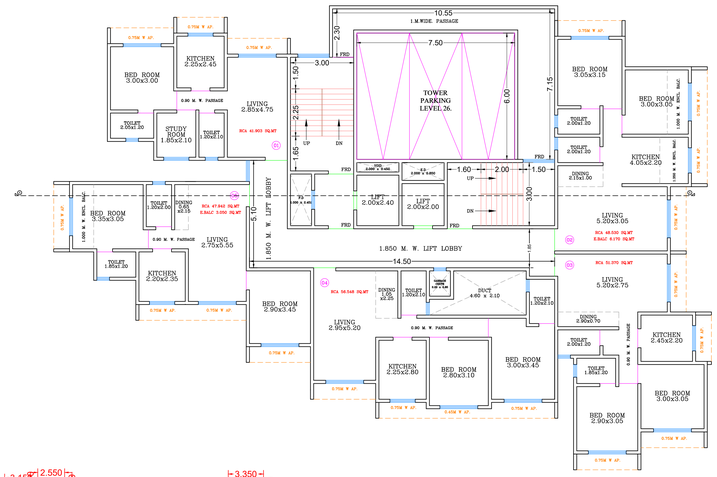

TYPE–A 4TH TO 6TH & 8TH FLOOR PLAN
SCALE 1:100

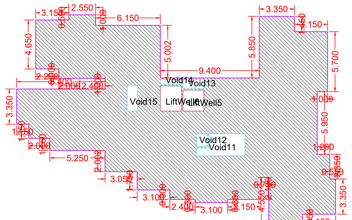

BUILT UP AREA CALCULATION
FOR 4TH TO 6TH & 8TH FLOOR TYPE A

AREA NAME	LENGTH	WIDTH	Area(Sq.M)
BLOCK	30.300	20.001	365.153
		BLOCK AREA TOTAL =365.153Sq.M	
Void16	-	-	2.401
Void13	-	-	9.900
Void15	-	-	4.800
Void12	-	-	1.200
Void11	-	-	8.107
LiftWell5	-	-	4.800
LiftWell3	-	-	4.800
		TOTAL Deduction =35.908Sq.M	
		Net Builtup Area =329.245 Sq.M	

BUILT–UP AREA CALCULATION 4TH TO 6TH & 8TH FLOOR TYPE–A
SCALE 1:200

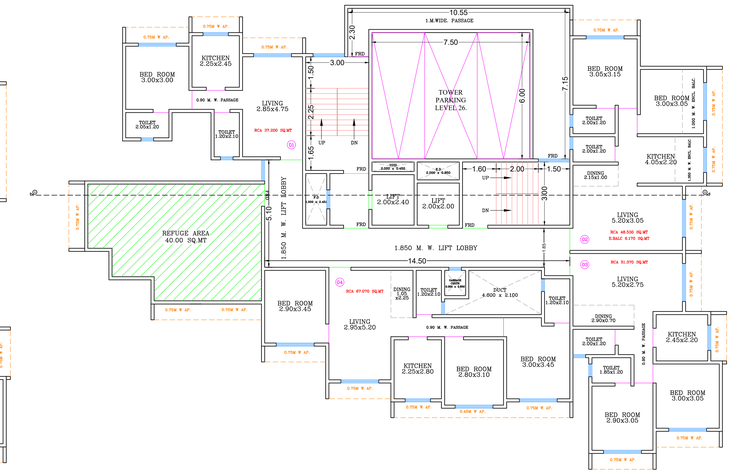

TYPE–A 7TH 12TH & 17TH FLOOR PLAN
SCALE 1:100

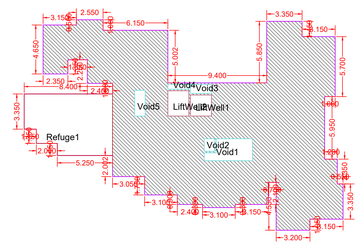

BUILT UP AREA CALCULATION
FOR 7TH 12TH & 17TH FLOOR TYPE A

AREA NAME	LENGTH	WIDTH	Area(Sq.M)
BLOCK	30.300	20.001	374.492
		BLOCK AREA TOTAL =374.492Sq.M	
Refuge1	-	-	42.880
Void5	-	-	2.401
Void4	-	-	9.900
Void3	-	-	1.700
Void2	-	-	1.200
Void1	-	-	8.107
LiftWell1	-	-	4.800
LiftWell2	-	-	4.800
		TOTAL Deduction =65.588Sq.M	
		Net Builtup Area =308.732 Sq.M	

BUILT–UP AREA CALCULATION 7TH 12TH & 17TH FLOOR TYPE–A
SCALE 1:200

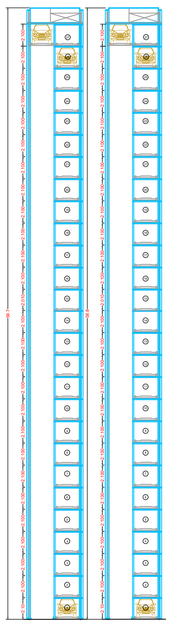

PARKING TOWER TYPE–A
SCALE 1:200

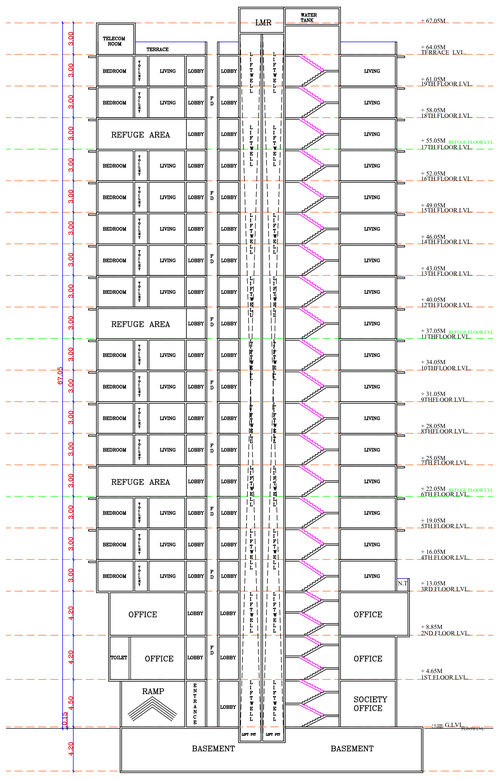

TYPE–A SECTION PLAN A–A
SCALE 1:200

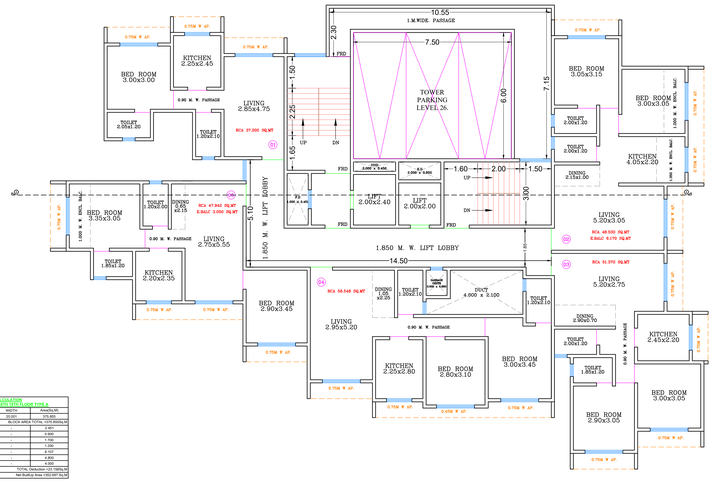

TYPE–A 9TH TO 11TH 13TH TO 16TH 18TH & 19 FLOOR PLAN
SCALE 1:100

BUILT UP AREA CALCULATION
FOR 9TH TO 11TH 13TH TO16TH 18TH 19TH FLOOR TYPE A

AREA NAME	LENGTH	WIDTH	Area(Sq.M)
BLOCK	30.300	20.001	365.153
		BLOCK AREA TOTAL =365.153Sq.M	
Void9	-	-	2.401
Void8	-	-	9.900
Void10	-	-	4.800
Void7	-	-	1.200
Void6	-	-	8.107
LiftWell3	-	-	4.800
LiftWell4	-	-	4.800
		TOTAL Deduction =35.908Sq.M	
		Net Builtup Area =329.245 Sq.M	

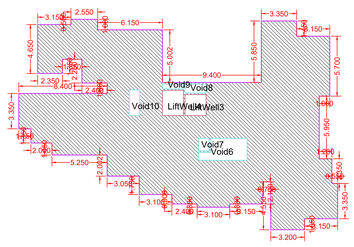

BUILT–UP AREA CALCULATION 9TH TO 11TH 13TH TO16TH 18TH 19TH FLOOR TYPE–A
SCALE 1:200

BUILT UP AREA CALCULATION
FOR TERRACE FLOOR TYPE A

AREA NAME	LENGTH	WIDTH	Area(Sq.M)
BLOCK	3.700	3.350	12.395
		BLOCK AREA TOTAL =12.395Sq.M	
		TOTAL Deduction =0.000Sq.M	
		Net Builtup Area =12.395 Sq.M	

BUILT–UP AREA CALCULATION TERRACE FLOOR TYPE–A
SCALE 1:200

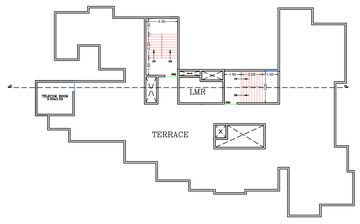

TYPE–A TERRACE FLOOR PLAN
SCALE 1:100

FLOOR PLAN TYPE A | SHEET NO. 2/4

Proforma I : Area Statement

1. Area of plot(Minimum area of a, b, c to be considered) or area of subplot with sanctioned layout No. and subplot No.	3670.000
(a) As per ownership document (7/12, CTS extract)	3670.000
(b) as per TILR or City Survey measurement sheet	3670.000
(c) as per Demarcated drawing area	3670.000
LESS	
2.Area not in possession	0.000
3. Area Proposed for development (out of 1-2)	3670.000
4.Deductions for(out of 3)	
(a) Proposed D.P./ D.P. Road widening Area/Proposed DP road, Road under MMC act	492.000
(b) Any D.P. Reservation area	0.000
(c) Green Belt	0.000
(Total a+b+c)	492.000
5. Balance area of plot (3-4)	3178.000
6. Amenity Space Proposed	0.000
(Required -(a) Upto 20,000 sqmt - Nil	-
(b) Above 20,000 and more - (a) + 5% of Total area	0.000
7. Net Plot Area (5-6)	3178.000
8.Recreational Open Space (Not applicable if plots are from sanctioned layout)	-
(a). If area is more than (5) 4000 sqmt - 10 % of (5) is required.	0.000
Proposed	0.000
(A)10 % Subject to minimum 200 sqmt(Not applicable if plots are from sanctioned layout or each plot admeuring less than 4000sq.m regularised under gunthewari act)	0.000
Proposed	0.000
(B)Exemption to leave open space subject to availing basic F.S.I. of 75 %	-
(C)Exemption to leave open space subject to payment of 10 % land value of land at (7) as per annual statement of rate.	-
If (5) > 4000sq.m then Land admeuring 20% of (5) is to be utilised for inclusive housing	0.000
Proposed Area	0.000
Architect/ Licensed Engineer/ Supervisor name and signature	

Registration No. of Architect/ License no. of Licensed Engineer/ Supervisor: CA/2019/106930

AMBER CO-OP.H.SCOCIETY & G.H.KOLTE & OTHERS.
POA M/S MIDAS CREATORS.
THROUGH MR.PRANAV PRAKASH PENKAR
Postal Address : 302-Morya Apartment,Tilak Chowk,Kalyan,Thane,Maharashtra-421301,1st floor, Sharad Complex, Oak Bagh , near kalyan station west, 421301

DESCRIPTION OF PROJECT :

Type of Proposal : Mixed
BUILDING ON CTS. NO. 3360,3361,3362,3363, AT. KALYAN, TAL-KALYAN, DIST-THANE

SITE ADDRESS :
CTS NO. 3360,3361,3362,3363, AT. KALYAN, TAL-KALYAN, DIST-THANE

Name Of Architect : Tejas Anil Nirgude

LOGO	ADDRESS OF OFFICE
	OFFICE - 5TH FLOOR, MIDTOWN EMBASSY, BEHIND VASANT VALLEY BUS DEPOT, OPP. NARAYANA SCHOOL, GANDHARE, KALYAN - 421301

OWNERS SIGN -	TECHNICAL PERSON SIGN
	TEJAS ANIL NIRGUDE Digitally signed by TEJAS ANIL NIRGUDE Date: 2026.01.20 17:46:49 +05'30'
SCALE -	DATE: Date: 20/01/26
JOB NO - KDMCC-26-01792	CHECK BY - ANIL

SUBMISSION DRAWING

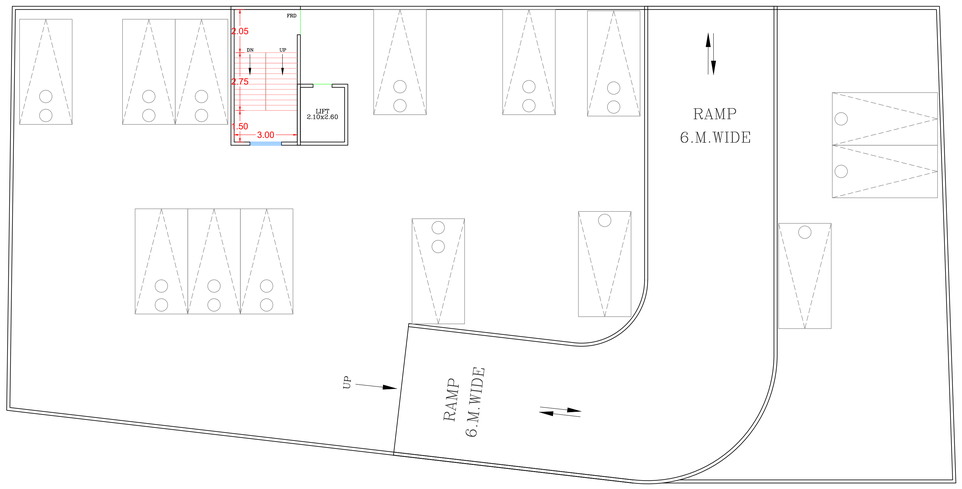

TYPE–B BASEMENT FLOOR PLAN
SCALE 1:100

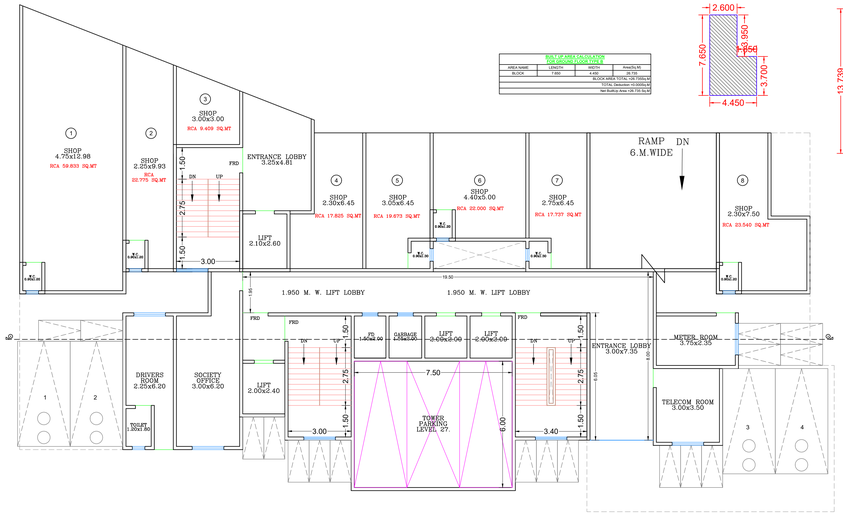

AREA NAME	LENGTH	WIDTH	Area(Sq.M)
BLOCK	2.600	10.700	27.820
		BLOCK AREA TOTAL=27.820SQ.M	
		TOTAL Deduction=0.000SQ.M	
		Net Builtup Area=27.820 Sq.M	

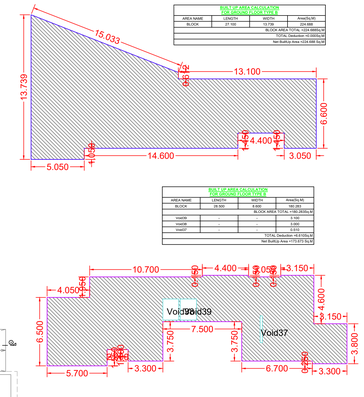

AREA NAME	LENGTH	WIDTH	Area(Sq.M)
BLOCK	39.700	19.200	762.240
		BLOCK AREA TOTAL=762.240SQ.M	
void1	-	-	1.950
void2	-	-	2.340
void3	-	-	3.510
void4	-	-	2.340
void5	-	-	2.340
void6	-	-	4.387
void7	-	-	1.463
void8	-	-	1.463
void9	-	-	3.510
void10	-	-	4.387
void11	-	-	1.463
void12	-	-	1.463
void13	-	-	3.510
void934	-	-	4.387
void935	-	-	1.463
void936	-	-	1.463
void937	-	-

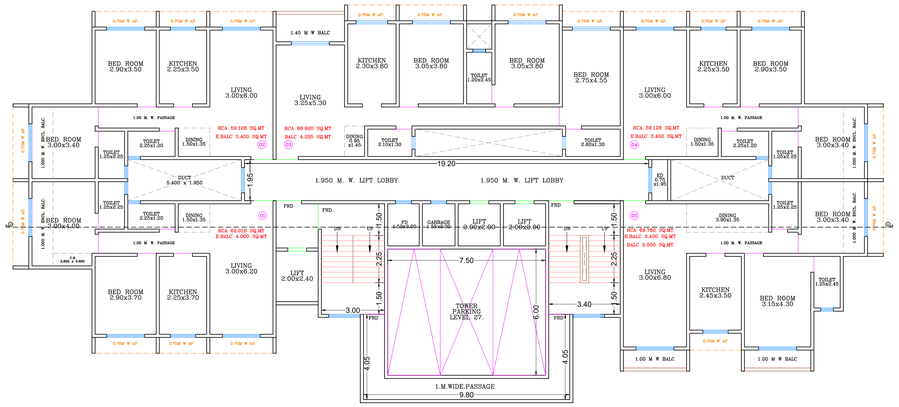

TYPE-B 5TH FLOOR PLAN

SCALE 1:100

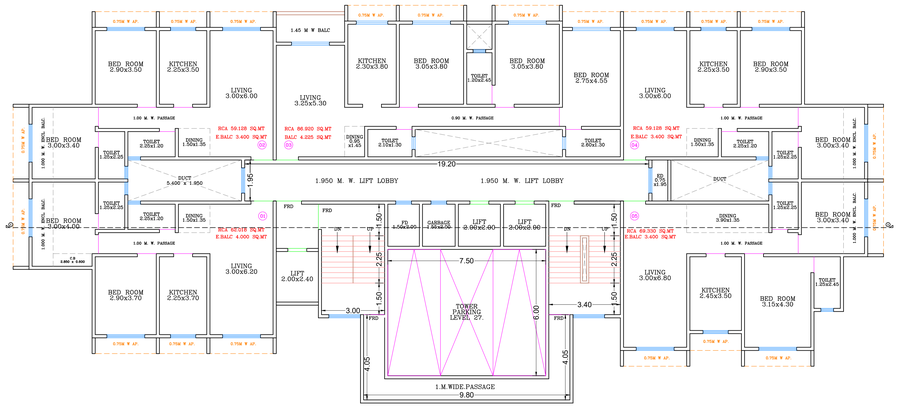

TYPE-B 6TH 8TH TO 11 13 TO 16 & 18TH 20TH FLOOR PLAN

SCALE 1:100

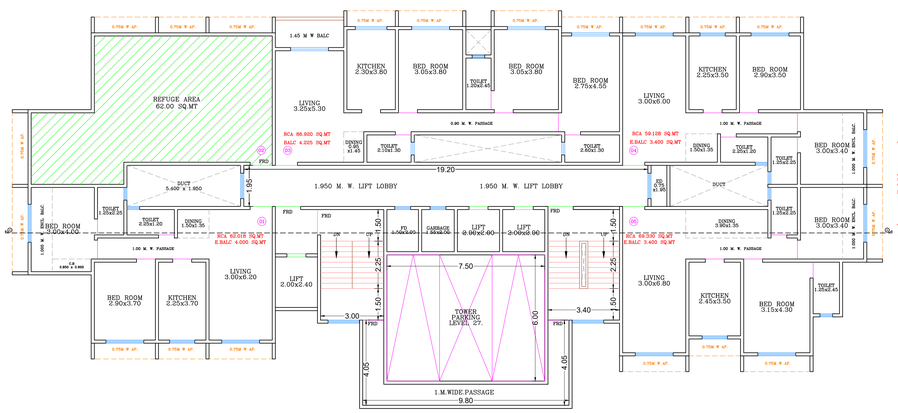

TYPE-B 7TH 12TH 17TH FLOOR PLAN

SCALE 1:100

BUILT UP AREA CALCULATION
FOR STILT FLOOR TYPE-B

AREA NAME	LENGTH	WIDTH	Area(SQ.M)
BLOCK	39.800	15.100	533.205
		BLOCK AREA TOTAL =539.315SQ.M	
Void11	-	-	3.000
Void12	-	-	3.100
Void13	-	-	1.463
Void8	-	-	0.410
LiftWell8	-	-	4.800
LiftWell9	-	-	4.800
LiftWell7	-	-	4.000
Duct8	-	-	10.530
Duct9	-	-	6.150
Duct7	-	-	3.067
TOTAL Deduction =44.319Sq.M			
Net Built Up Area=1471.18 Sq.M			

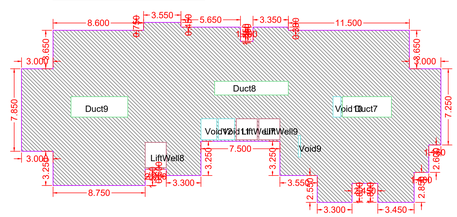

BUILT-UP AREA CALCULATION
5RD FLOOR TYPE-B

SCALE 1:200

BUILT UP AREA CALCULATION
FOR STILT FLOOR TYPE-B

AREA NAME	LENGTH	WIDTH	Area(SQ.M)
BLOCK	39.800	15.100	533.205
		BLOCK AREA TOTAL =539.315SQ.M	
Void6	-	-	3.000
Void7	-	-	3.100
Void8	-	-	1.463
Void9	-	-	0.410
LiftWell6	-	-	4.800
LiftWell7	-	-	4.800
LiftWell4	-	-	4.000
Duct6	-	-	10.530
Duct5	-	-	6.150
Duct4	-	-	3.067
TOTAL Deduction =44.319Sq.M			
Net Built Up Area =1471.18 Sq.M			

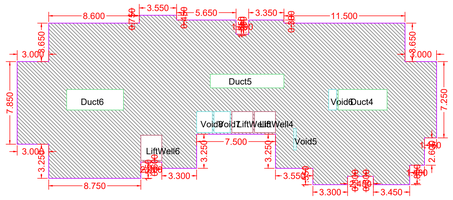

BUILT-UP AREA CALCULATION
6TH 8TH TO 11 13 TO 16
& 20TH FLOOR TYPE-B

SCALE 1:200

BUILT UP AREA CALCULATION
FOR STILT FLOOR TYPE-B

AREA NAME	LENGTH	WIDTH	Area(SQ.M)
BLOCK	39.800	15.100	533.205
		BLOCK AREA TOTAL =539.315SQ.M	
Refuge1	-	-	66.135
void4	-	-	3.000
void5	-	-	3.100
void6	-	-	1.463
void3	-	-	0.410
LiftWell3	-	-	4.800
LiftWell2	-	-	4.800
LiftWell1	-	-	4.000
Duct3	-	-	10.530
Duct2	-	-	6.150
Duct1	-	-	3.067
TOTAL Deduction =110.495Sq.M			
Net Built Up Area =428.819 Sq.M			

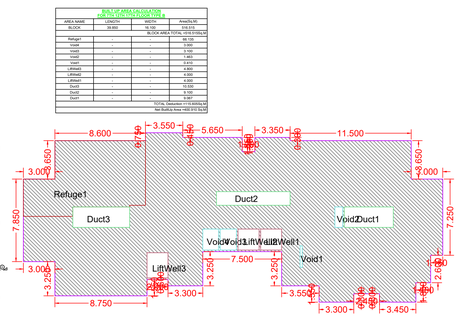

BUILT-UP AREA CALCULATION
7TH 12TH 17TH FLOOR TYPE-B

SCALE 1:200

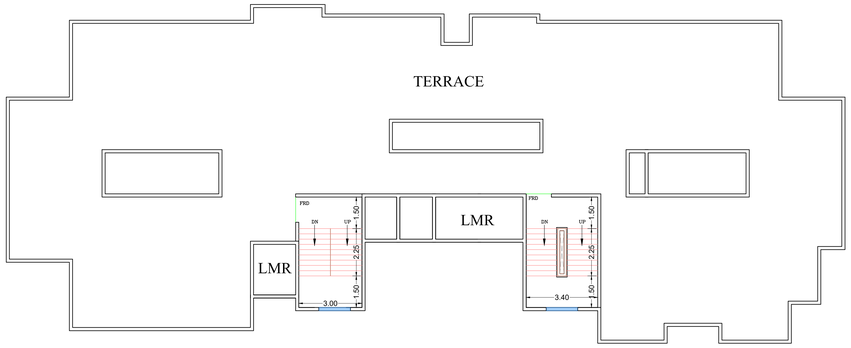

TERRACE FLOOR PLAN

SCALE 1:100

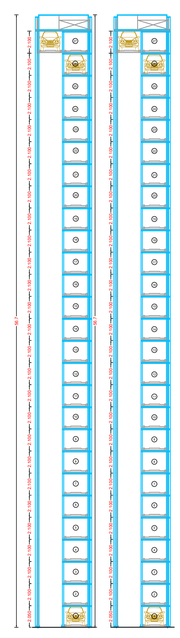

PARKING TOWER TYPE-B

SCALE 1:200

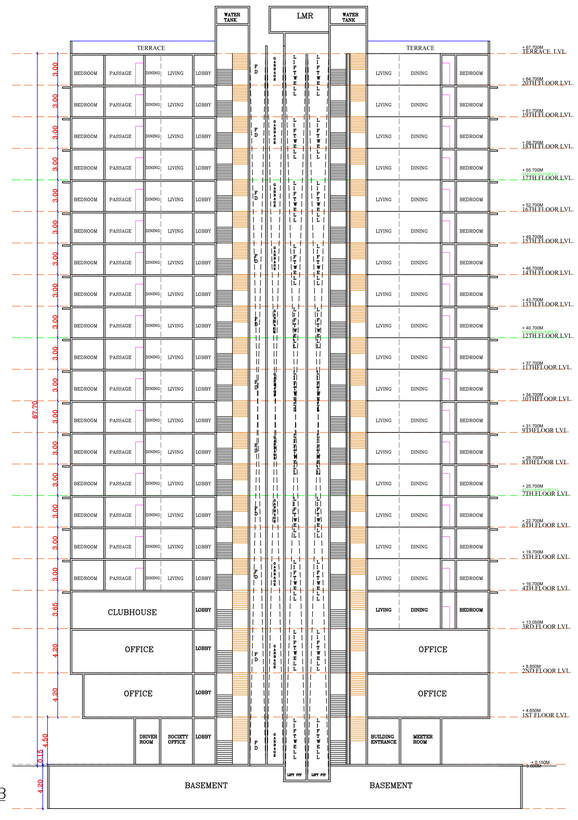

TYPE-B SECTION PLAN A-A

SCALE 1:200

FLOOR PLAN TYPE B | SHEET NO. 4/4

Proforma I : Area Statement

1. Area of plot(Minimum area of a, b, c to be considered) or area of subplot with sanctioned layout No. and subplot No.	3670.000
(a) As per ownership document (7/12, CTS extract)	3670.000
(b) as per TILR or City Survey measurement sheet	3670.000
(c) as per Demarcated drawing area	3670.000
LESS	
2.Area not in possession	0.000
3. Area Proposed for development (out of 1-2)	3670.000
4.Deductions for(out of 3)	
(a) Proposed D.P./ D.P. Road widening Area/Proposed DP road, Road under MMC act	492.000
(b) Any D.P. Reservation area	0.000
(c) Green Belt	0.000
Total a+b+c)	492.000
5. Balance area of plot (3-4)	3178.000
6. Amenity Space Proposed	0.000
(Required -(a) Upto 20,000 sqmt - Nil	-
(b) Above 20,000 and more - (a) + 5% of Total area	0.000
7. Net Plot Area (5-6)	3178.000
8.Recreational Open Space (Not applicable if plots are from sanctioned layout)	- -
(a). If area is more than (5) 4000 sqmt - 10 % of (5) is required.	0.000
Proposed	0.000
(A)10 % Subject to minimum 200 sqmt(Not applicable if plots are from sanctioned layout or each plot admesuring less than 4000sq.m regularised under gunthewari act)	0.000
Proposed	0.000
(B)Exemption to leave open space subject to availing basic F.S.I of 75 %	-
(C)Exemption to leave open space subject to payment of 10 % land value of land at (7) as per annual statement of rate.	-
If (5) > 4000sq m then Land admesuring 20% of (5) is to be utilised for inclusive housing	0.000
Proposed Area	0.000
Architect/ Licensed Engineer/ Supervisor name and signature	
Registration No. of Architect/ License no. of Licensed Engineer/ Supervisor: CA/2019/106930	

AMBER CO-OP.H.SCOCIETY & G.H.KOLTE & OTHERS.
POA,M/S MIDAS CREATORS.
THROUGH MR.PRANAV PRAKASH PENKAR
Postal Address : 302-Morya Apartment,Tilak Chowk,Kalyan,Thane,Maharashtra-421301,1st floor, Sharad Complex, Oak Bagh , near kalyan station west, 421301

DESCRIPTION OF PROJECT :

Type of Proposal : Mixed
BUILDING ON CTS. NO. 3360,3361,3362,3363, AT. KALYAN, TAL-KALYAN, DIST-THANE

SITE ADDRESS :
CTS NO. 3360,3361,3362,3363, AT. KALYAN, TAL-KALYAN, DIST-THANE

Name Of Architect : Tejas Anil Nirgude

LOGO	ADDRESS OF OFFICE
	OFFICE - 5TH FLOOR, MIDTOWN EMBASSY, BEHIND VASANT VALLEY BUS DEPOT, OPP. NARAYANA SCHOOL, GANDHARE, KALYAN - 421301

OWNERS SIGN -	TECHNICAL PERSON SIGN
	TEJAS ANIL NIRGUDE Digitally signed by TEJAS ANIL NIRGUDE Date: 2026.01.20 17:42:20 +05'30'

SCALE -	DATE: Date: 20/01/26
JOB NO - KDMCC-26-01792	CHECK BY - ANIL

SUBMISSION DRAWING