BUILT UP AREA CALCULATION

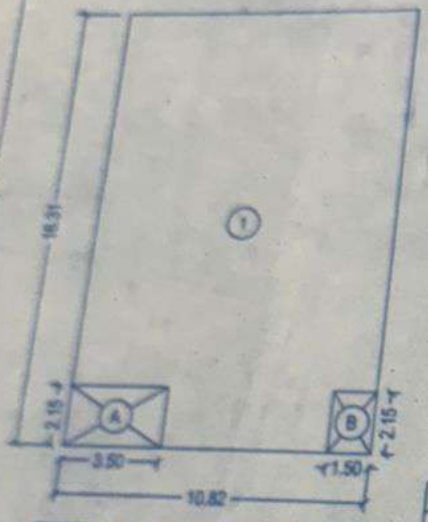

EXISTING AREA DIAGRAM FOR 1ST TO 2ND FLOOR

SCALE - 1:200

BUILT UP AREA CALCULATION

EXISTING TYP. 1ST & 2ND FL.			SQ.MT.
1	10.82 X16.31 X 1 NO	=	176.47
	TOTAL ADDITION	=	176.47

DEDUCTIONS

1	3.50 X 2.15 X 1 NO	=	7.53
2	1.50 X 2.15 X 1 NO	=	3.23
	TOTAL DEDUCTION	=	10.76
TOTAL BUILT UP AREA		=	165.71

BUILT UP AREA CALCULATION

EXISTING GROUND FLOOR			SQ.MT.
1	9.29 X 14.16 X 1 NO	=	131.55
	TOTAL ADDITION	=	131.55

DEDUCTIONS

A	2.59 X 5.17 X 1 NO	=	13.39
	TOTAL DEDUCTION	=	13.39
TOTAL BUILT UP AREA		=	118.33

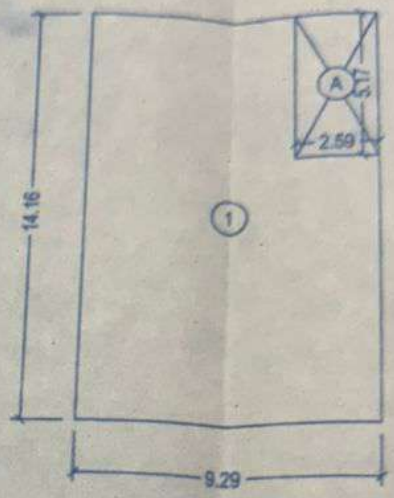

EXISTING AREA DIAGRAM FOR GROUND FLOOR

SCALE - 1:200

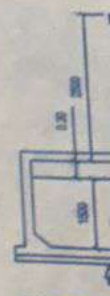

SECT. THR

SCALE 1:50

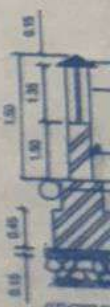

SECTIO

SCALE 1:5

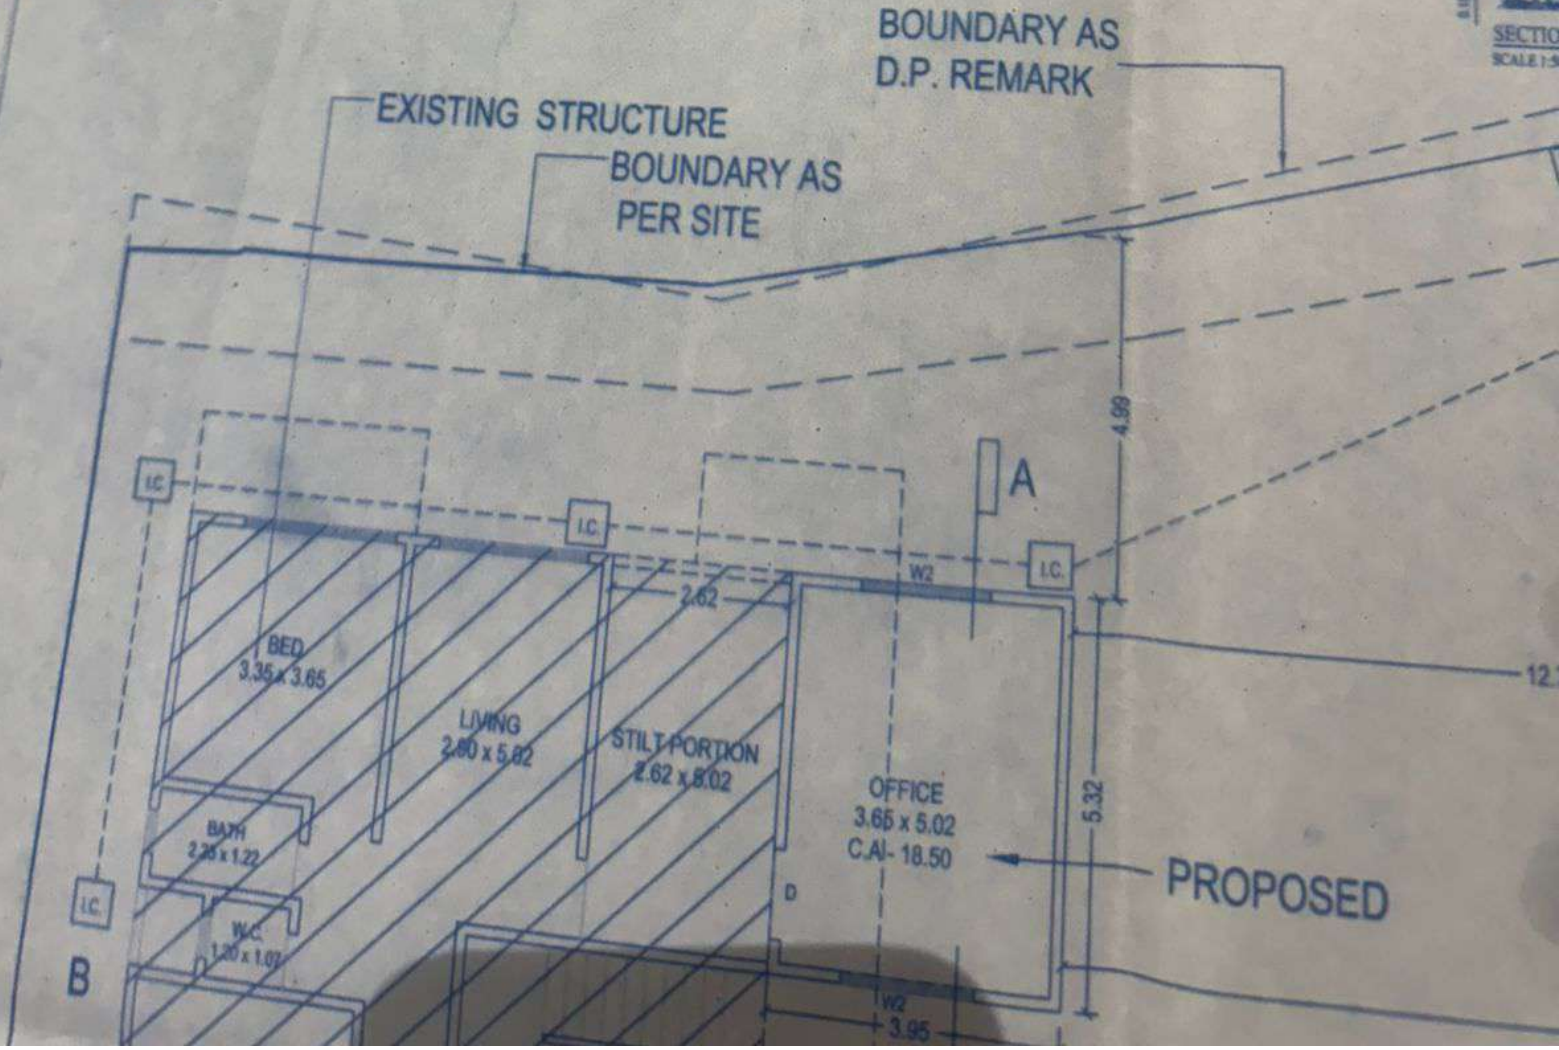

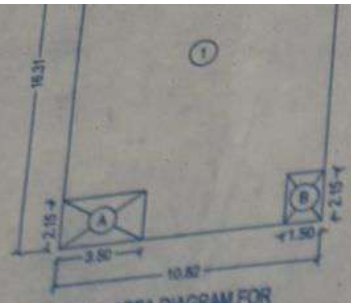

EXISTING AREA DIAGRAM FOR 1ST TO 2ND FLOOR
SCALE - 1:200

TOTAL BUILT UP AREA	=	165.71

BUILT UP AREA CALCULATION

			SQ.MT.
EXISTING GROUND FLOOR			
1	9.29 X 14.16 X 1 NO	=	131.55
TOTAL ADDITION		=	131.55

DEDUCTIONS

A	2.59 X 5.17 X 1 NO	=	13.39
TOTAL DEDUCTION		=	13.39
TOTAL BUILT UP AREA		=	118.33

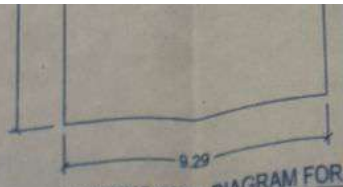

EXISTING AREA DIAGRAM FOR GROUND FLOOR
SCALE - 1:200

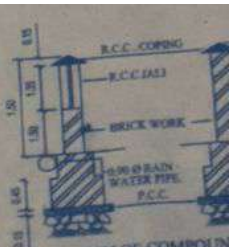

SECTION OF COMPOUN
SCALE 1:50

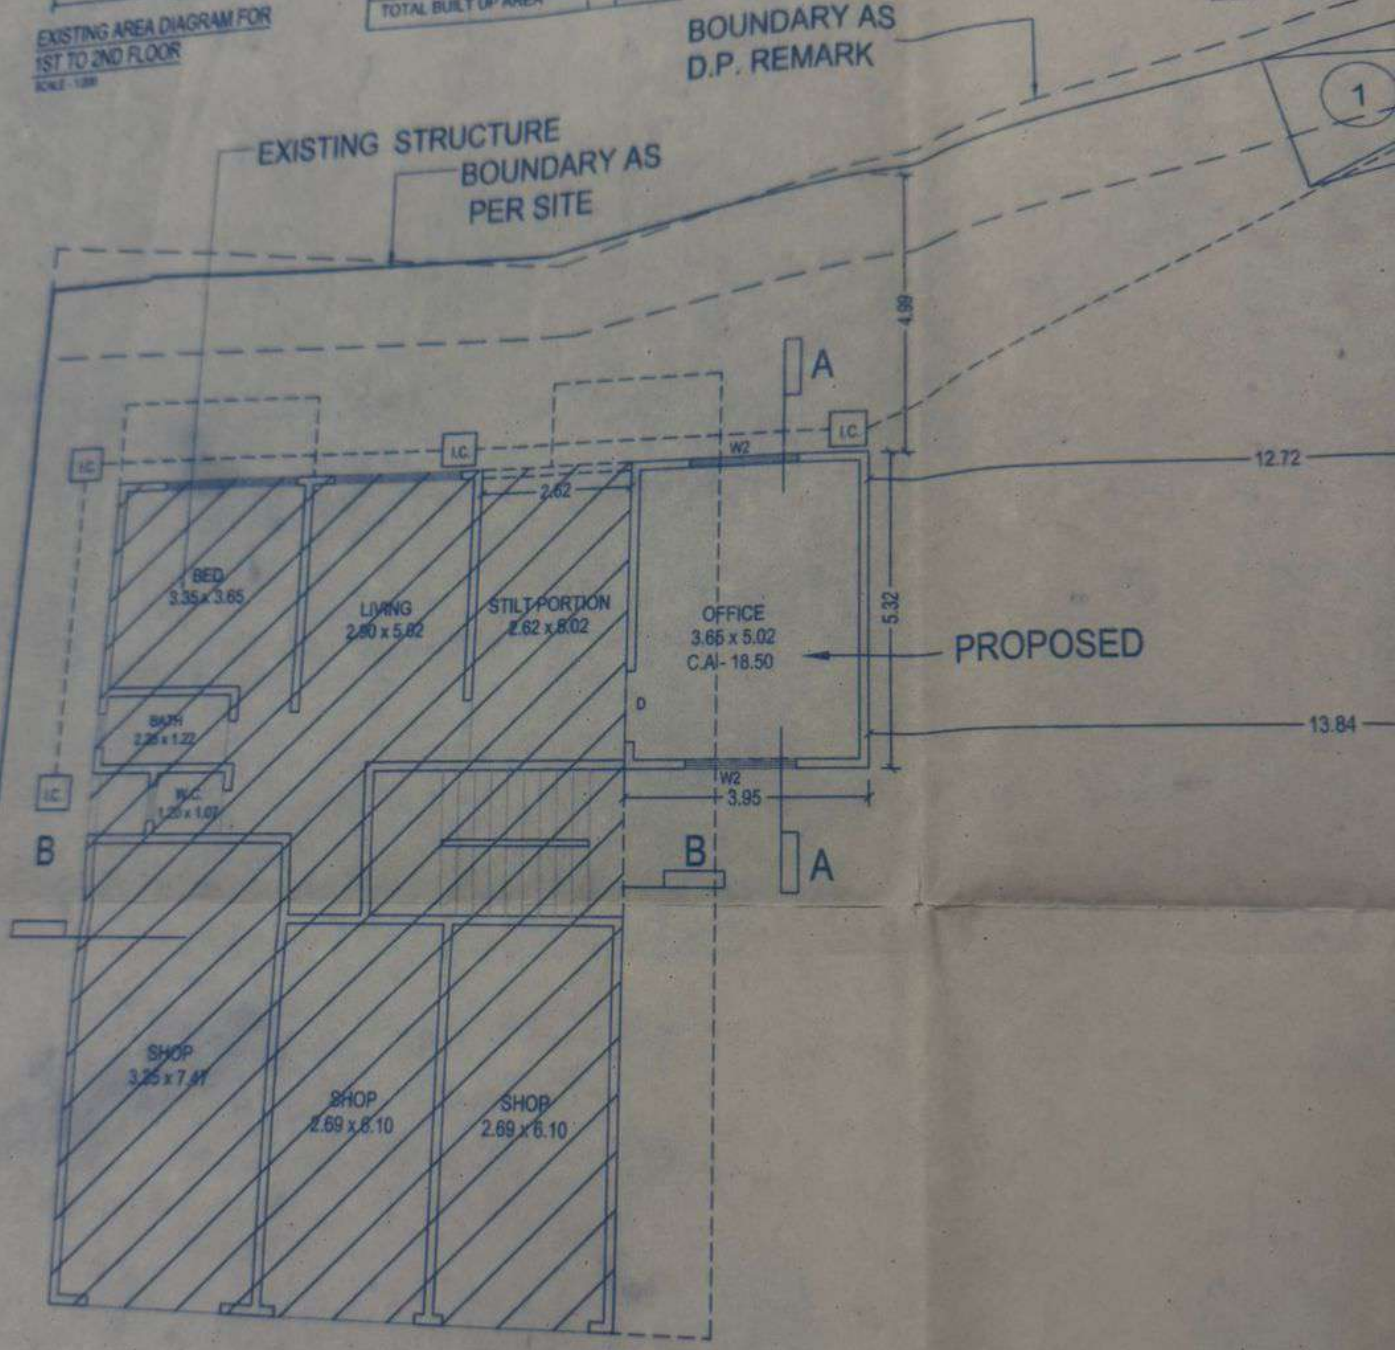

PROPOSED GROUND FLOOR PLAN.
SCALE - 1:100

SET BACK AREA

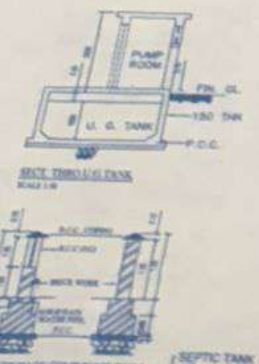

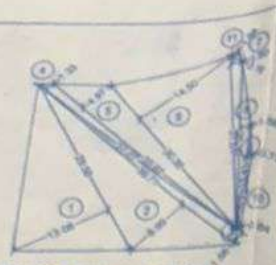

PLOT AREA DIAGRAM
SCALE- 1:500

PLOT AREA CALCULATION			SQ.MT.
1	1/2 X 26.88 X 15.06 X 1 NO	=	185.41
2	1/2 X 38.71 X 8.86 X 1 NO	=	174.57
3	1/2 X 38.71 X 1.58 X 1 NO	=	30.58
4	1/2 X 27.67 X 1.50 X 1 NO	=	20.85
5	1/2 X 30.87 X 4.97 X 1 NO	=	85.64
6	1/2 X 30.30 X 14.50 X 1 NO	=	219.29
7	1/2 X 27.01 X 1.62 X 1 NO	=	22.01
8	1/2 X 38.12 X 1.38 X 1 NO	=	26.28
9	1/2 X 15.41 X 0.73 X 1 NO	=	5.62
10	1/2 X 15.73 X 0.91 X 1 NO	=	7.15
11	1/2 X 2.56 X 1.04 X 1 NO	=	1.12
	TOTAL ADDITION	=	785.90

AREA UNDER ROAD CALCULATION

SET BACK AREA			SQ.MT.
a	1/2 X 28.30 X 6.56 X 1 NO	=	92.82
b	1/2 X 28.12 X 7.44 X 1 NO	=	104.61
	TOTAL ADDITION	=	197.43

SETBACK AREA DIAGRAM
SCALE- 1:500

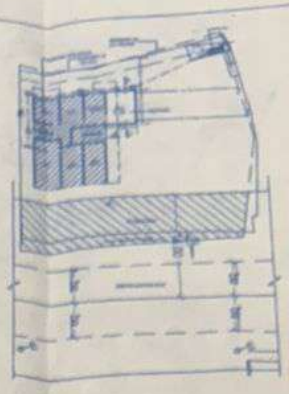

BLOCK PLAN.
SCALE - 1:500

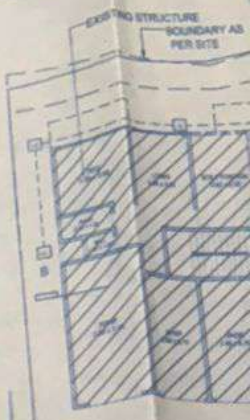

Form of Statement 1
Existing Building to be retained

Existing Building No.	Floor No.	Plinth Area	Total Floor Area of Existing Existing Building Use	Occupancy of Floors
1	2	3	4	5
NIL	G+2	108.33	449.75	G+2

Form of Statement 2
Proposed Building

Building No.	Floor No.	Total B-up Area of floor as per outer construction Line
1	2	3
1	GROUND	21.01 SQ.M.

Form of Statement 3
Area details of Apartment

Building No.	Floor No	Apartment No.	Carpet area of apartment	Area of Bal. attached to Apart.	Area of Double height terraces attached to flat.
1	2	3	4	5	6
1	GROUND	NIL	18.50	0.00	0.00

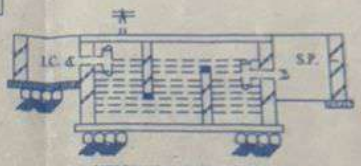

SECTION OF SEPTIC TANK
SCALE 1:50

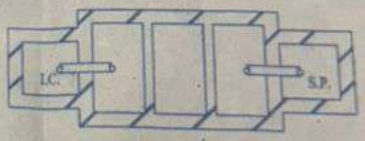

PLAN OF SEPTIC TANK
SCALE 1:50

LAYOUT PLA
SCALE - 1:200

DOORS & WINDOWS SCHEDULE

	SIZE IN MTS	AREA	DESCRIPTION OF PARTICULERS
D	1.00 X 2.10	2.1 SQMT	T.W.FRAMED FULLY PANELLED SINGLE LEAF
D1	0.90 X 2.10	1.89 SQMT	T.W.FRAMED FULLY FLUSHED SINGLE LEAF
D2	0.75 X 2.00	1.50 SQMT	T.W.FRAMED 0.25 MHIGH GLASS AT TOP,SINGLE LEAF
W	1.80 X 2.10	3.78 SQMT	ALLUMINIUM FRAME FULLY GLAZED SLIDING WINDOW
W2	1.80 X 1.20	2.16 SQMT	ALLUMINIUM FRAME FULLY GLAZED SLIDING WINDOW
V	0.80 X 0.80	0.64 SQMT	ALLUMINIUM FRAME FULLY GLAZED SLIDING WINDOW
RS	1.80 X 2.10	3.78 SQMT	ROLLING SHUTTER

BAUP AREA STATEMENT

FLOOR	EXISTING BUILT UP AREA	PROP. F.S.I.
GROUND	118.33	21.01
1ST	165.71	
2ND	165.71	
TOTAL	449.75	21.01

PARKING AREA ST

RESI.AREA

For every two tenements with each ten
having carpet area less than 30 Sq.m
For every two tenements with each ten
carpet area less than 45 Sq.m. but more
For every two tenements with each tenem
area equal to or above 45 Sq.m. but less th
For every tenement having carpet area equa
60 sq.m. but less than 90 sq.m.
For every 100 sq.m or part thereof, or fraction the

TOTAL
TOTAL PARKING REQUIRED
TOTAL PARKING PROVIDED 50 %

TOTAL PARKING REQUIRED
TOTAL CAR PARKING PROVIDED
TOTAL SCOOTER PARKING PROVIDED
BALANCE SCOOTER PARKING CONVERT IN TO COMP
COMPOSITE RATIO CAR PARKING TO CAR PARKING

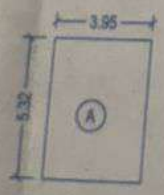

PROPOSED AREA DIAGRAM FOR GROUND FLOOR
SCALE - 1:200

BUILT UP AREA CALCULATION

PROPOSED GROUND FLOOR			SQ.MT.
A	3.95 X 5.32 X 1 NO	=	21.01
	TOTAL ADDITION	=	21.01

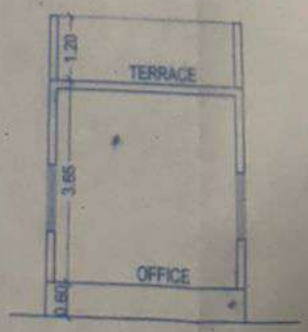

SECTION A-A
SCALE - 1:100