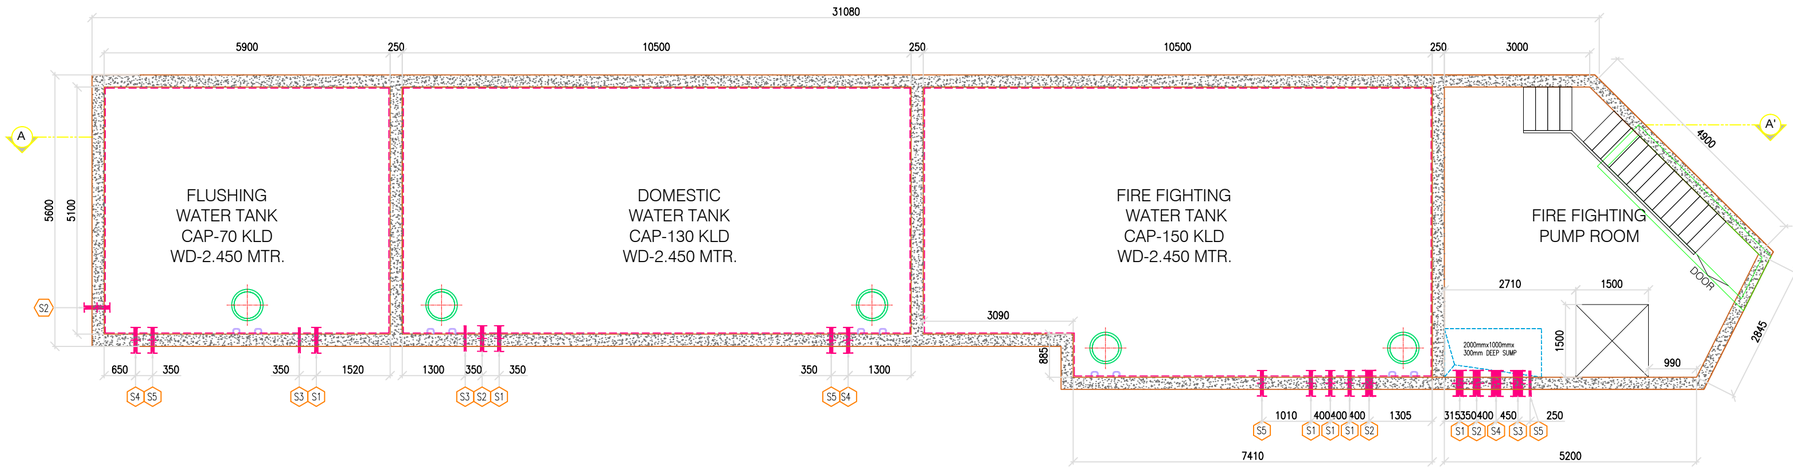

UGT PLAN

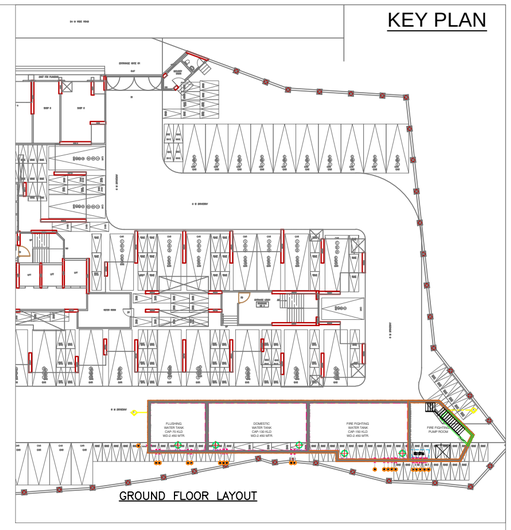

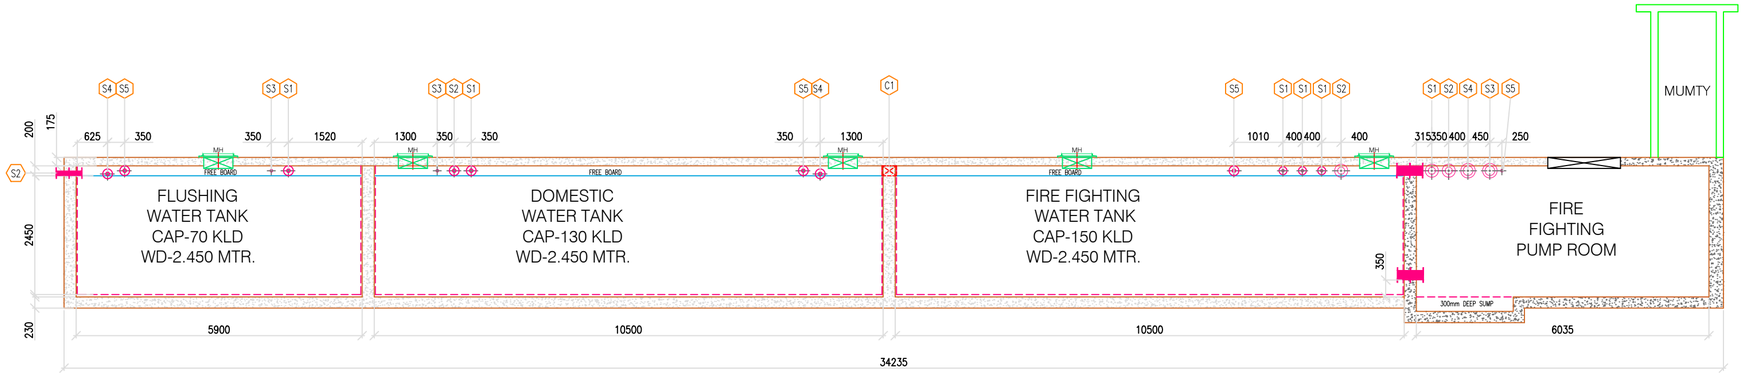

SECTION 'A'A'

THIS DRAWING IS THE PROPERTY OF ELCON ENGINEERS AND COPYRIGHT RESERVED. THIS DRAWING IS ISSUED ON CONDITION THAT IT IS NOT COPIED, REPRODUCED, RETAINED OR DISCLOSED TO ANY UNAUTHORIZED PERSON EITHER WHOLLY OR IN PART WITHOUT OUR CONSENT.

NO.	DATE	DESCRIPTION	NO.	DATE	DESCRIPTION
		REVISION DETAILS			REVISION DETAILS

CLIENT: KGI REALTY PVT LTD

ARCHITECT: --

DRAWN BY:	TTP	FOR DISCUSSION
CHECKED BY:	ASM	FOR APPROVAL
		FOR TENDER
APPROVED BY:	SDG	FOR CONSTRUCTION

STAMP & SIGNATURE:

ELCON
www.elconeng.com
B/12, Nav Dhanavanti CHS., Plot No. R-1, Sudarshan Nagar, MIDC, Dombivli (East) - 421 203.

DRAWING TITLE: UGT DETAILS

PROJECT: KOHINOOR HIGHLAND

DRAWING DATE:	SCALE:
12.04.2023	1:120
SHEET NO.: 01 OF 01	REVISION NO.: 00
DRAWING NO.: 2223-83-07	