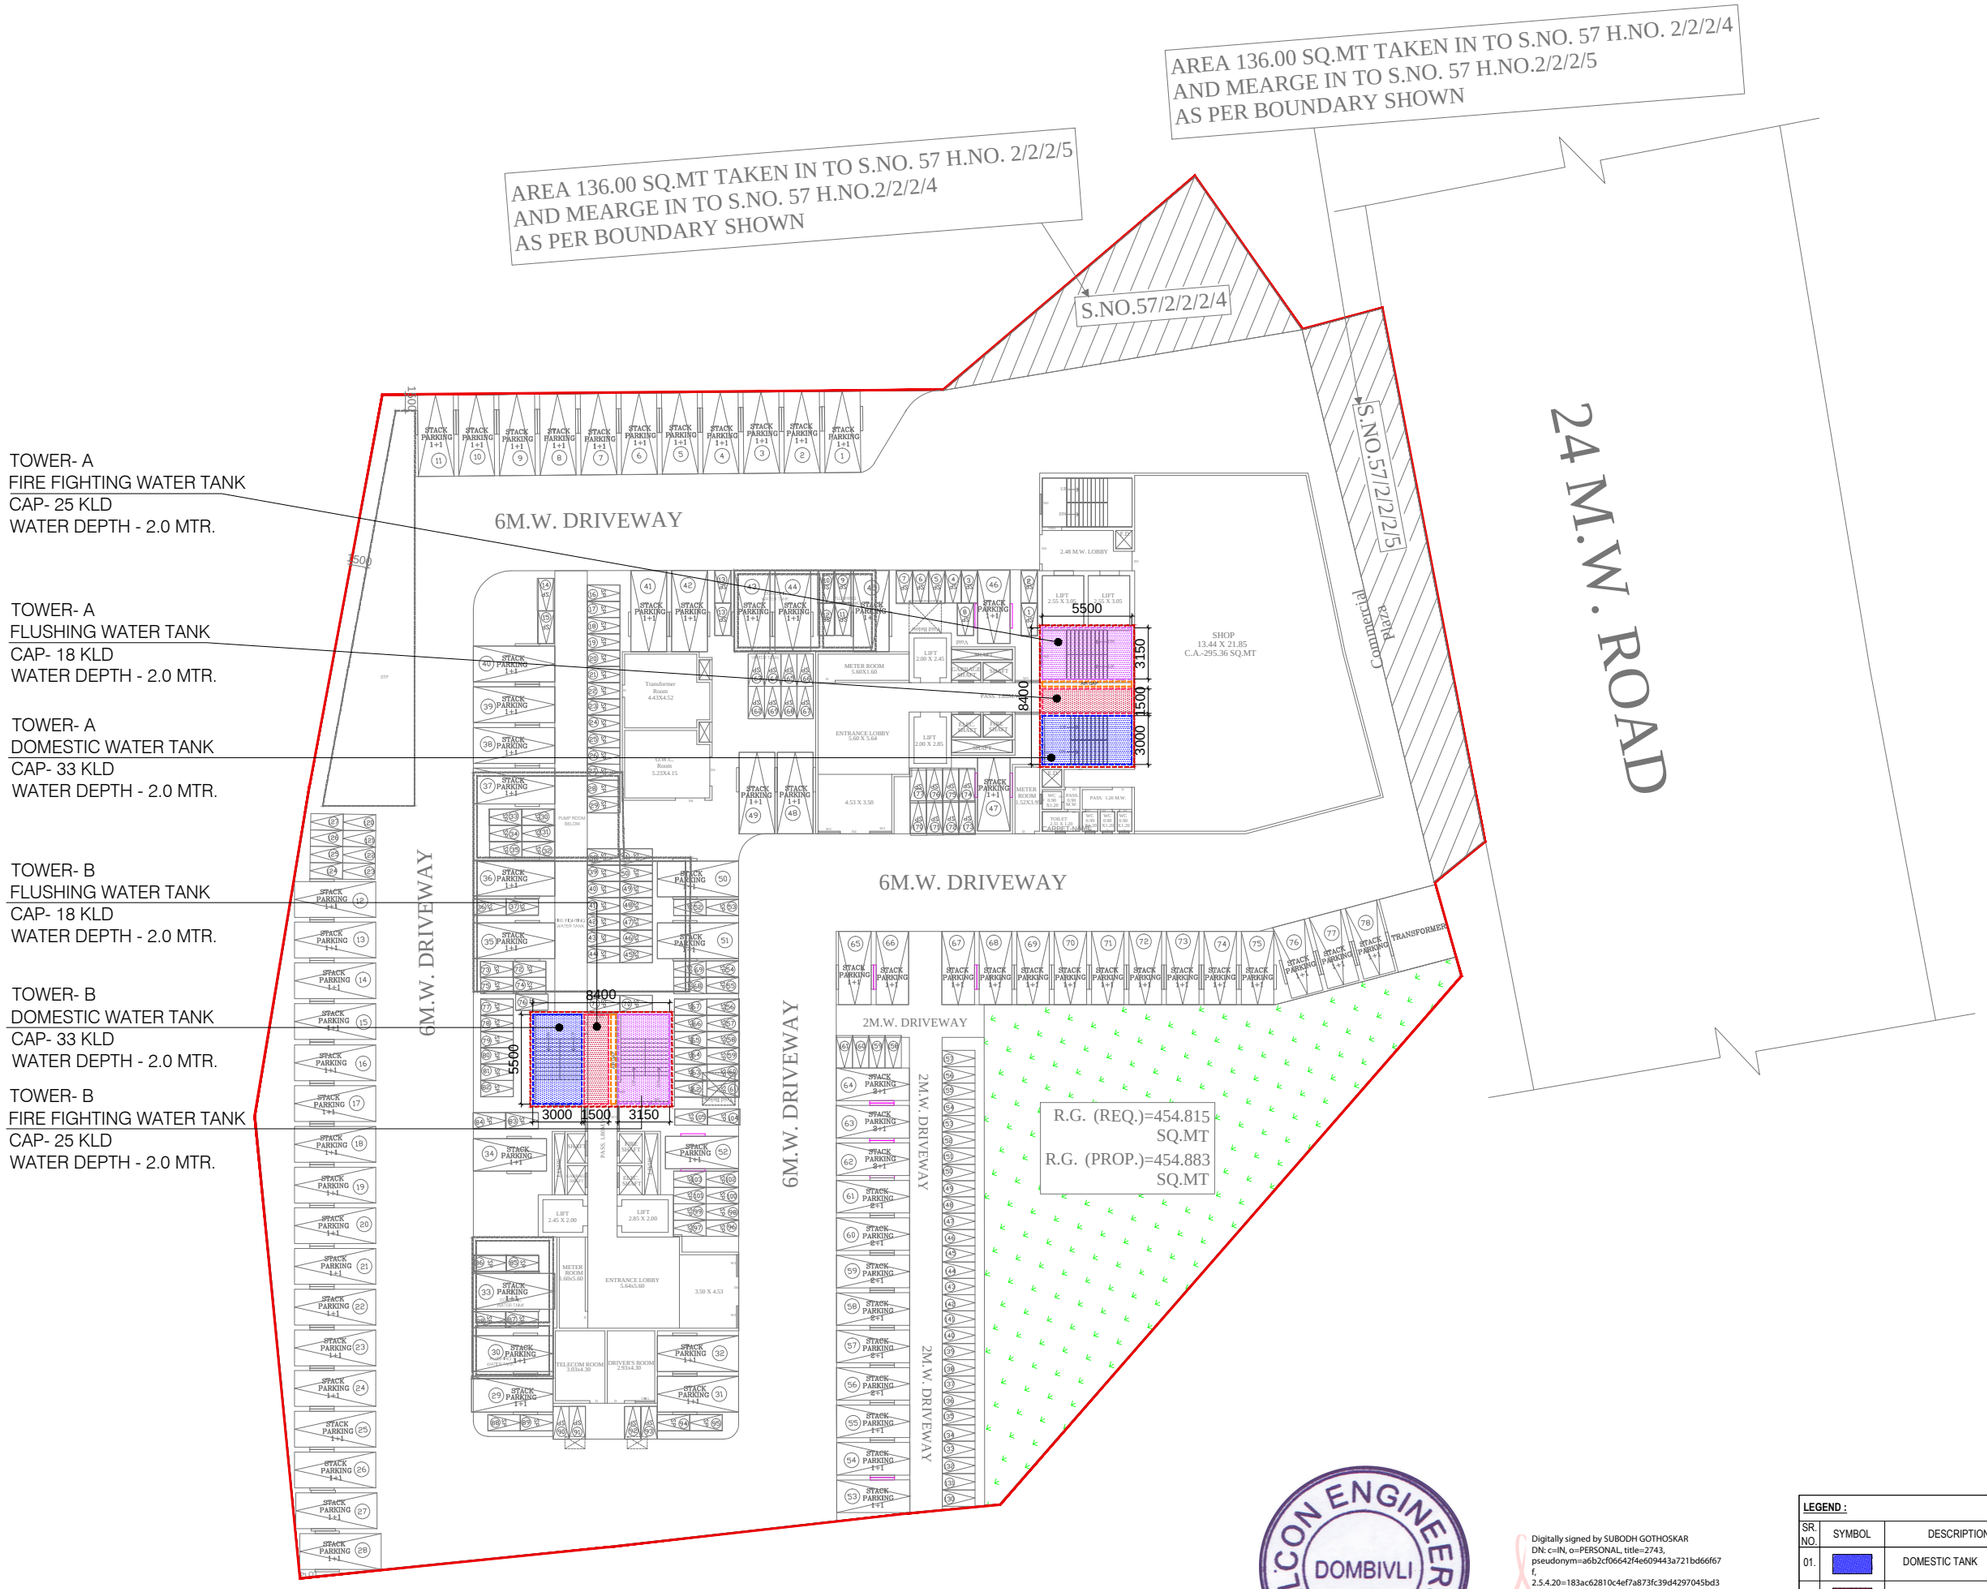

O.H. TANK DETAILS PLAN

ELCON ENGINEERS DOMBIVLI

KAR

Digitally signed by SUBODH GOTHOSKAR
DN: c=IN, o=PERSONAL, title=2743, pseudonym=a6b2cf06642f4e609443a721bd66f67f, 2.5.4.20=183ac62810c4ef7a873fc39d4297045bd3a4e2852f3a34bf1bd70cb479d7ad8a, postalCode=421301, st=Maharashtra, serialNumber=ef390763b4f8c69191fe25800f5aca39ca0755c25ec0b0546949141687dd8988, cn=SUBODH GOTHOSKAR
Date: 2026.03.12 14:34:12 +05'30'

LEGEND :

SR. NO.	SYMBOL	DESCRIPTION
01.		DOMESTIC TANK
02.		RWH TANK
03.		FIRE TANK
05.		PUMP ROOM

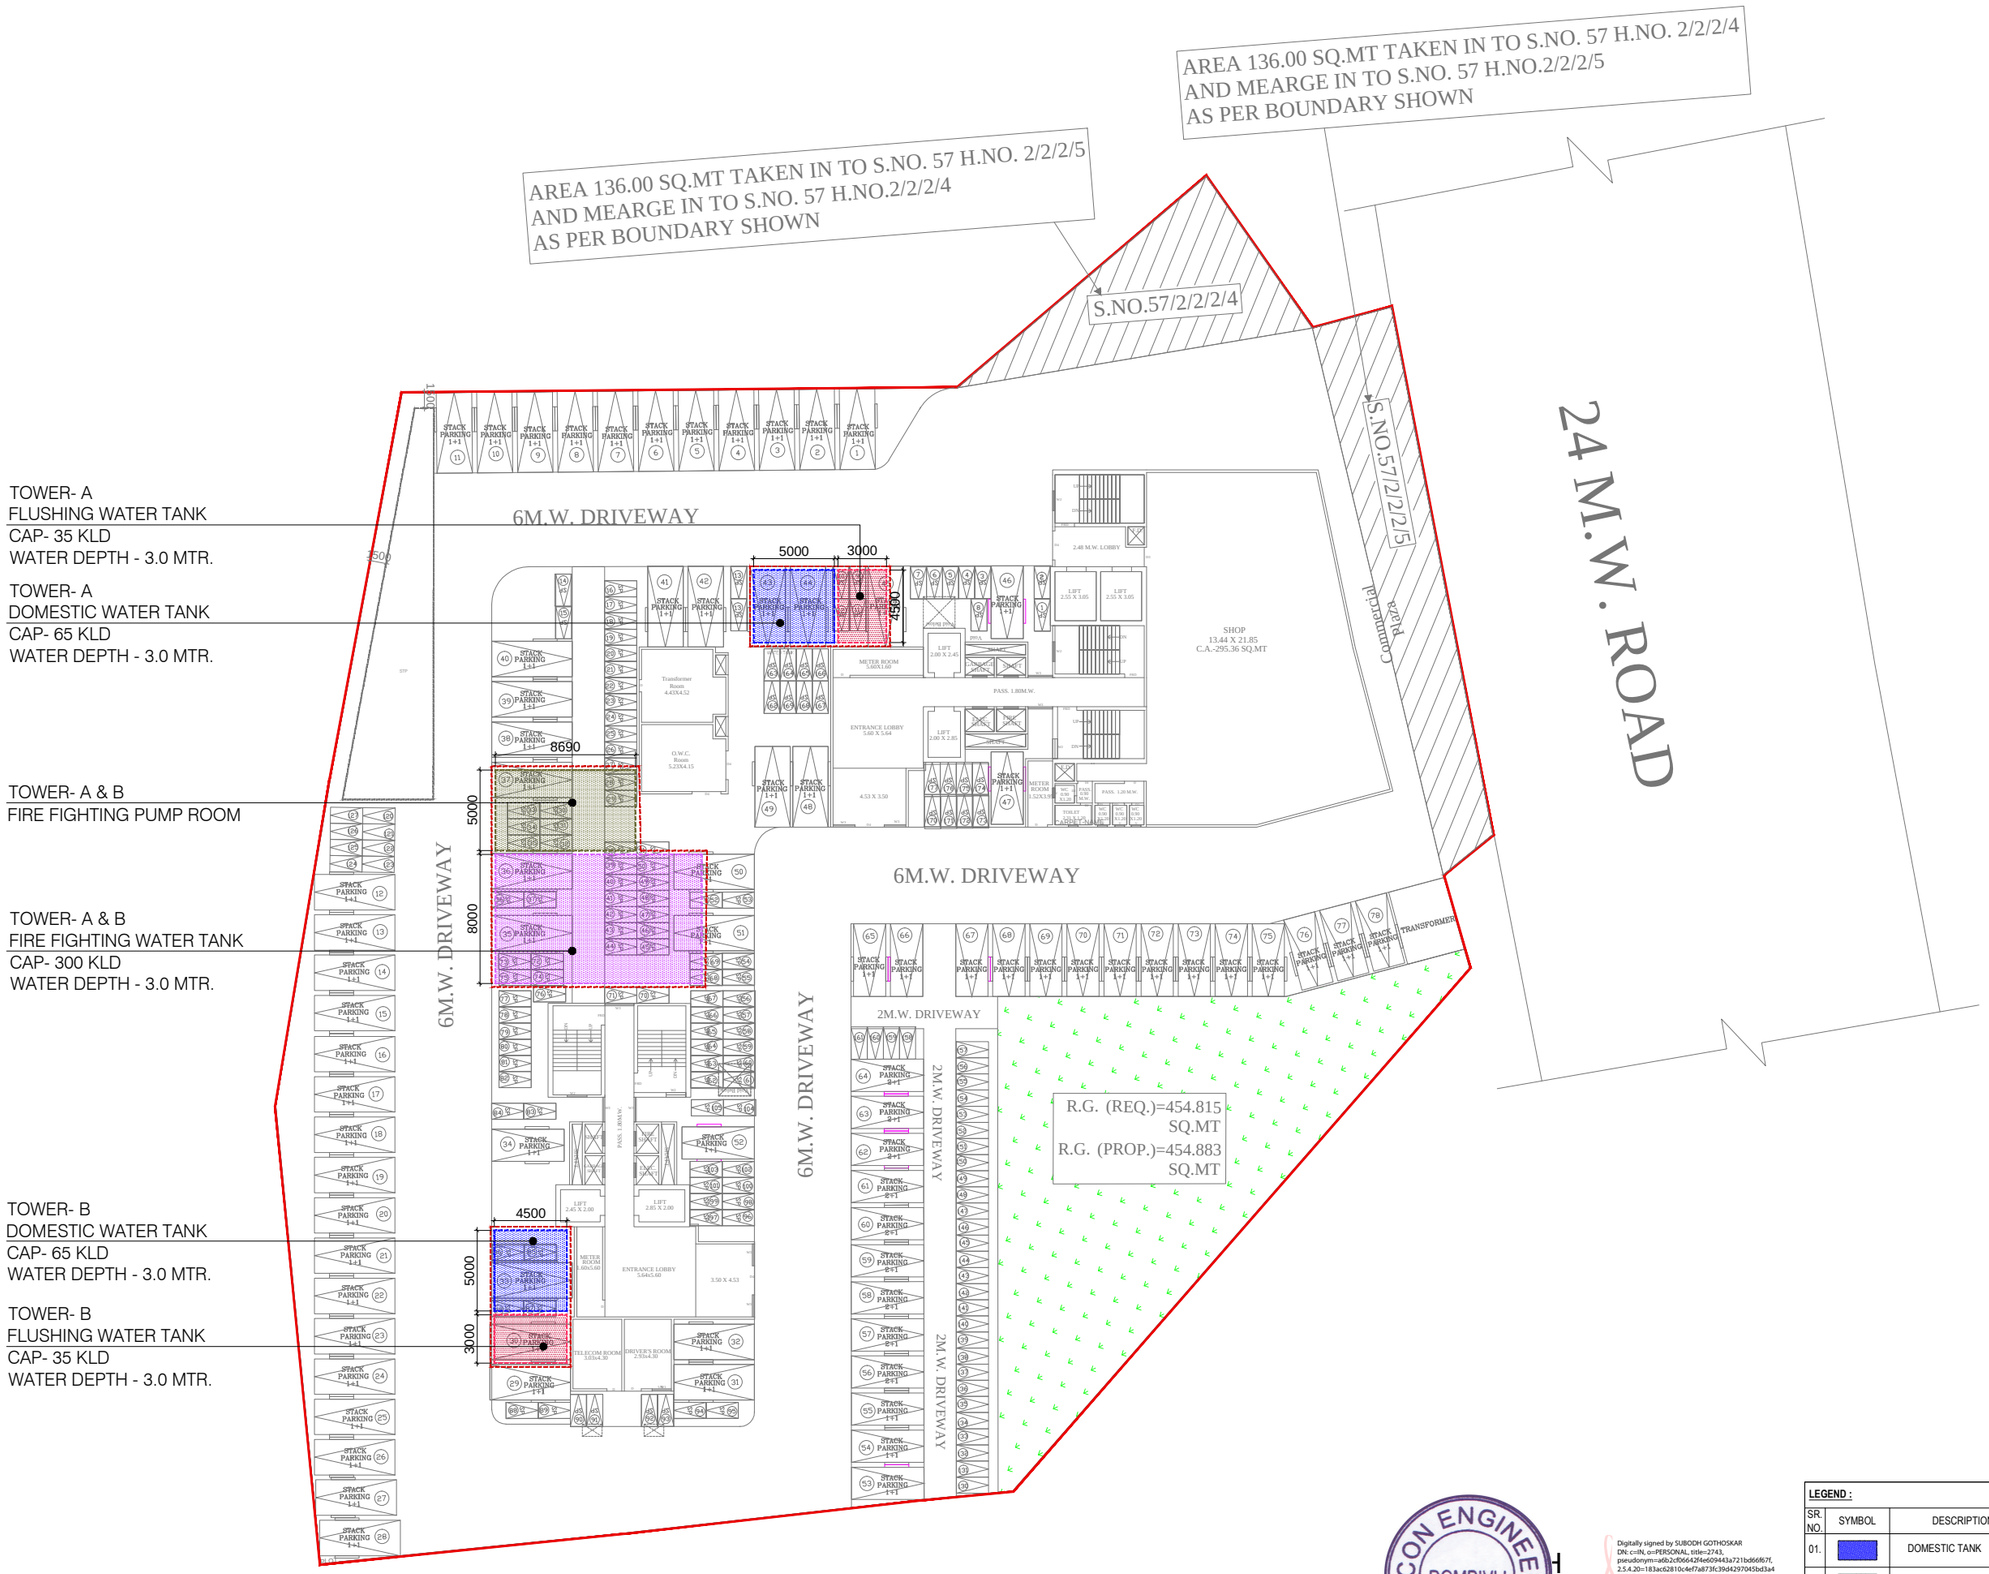

U.G.TANK DETAILS PLAN

ELCON ENGINEERS DOMBIVLI

Digitally signed by SUBODH GOTHOSKAR
DN: c=IN, o=PERSONAL, title=2743, pseudonym=a6b2cf06642f4e609443a721bd66f67f, 2.5.4.20=183ac62810c4ef7a873fc39d4297045bd3a4e2852f3a34bf1bd70cb479d7ad8a, postalCode=421301, st=Maharashtra, serialNumber=ef390763b4ffbc691916c25800f5aca39ca0755c25ec0b054649491416fdd8988, cn=SUBODH GOTHOSKAR
Date: 2026.03.12 14:34:57 +05'30'

LEGEND :

SR. NO.	SYMBOL	DESCRIPTION
01.		DOMESTIC TANK
02.		RWH TANK
03.		FIRE TANK
05.		PUMP ROOM

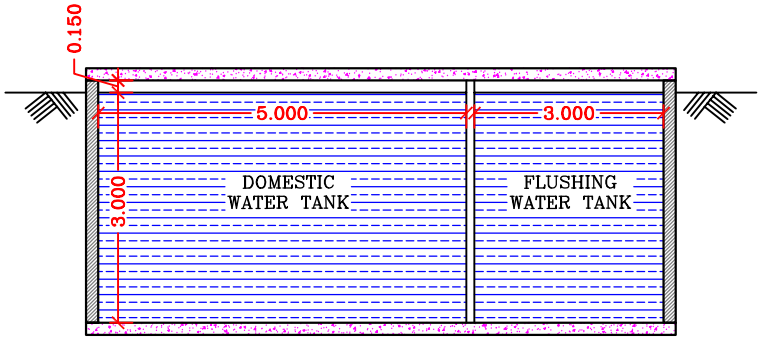

SECTION AA'

SCALE 1:100

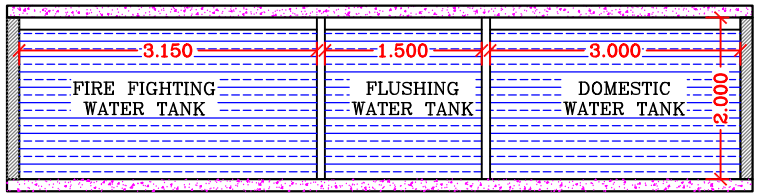

SECTION AA'

SCALE 1:100

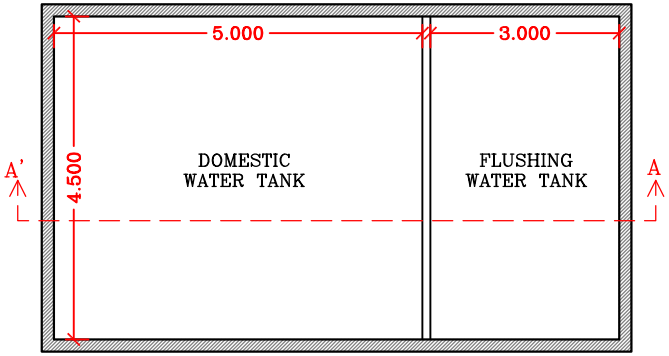

UNDER GROUND WATER TANK PLAN

TOWER C SCALE 1:100

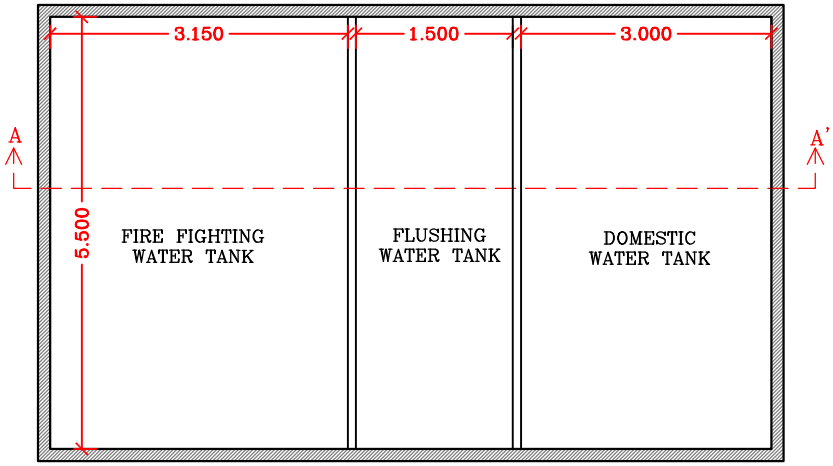

OVER HEAD WATER TANK PLAN

TOWER C SCALE 1:100

NAME OF ARCHITECT : TEJAS ANIL NIRGUDE PROJECT NAME : MEHARNAGAR	DATE 13-03-2026	SCALE AS SHOWN	LOGO	DESCRIPTION OF PROJECT : PROPOSED BUILDING ON (NEW) C.T.S. NO. 340,343,344,345,351,352, 353,356,357,358,359,360,(OLD) S.NO.59/3/A,57/2/2/2/5,59/2/C AT VILLAGE- VADEGHAR, TALUKA-KALYAN, DIST.-THANE