BLDG.NO.-01
FIRE FIGHTING WATER TANK
CAP- 150 KLD
WATER DEPTH - 3.0 MTR.

BLDG.NO.-01
DOMESTIC WATER TANK
CAP- 70 KLD
WATER DEPTH - 3.0 MTR.

BLDG.NO.-01
FIRE FIGHTING PUMP ROOM

BLDG.NO-01
FLUSHING WATER TANK
CAP- 35 KLD
WATER DEPTH - 3.0 MTR.

LEGEND :

SR. NO.	SYMBOL	DESCRIPTION
01.		DOMESTIC TANK
02.		FLUSHING TANK
03.		FIRE TANK
04.		PUMP ROOM

U.G.TANK DETAILS PLAN

SUBODH GOTHOSKAR

Digitally signed by SUBODH GOTHOSKAR
DN: c=IN, o=PERSONAL, title=2743, pseudonym=a6b2cf066424fed09443a721bd66f67f, 2.5.4.20=183ac62810e4ef7a873fc39d429704 5bd3a4e285 2f3a3 4bf1bd70c847947ed8a, postalCode=421301, st=Maharashtra, serialNumber=ef390763b4f8c6919 1fe25800f5aca39ca0755c25 ecfbc0548949141687dd8988, cn=SUBODH GOTHOSKAR
Date: 2026.03.21 13:47:41 +05'30'

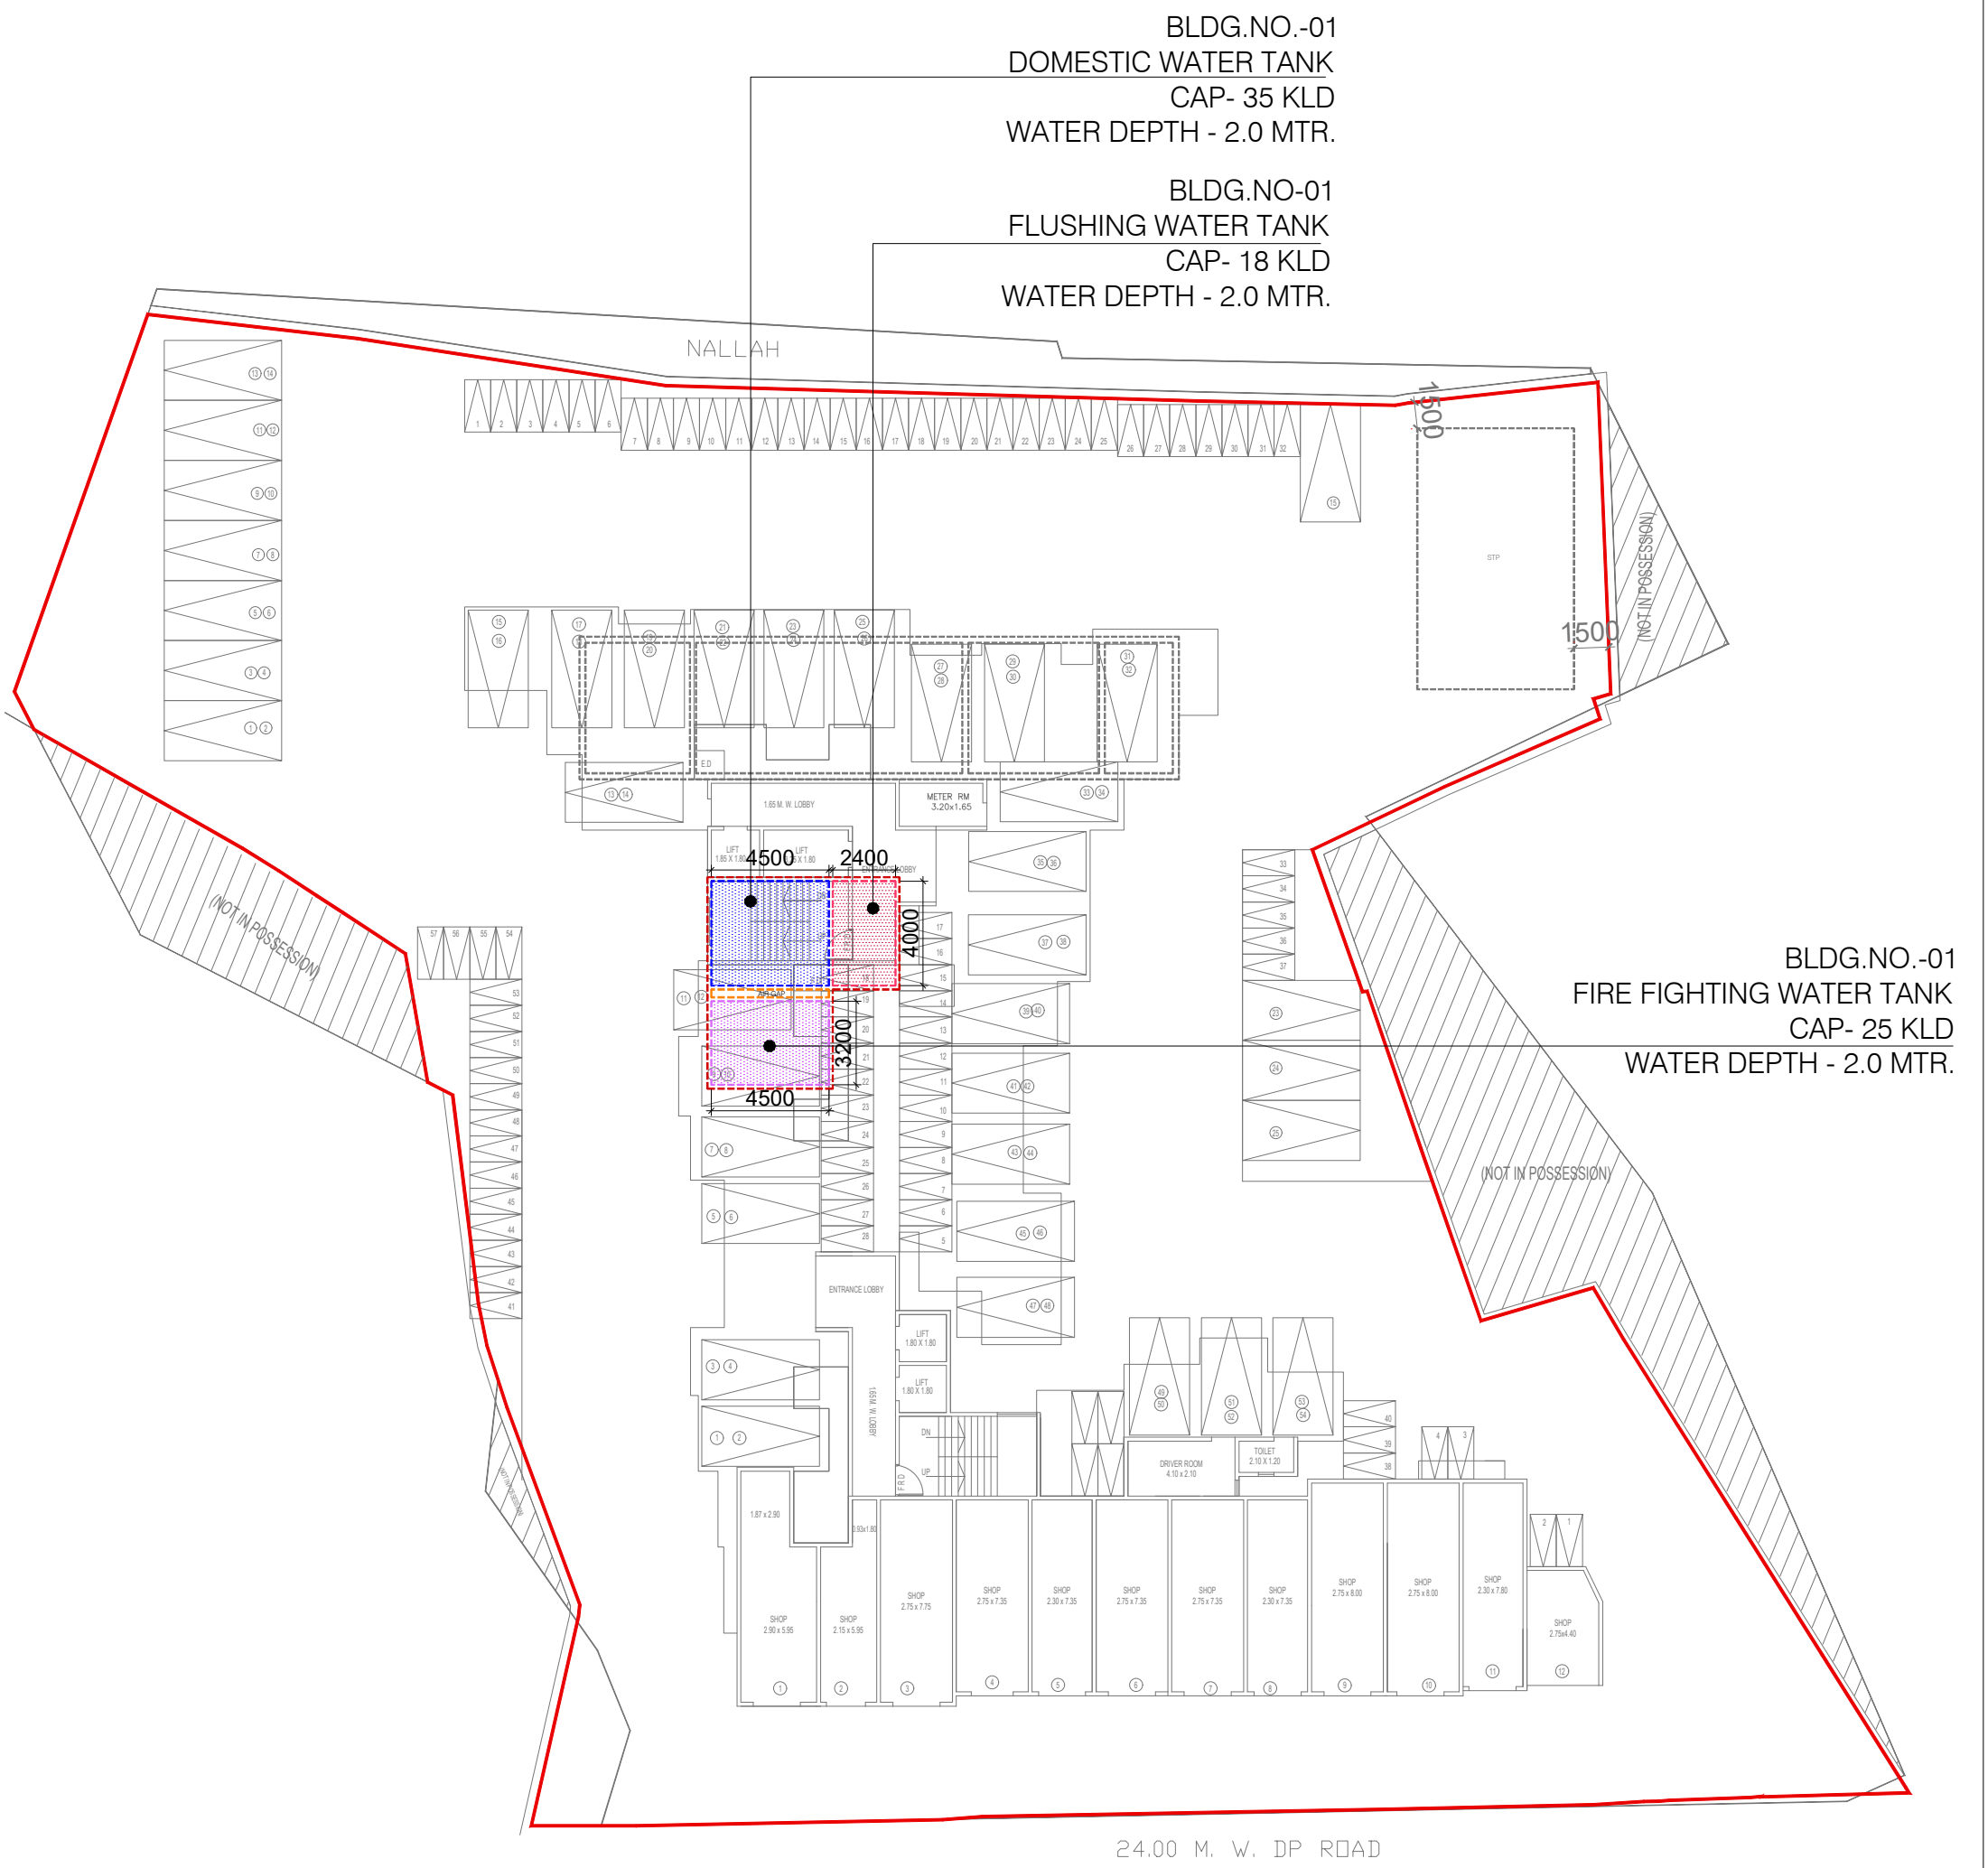

LEGEND :

SR. NO.	SYMBOL	DESCRIPTION
01.		DOMESTIC TANK
02.		FLUSHING TANK
03.		FIRE TANK

O.H. TANK DETAILS PLAN

SUBODH GOTHOSKAR

Digitally signed by SUBODH GOTHOSKAR
DN: c=IN, o=PERSONAL, title=2743, pseudonym=ab2cf0664214e609443a721bd66f67f, 2.5.4.20=183ac62810c4ef7a873fc39d4297045bd3a4e2852f3a34bf1bd70cb479d7ad8a, postalCode=421301, st=Maharashtra, serialNumber=ef390763b4f8c69191fe25800f5aca39c a1d753c25ec5b0546949141687dd898b, cn=SUBODH GOTHOSKAR
Date: 2026.03.21 13:48:07 +05'30'